


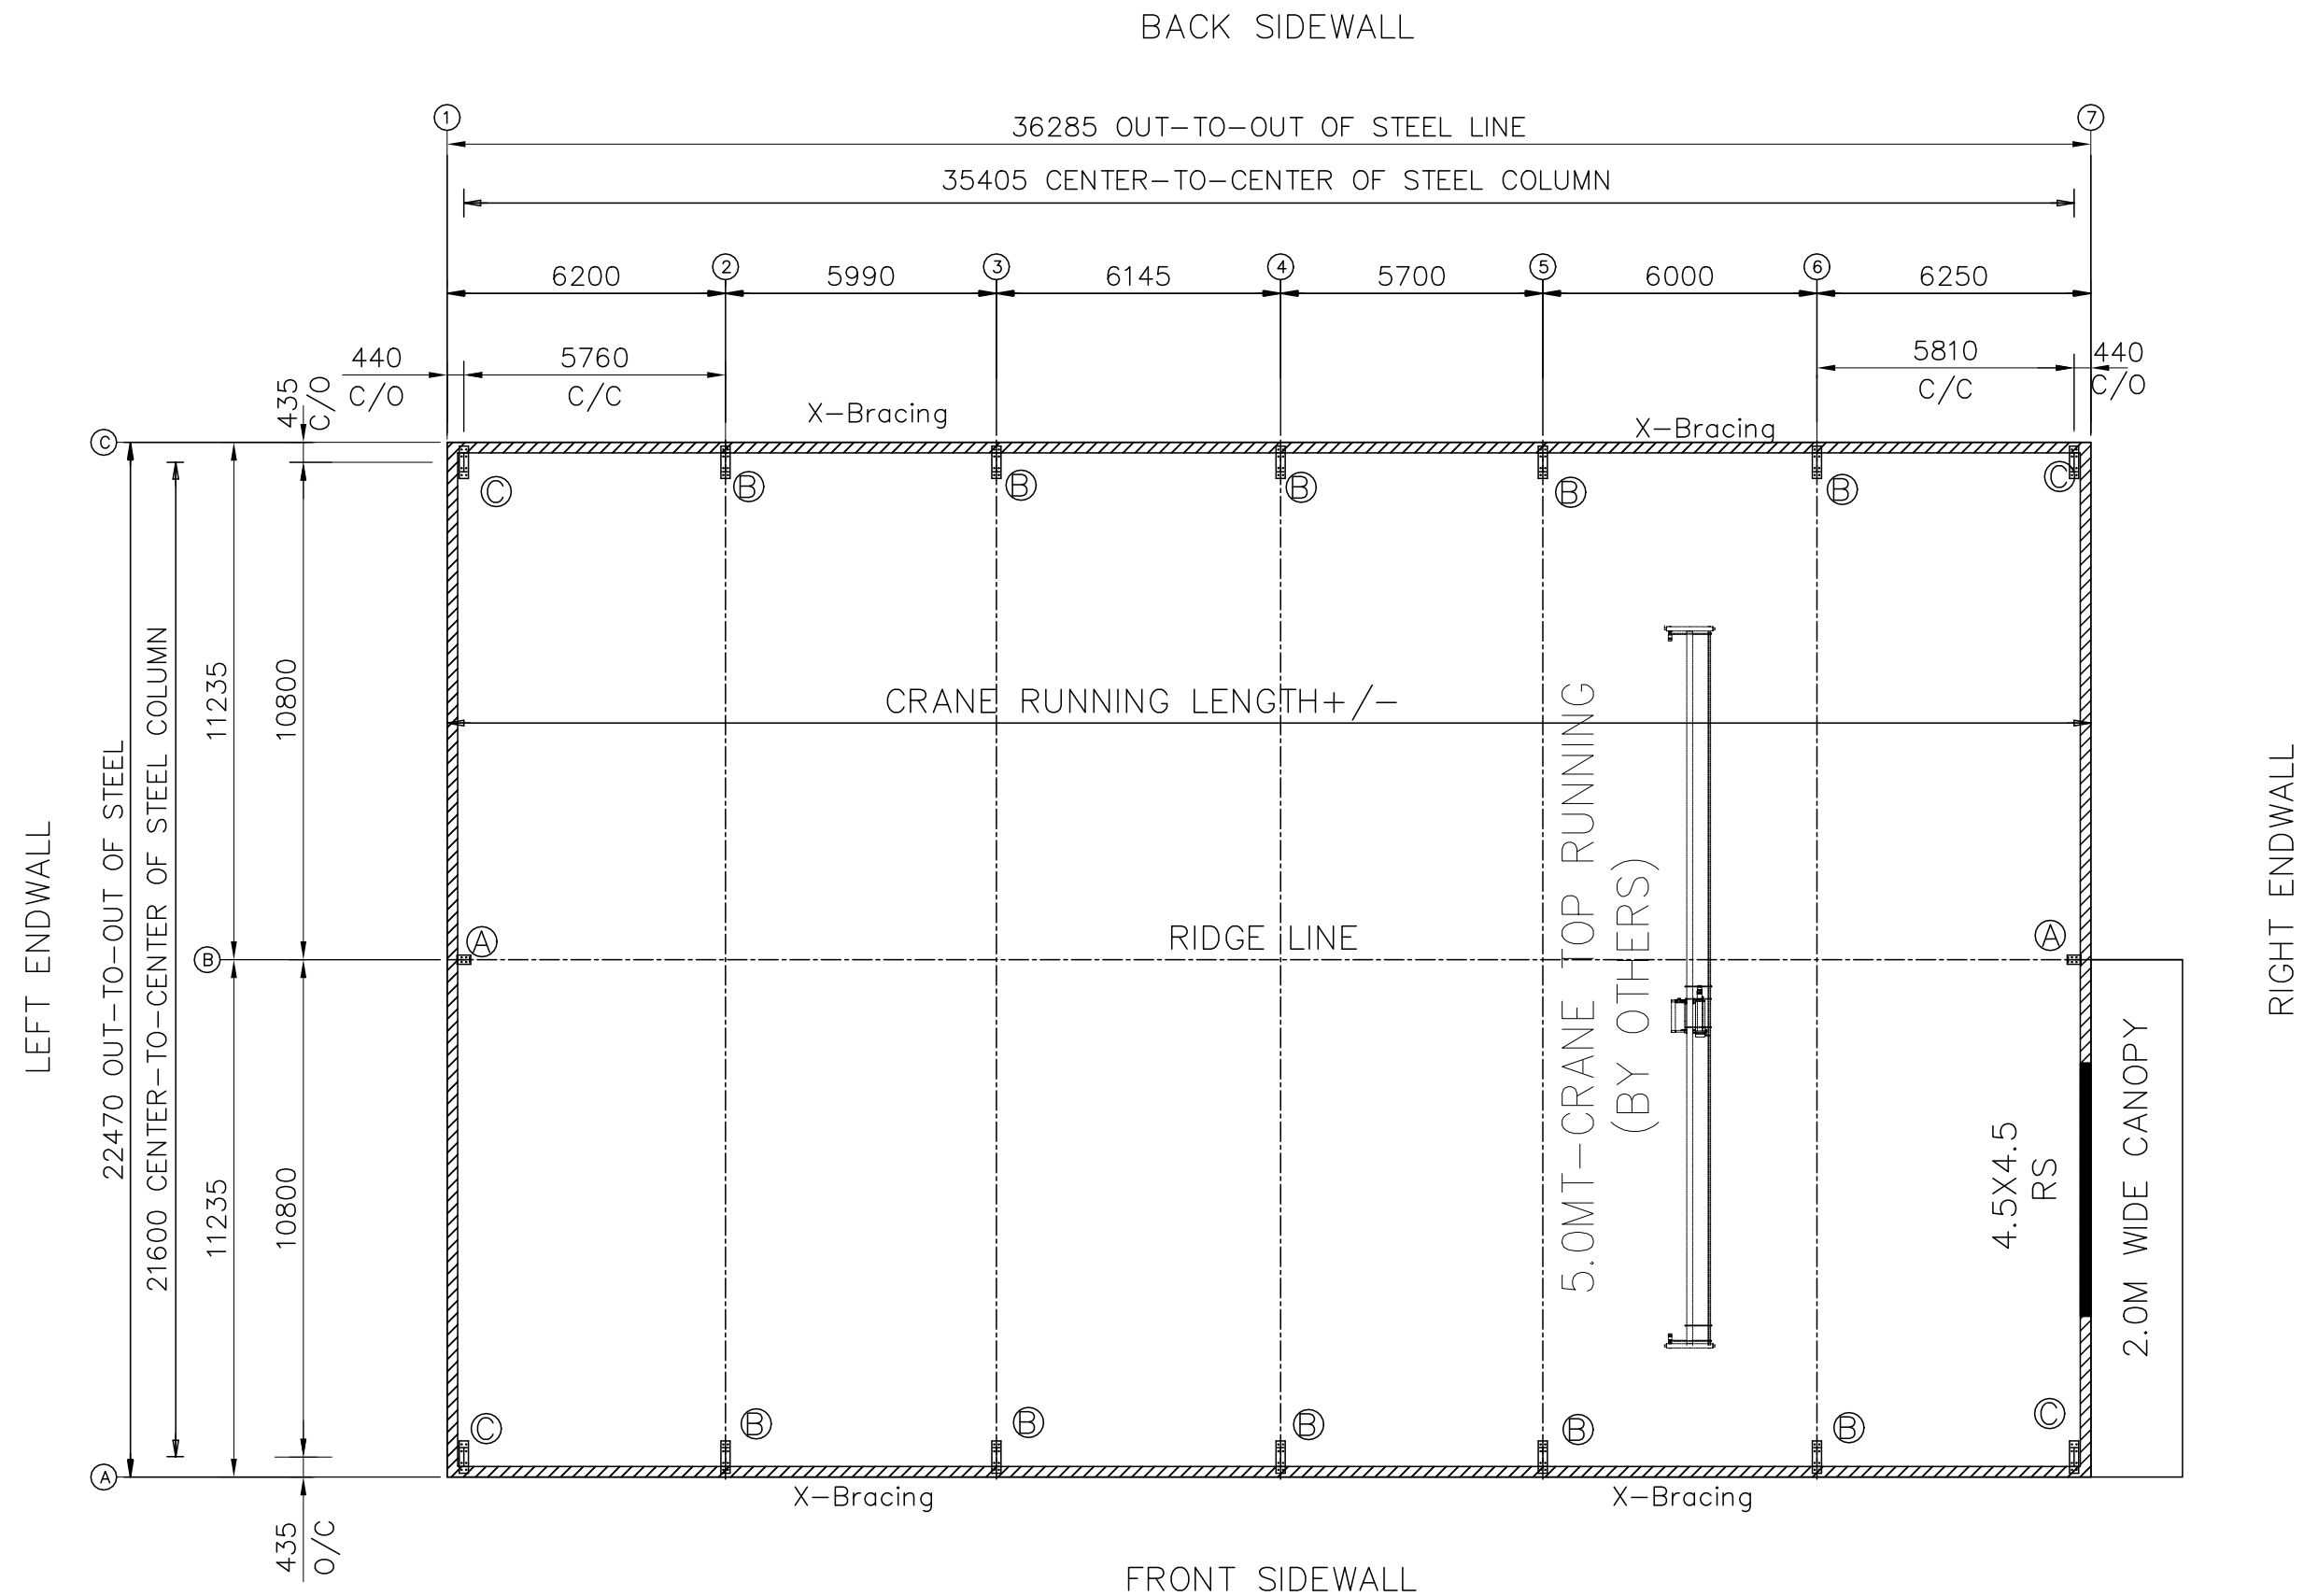

ANCHOR BOLT PLAN

NOTE: All Base Plates @ 0 (U.N.)



2.5M B/W AND ABOVE SHEETING

NOTE-THE DRAWING ARE INTENDED SOLELY FOR APPROVAL PURPOSES. CERTAIN PARTS OR DIMENSIONS MAY NOT BE TO SCALE AND THEREFORE MUST NOT BE USED FOR CONSTRUCTION OR ANY OTHER PURPOSE

RECLA INTERNATIONALS PRIVATE LIMITED

PROJECT	Proposed Warehouse	ANCHOR BOLT PLAN		
ID	C323-153	DESIGN: AAB	DRAFT: AAB	CHECK: VVJ
PROJECT ADDRESS	PUNE	DATE: 09/JUN/2025		
		C323-153_A01		



RECLA