


EXTENSION/CANOPY BOLTS				
ROOF PLAN				
MARK	QUAN	TYPE	DIA	LENGTH
EB-1	8	Gr8.8	20	90
EB-3	8	Gr8.8	20	90

MEMBER TABLE		
ROOF PLAN		
MARK	PART	LENGTH
EB-1	BEAM	2473
EB-3	BEAM	2031
P-1	200Z	6570
P-2	200Z	6740
P-3	200Z	6480
P-4	200Z	6980
P-5	200Z	6620
P-6	200Z	6620
P-7	200Z	6570
P-8	200Z	6620
P-9	250Z	11430
E-1	200Z	6570
E-2	200Z	6740
E-3	200Z	6480
E-4	200Z	6980
E-5	200Z	6620
E-6	200Z	6620
E-7	200Z	6570
E-8	200Z	6620
E-9	250Z	11435
CB-5	ROD20	8300
CB-6	ROD20	7580
CB-7	ROD20	8210
CB-8	ROD20	7480
SP-1	SROD12	697
SI-1	SROD12	1670
SI-2	SROD12	955
SE-1	SROD12	1590
SI-	SROD12	865

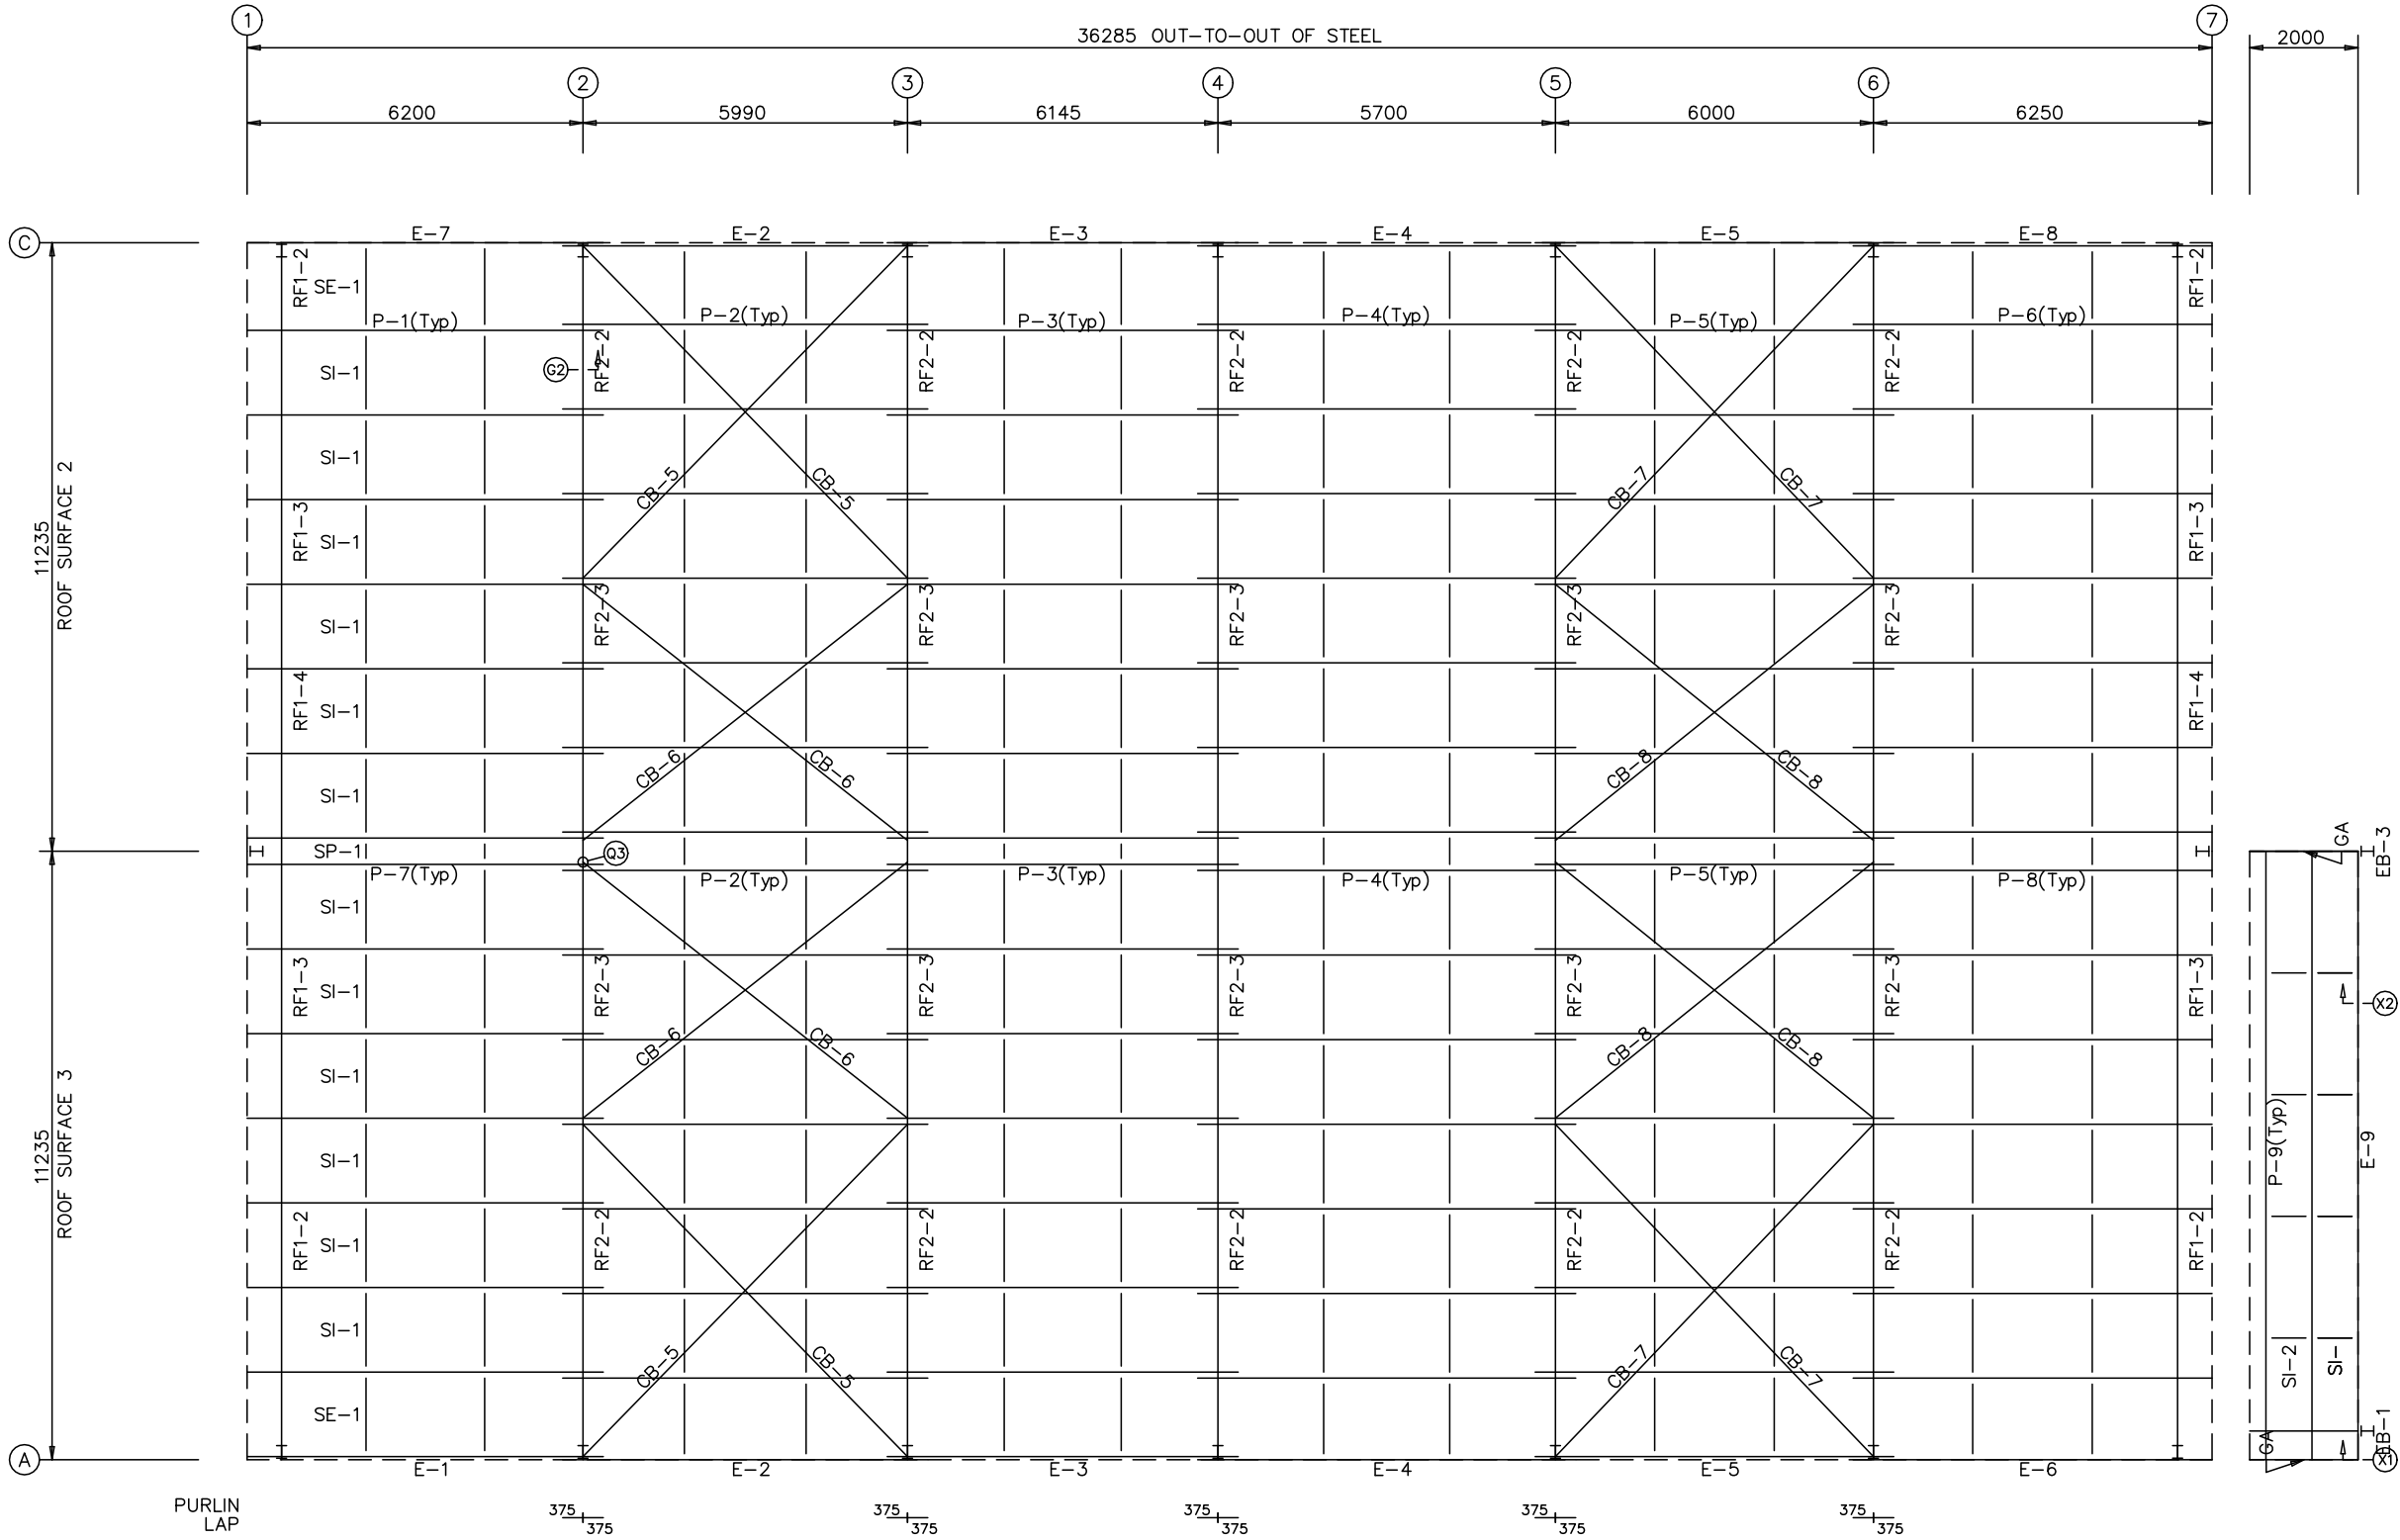

COLUMNS & RAFTERS MARKING PLAN

RECLA INTERNATIONAL PRIVATE LIMITED				
PROJECT	Proposed Warehouse	ROOF FRAMING		
ID	C323-153	DESIGN: AAB	DRAFT: AAB	CHECK: VVJ
PROJECT ADDRESS	PUNE	DATE: 23/JUL/2025		



RECLA