



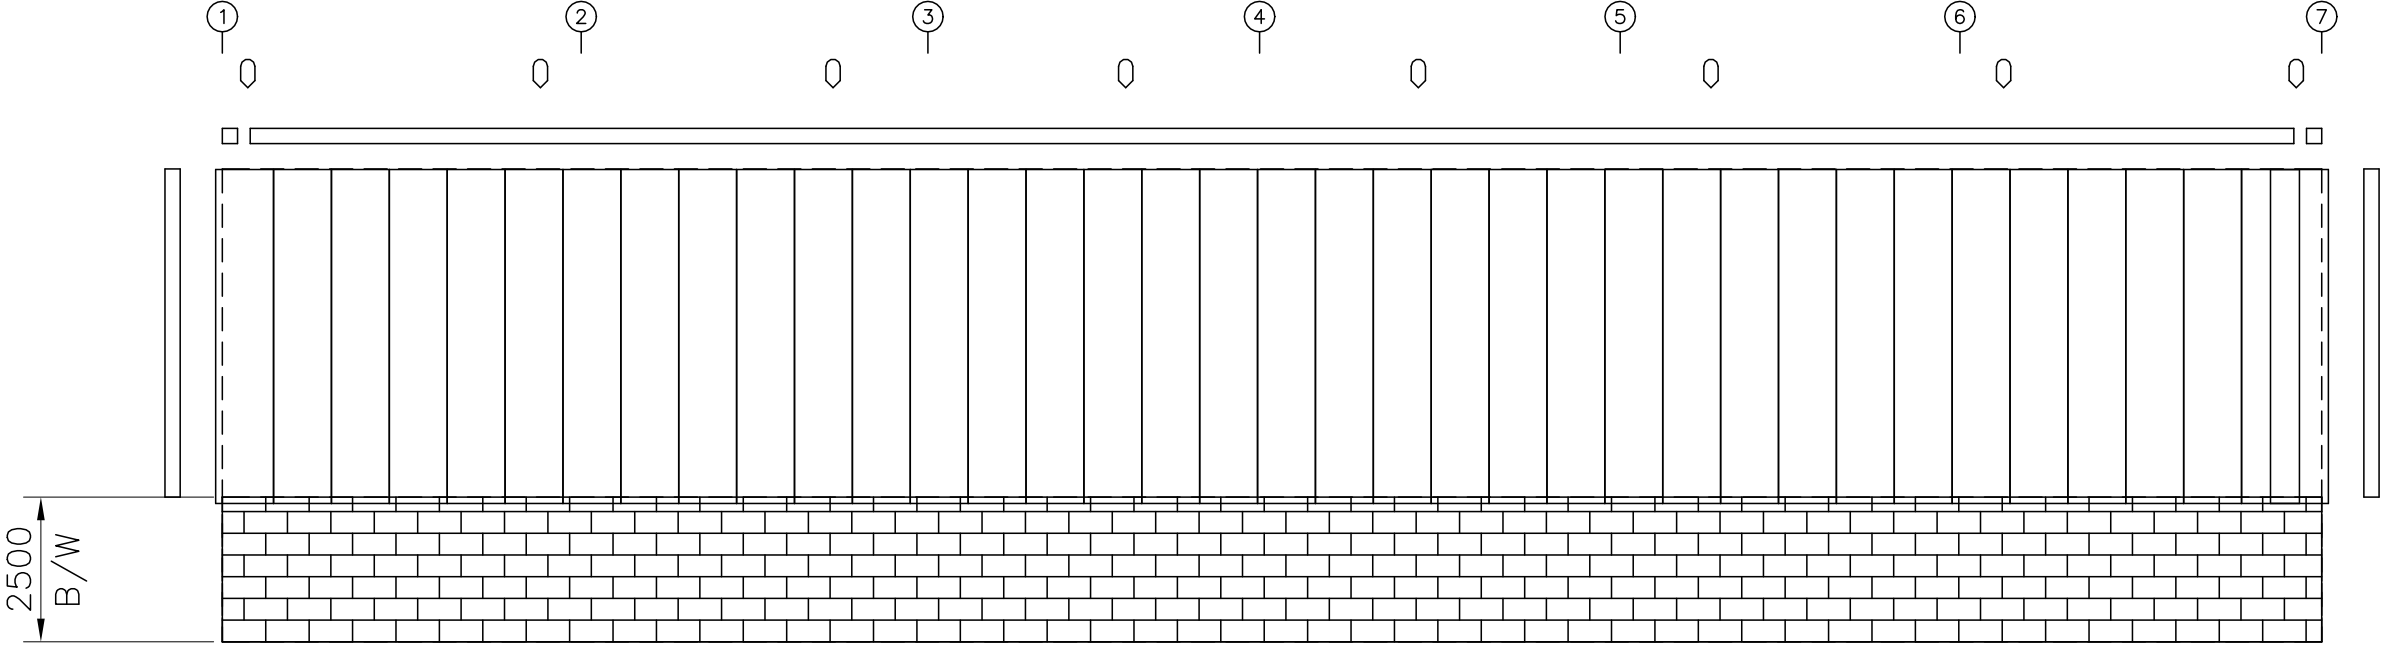

SIDEWALL SHEETING & TRIM: FRAME LINE A

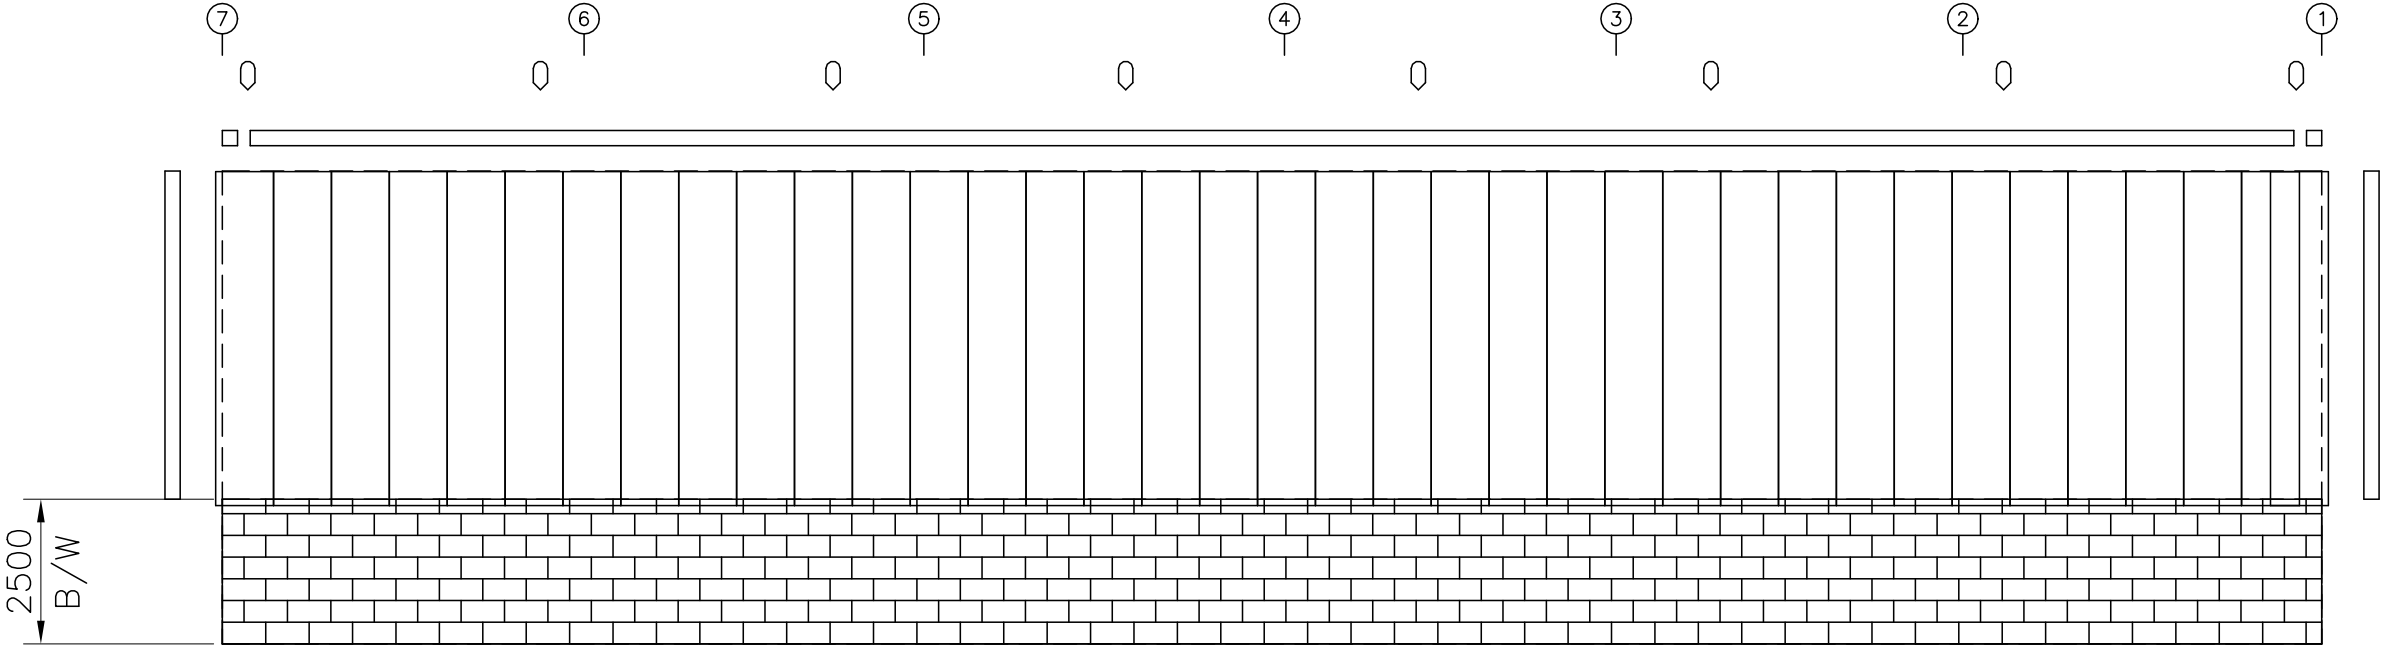

SIDEWALL SHEETING & TRIM: FRAME LINE C



RECLA

RECLA INTERNATIONAL PRIVATE LIMITED				
PROJECT	Proposed Warehouse	SIDEWALL FRAMING		
ID	C323-153	DESIGN: AAB	DRAFT: AAB	CHECK: VVJ
PROJECT ADDRESS	PUNE	DATE: 23/JUL/2025		