



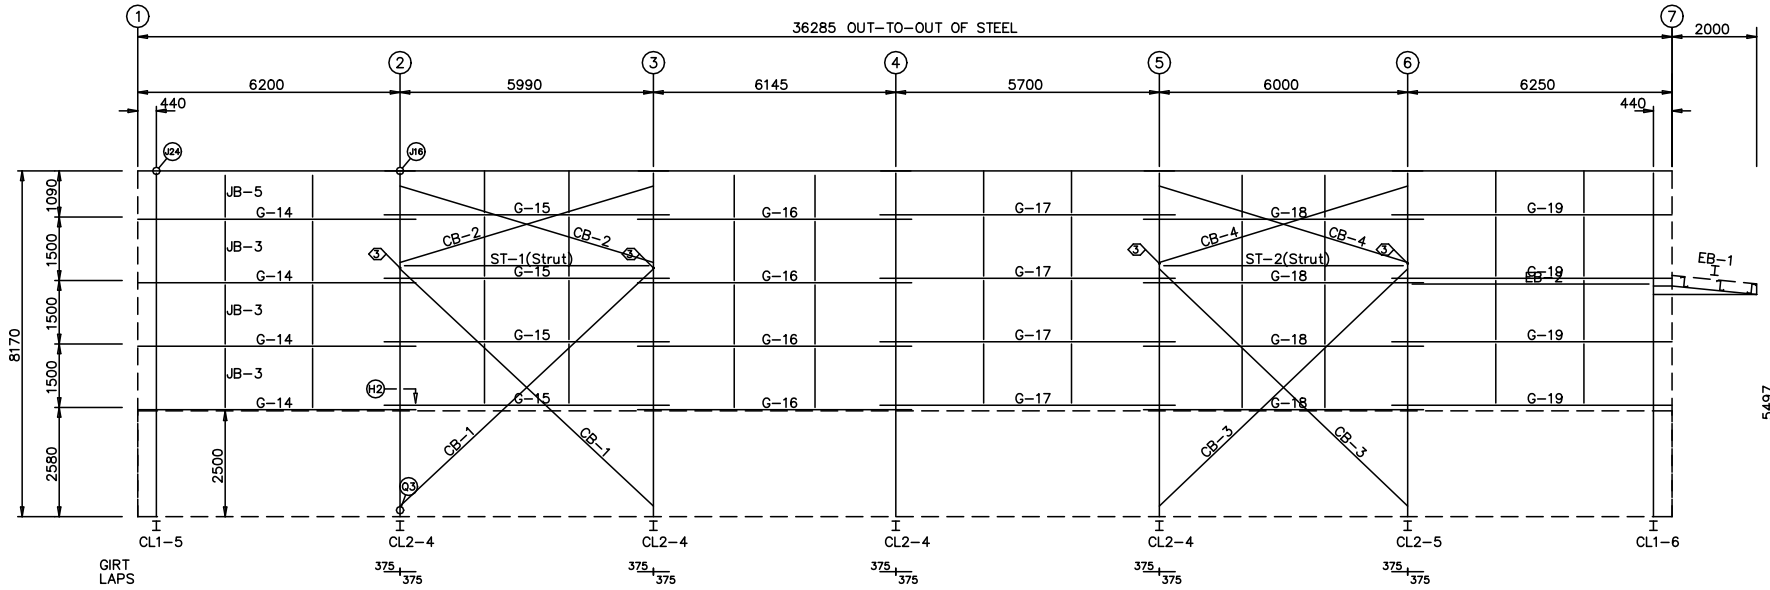

SIDEWALL FRAMING: FRAME LINE A

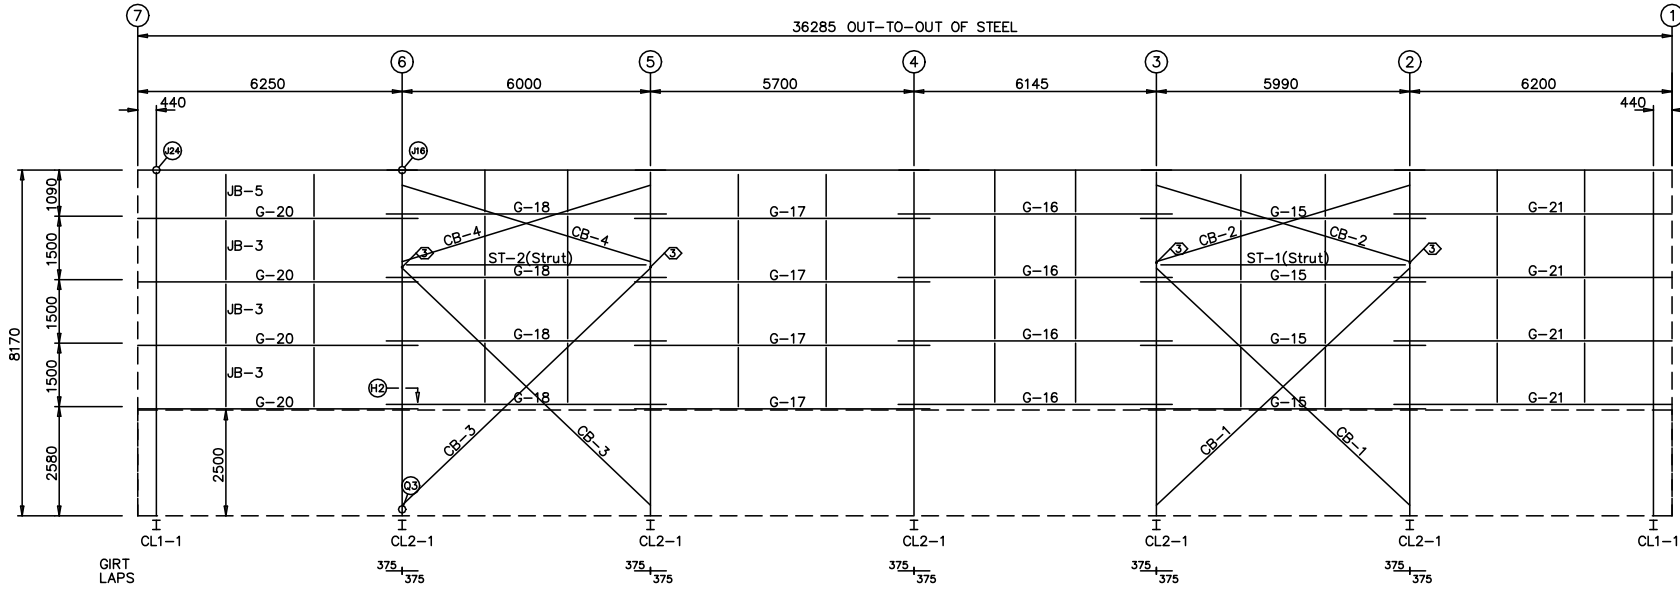

SIDEWALL FRAMING: FRAME LINE C

BOLT TABLE				
FRAME LINE A & C				
LOCATION	QUAN	TYPE	DIA	LENGTH
Strut	2	Gr8.8	16	70
EB-2 (L)	4	Gr8.8	16	
EB-2 (R)	8	Gr8.8	20	90

SPECIAL BOLTS				
Q ID	QUAN	TYPE	DIA	LENGTH
3	2	Gr8.8	16	70
				2

MEMBER TABLE		
FRAME LINE A & C		
MARK	PART	LENGTH
EB-1	BEAM	2473
EB-2	W30x155	5805
G-14	200Z	6570
G-15	200Z	6740
G-16	200Z	6480
G-17	200Z	6980
G-18	200Z	6620
G-19	200Z	6620
G-20	200Z	6620
G-21	200Z	6570
ST-1	T80x32	5945
ST-2	T80x32	5825
CB-1	ROD20	8140
CB-2	ROD20	6210
CB-3	ROD20	8050
CB-4	ROD20	6100
JB-3	SROD12	1600
JB-5	SROD12	990

RECLA INTERNATIONAL PRIVATE LIMITED				
PROJECT	Proposed Warehouse	SIDEWALL FRAMING		
ID	C323-153	DESIGN: AAB	DRAFT: AAB	CHECK: VVJ
PROJECT ADDRESS	PUNE	DATE: 23/JUL/2025		