



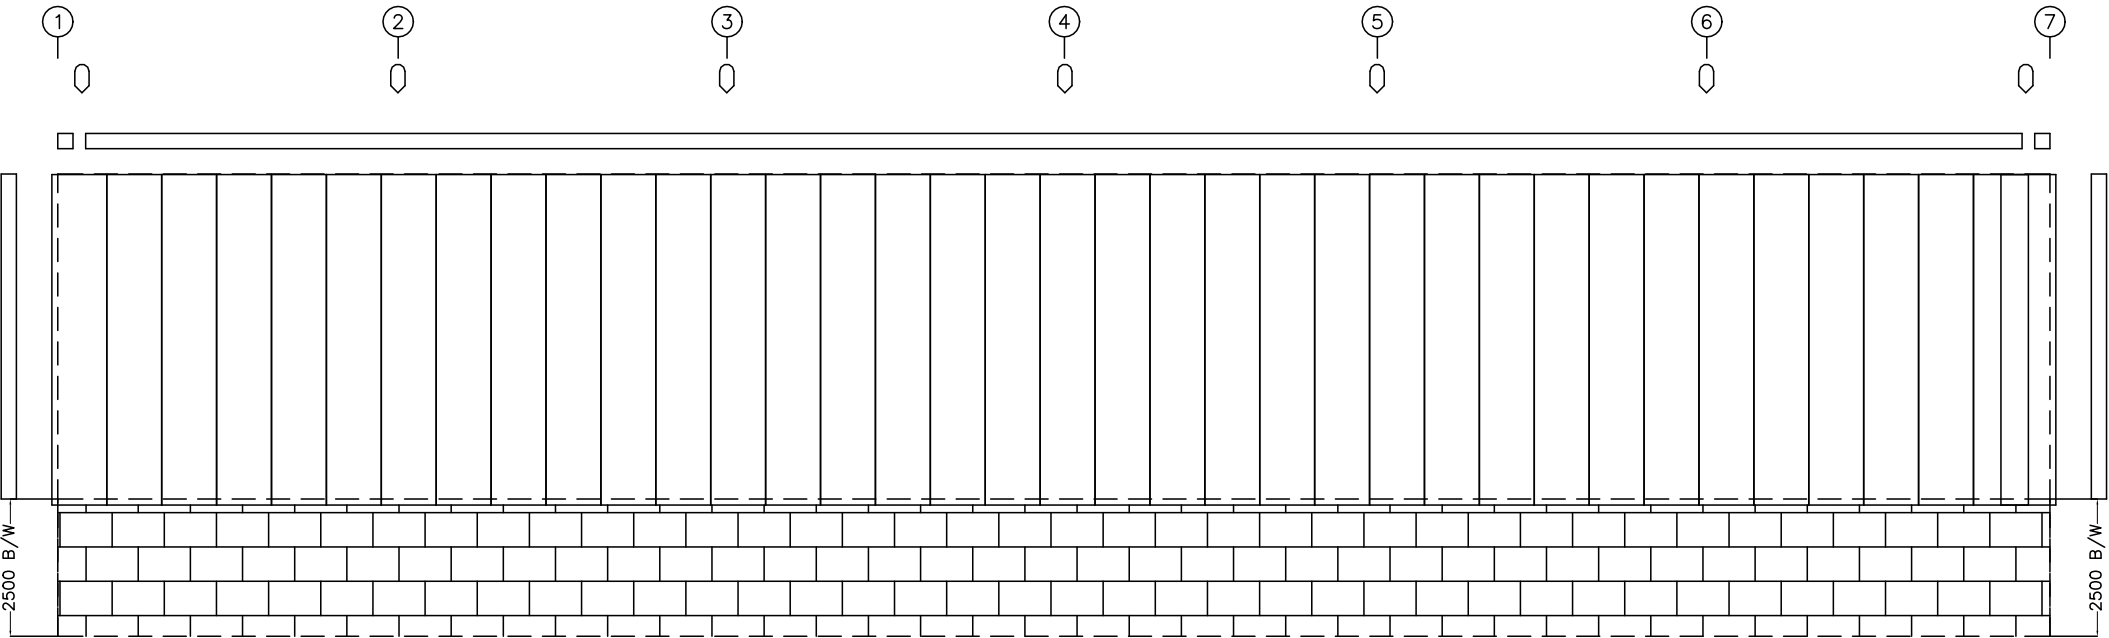

SIDEWALL SHEETING & TRIM: FRAME LINE A

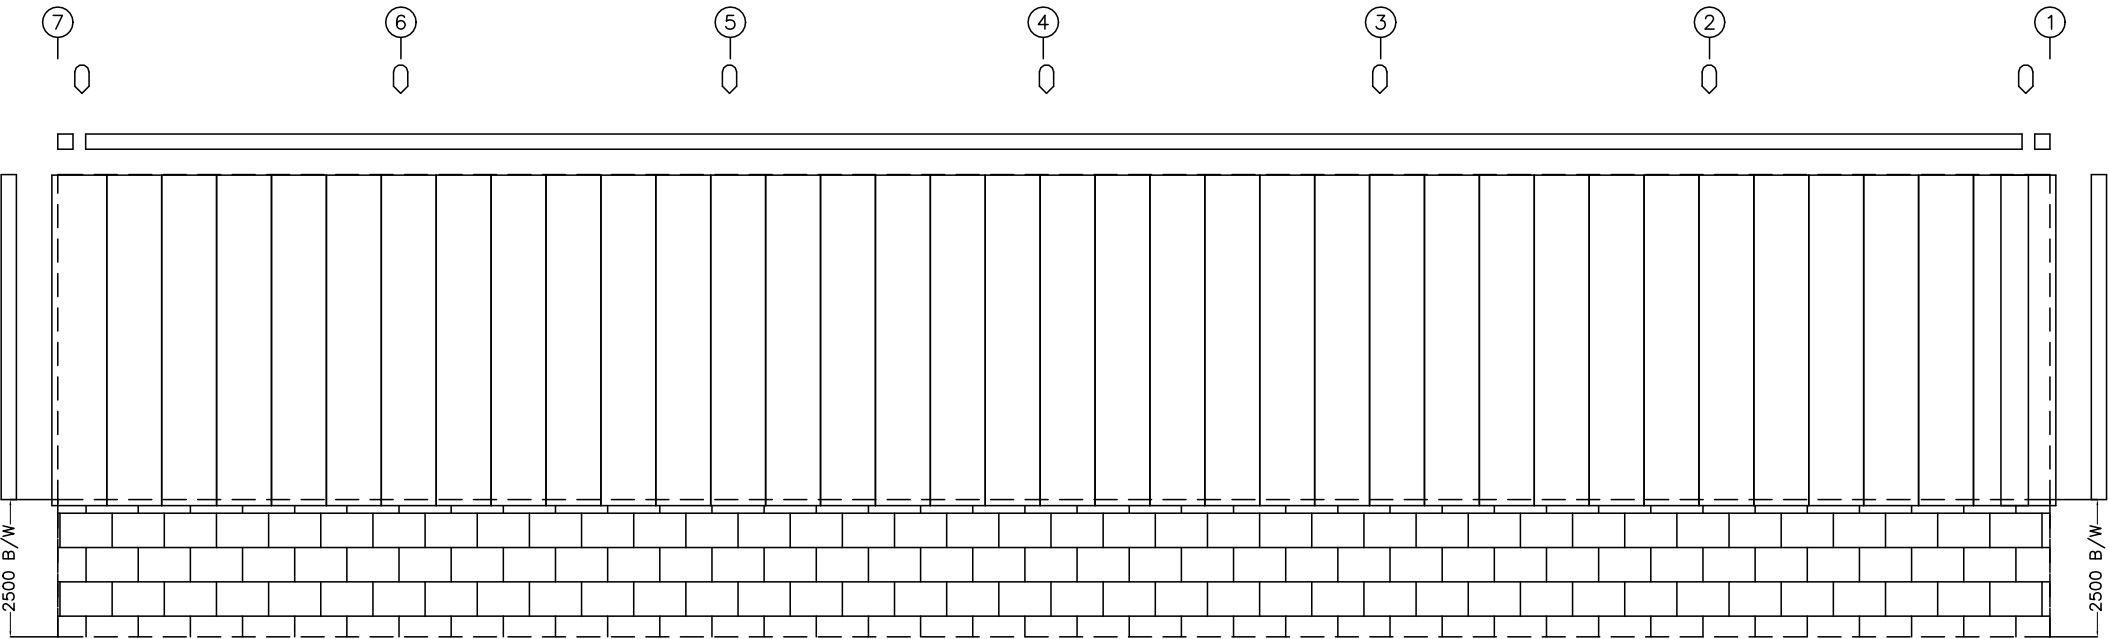

SIDEWALL SHEETING & TRIM: FRAME LINE C

RECLA INTERNATIONAL PRIVATE LIMITED				
PROJECT	Warehouse	SIDEWALL FRAMING		
ID	C323-153	DESIGN: AAB	DRAFT: SSP	CHECK: VVJ
PROJECT	Warehouse	DATE: 7/AUG/2025		
ADDRESS	PUNE	C323-153-A011		