



MEMBER TABLE		
FRAME LINE A & C		
MARK	PART	LENGTH
EB-1	BEAM	2272
EB-2	W30x155	5805
EB-4	BEAM	2272
G-16	200Z	6570
G-17	200Z	6740
G-18	200Z	6895
G-19	200Z	6450
G-20	200Z	6750
G-21	200Z	6620
G-22	200Z	6620
G-23	200Z	6570
G-24	200Z	6180
G-25	200Z	6190
CB-1	ROD	8220
CB-2	ROD	6270
CB-3	ROD	8230
JB-3	SROD	1600
JB-6	SROD	1290
WA	Z200	200

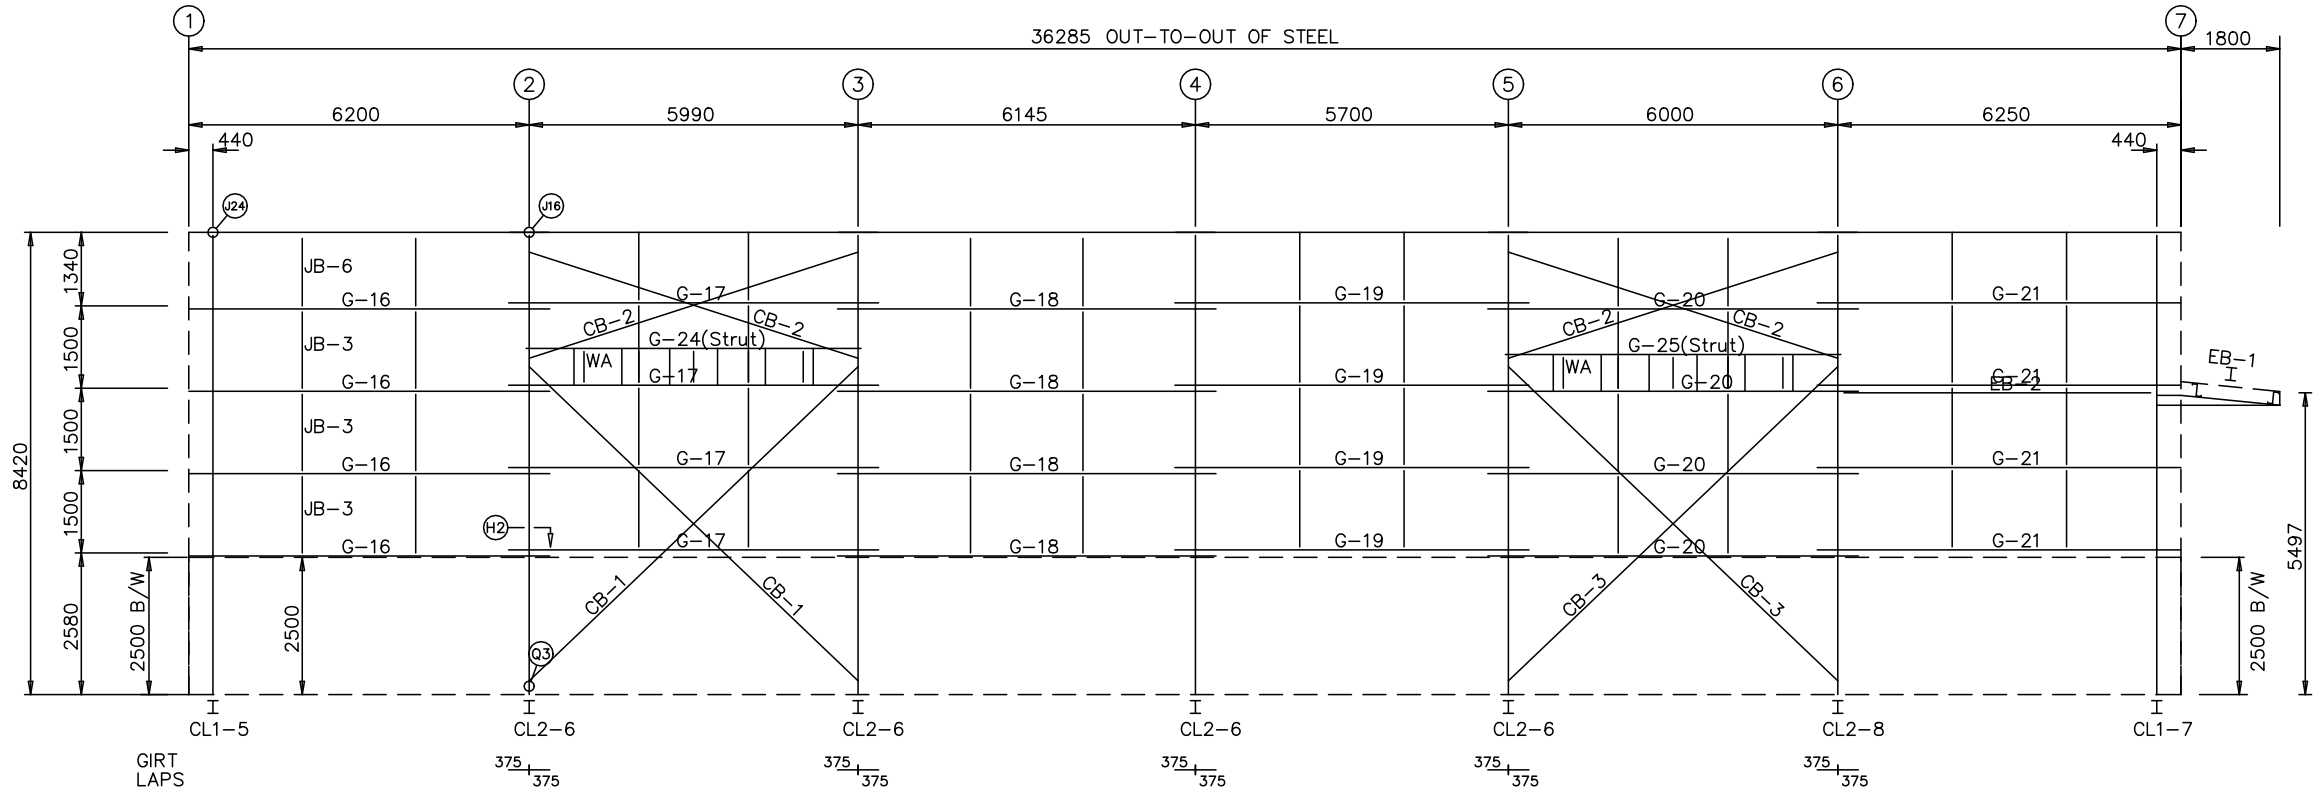

SIDEWALL FRAMING: FRAME LINE A

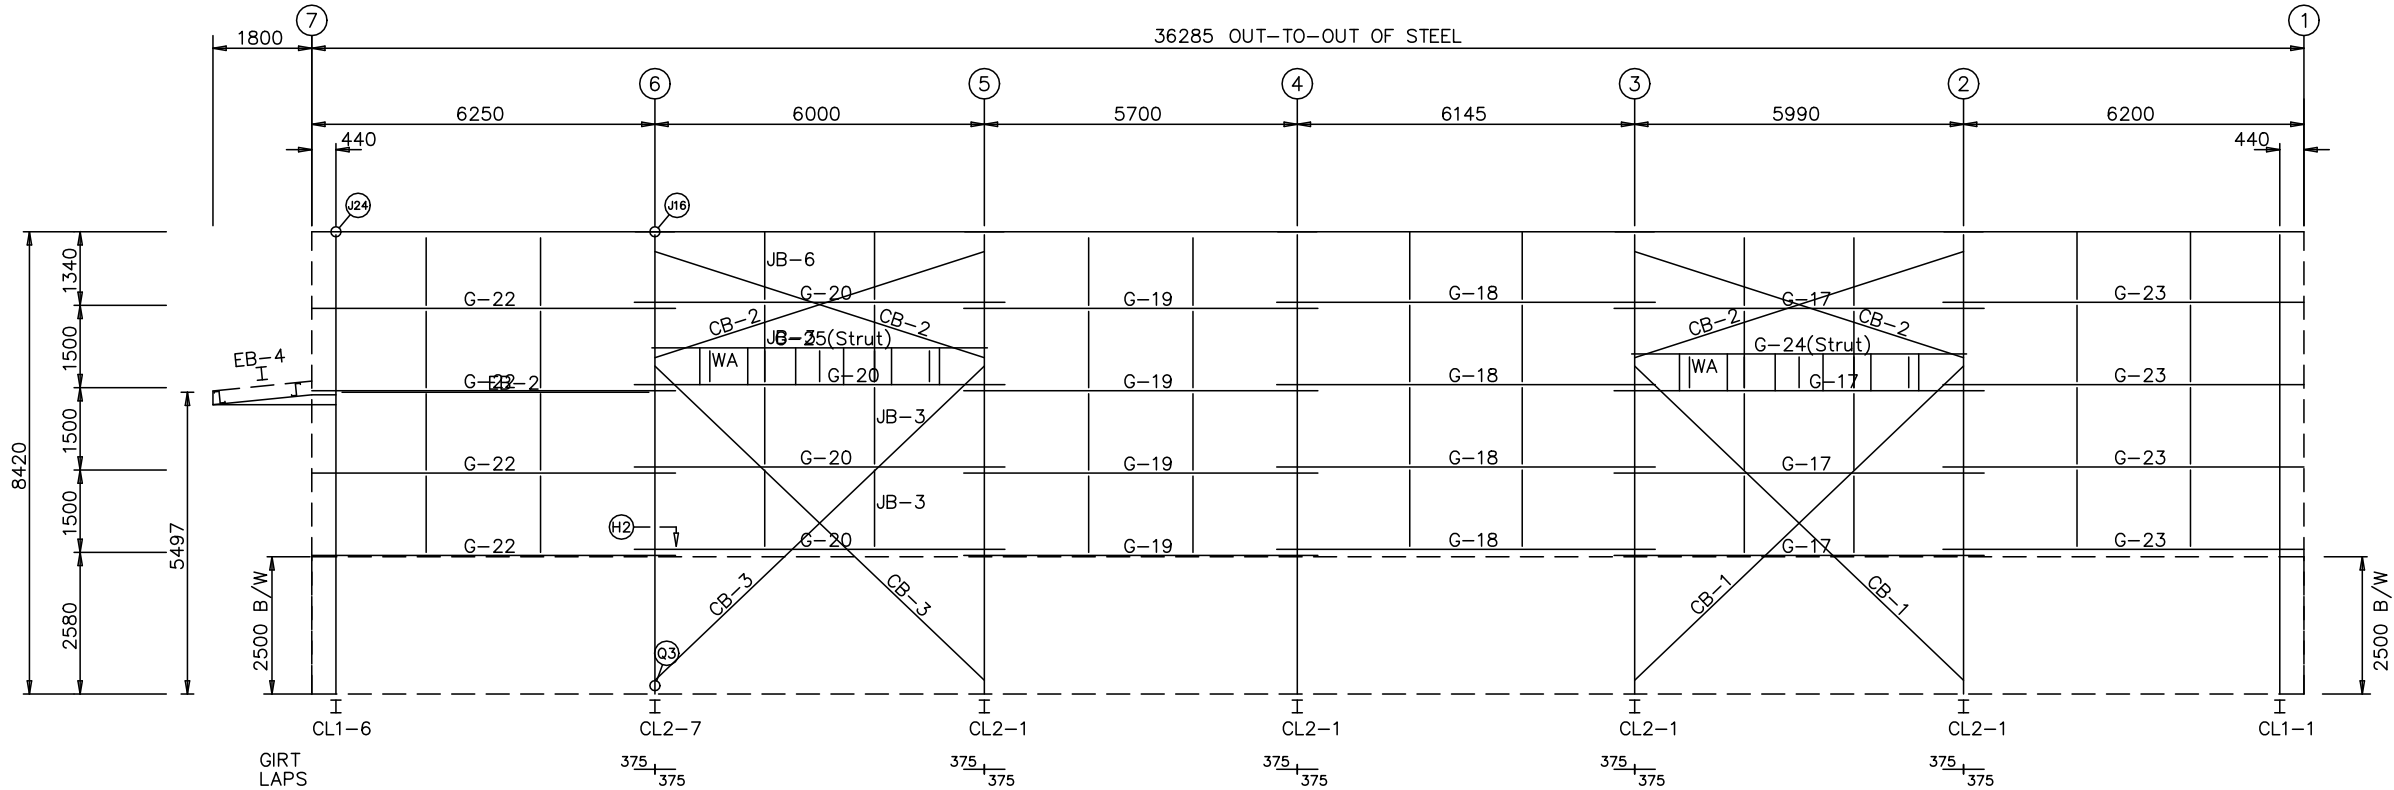

SIDEWALL FRAMING: FRAME LINE C

RECLA INTERNATIONAL PRIVATE LIMITED				
PROJECT	Warehouse	SIDEWALL FRAMING		
ID	C323-153	DESIGN: AAB	DRAFT: SSP	CHECK: VVJ
PROJECT	Warehouse	DATE: 7/AUG/2025		
ADDRESS	PUNE	C323-153-A012		