


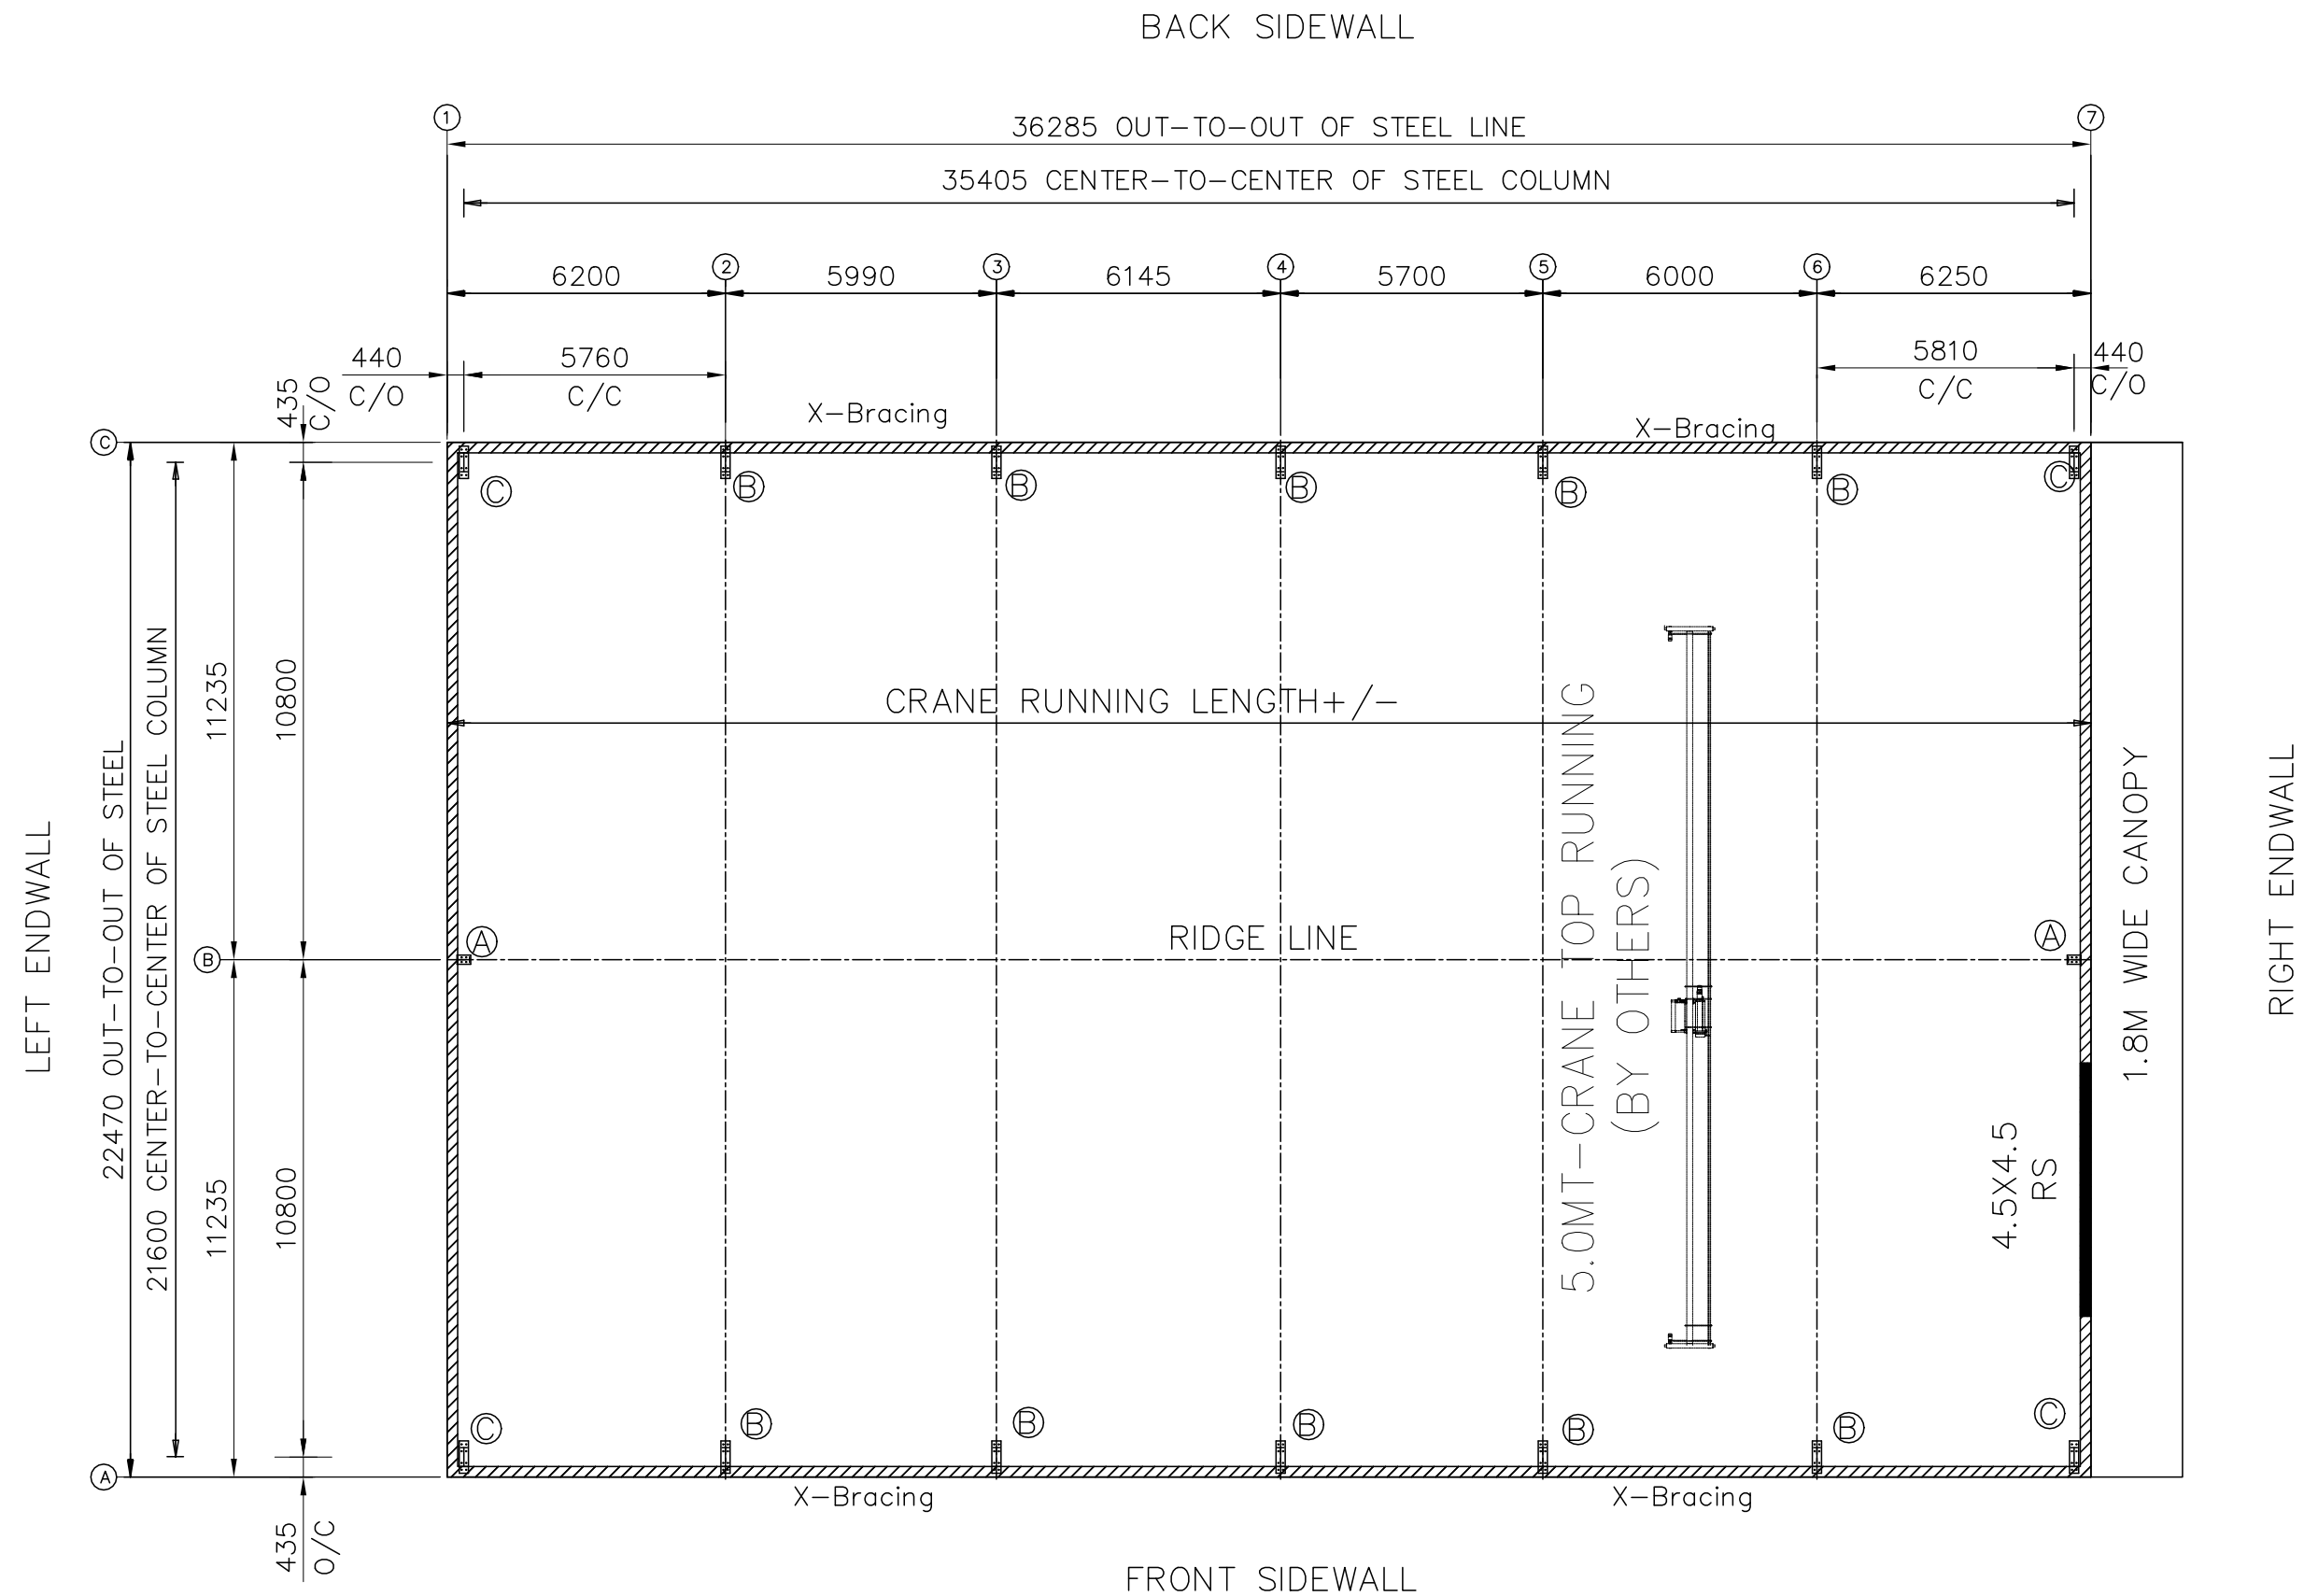

FRONT SIDEWALL

ANCHOR BOLT PLAN

NOTE: All Base Plates @ 0 (U.N.)



2.5M B/W AND ABOVE SHEETING

NOTE: CRANE IS IN FUTURE



RECLA

|   |                    |                                       |
|---|--------------------|---------------------------------------|
| NOTE-THE DRAWING ARE INTENDED SOLELY FOR APPROVAL PURPOSES. CERTAIN PARTS OR DIMENSIONS MAY NOT BE TO SCALE AND THEREFORE MUST NOT BE USED FOR CONSTRUCTION OR ANY OTHER PURPOSE |                    |                                       |
| RECLA INTERNATIONALS PRIVATE LIMITED   |                    |                                       |
| PROJECT   | Proposed Warehouse | ANCHOR BOLT PLAN                      |
| ID   | C323-153           | DESIGN: AAB   DRAFT: AAB   CHECK: VVJ |
| PROJECT ADDRESS   | PUNE               | DATE: 09/JUN/2025                     |
|   |                    | C323-153_A01                          |