




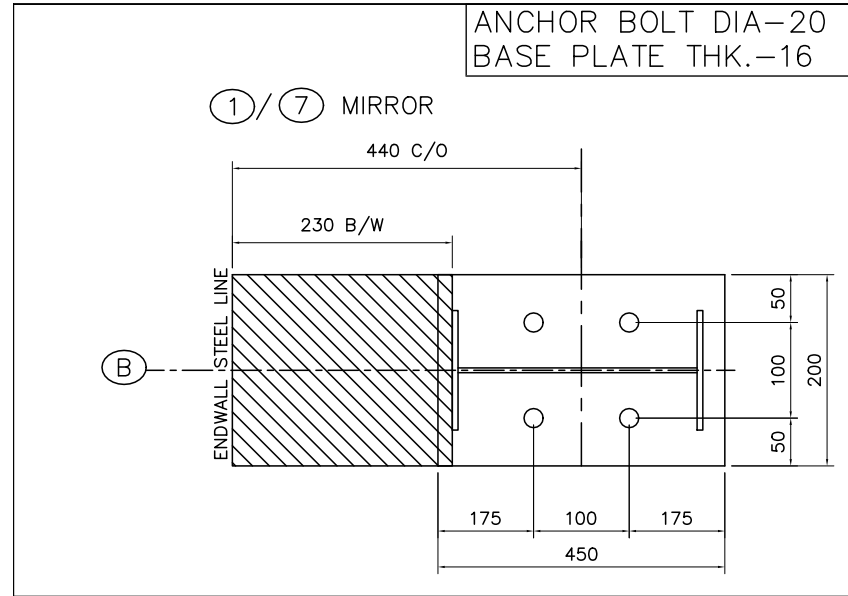


DETAIL-A

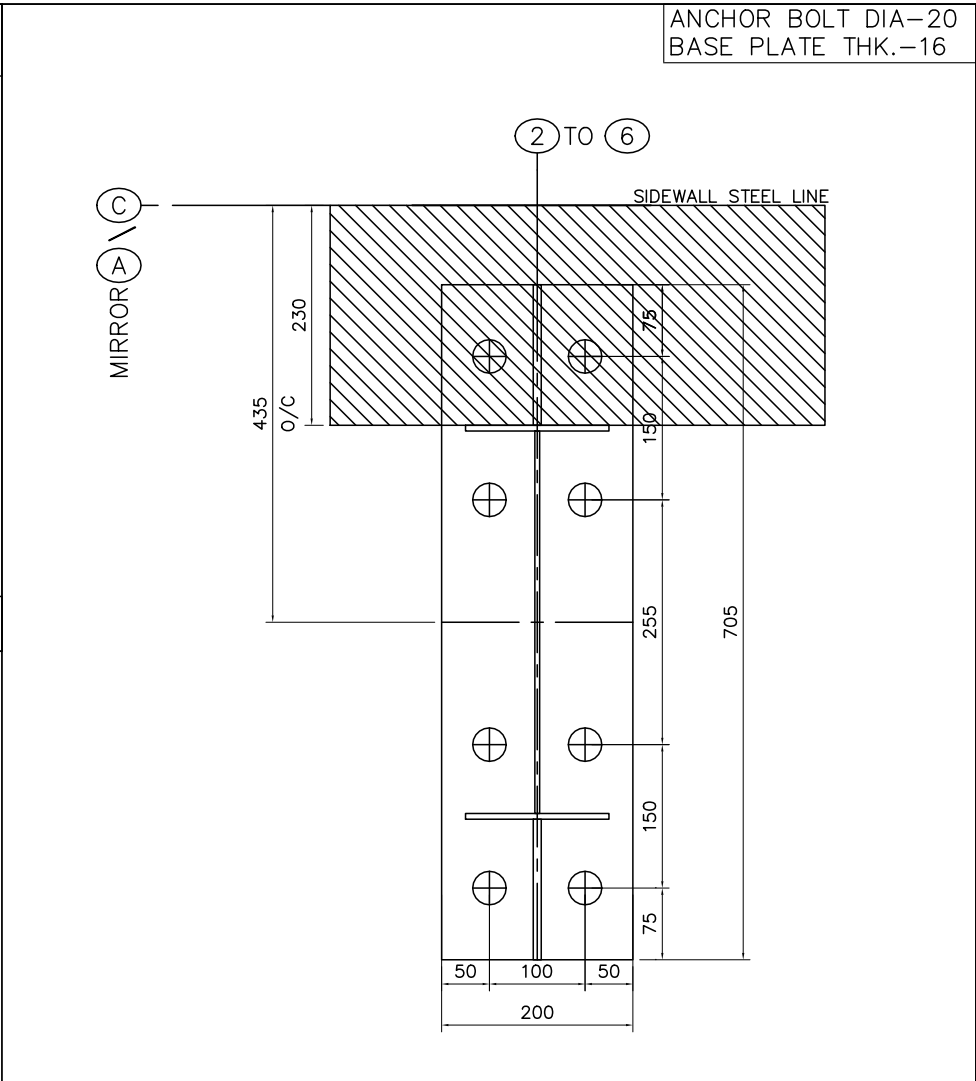



DETAIL-C

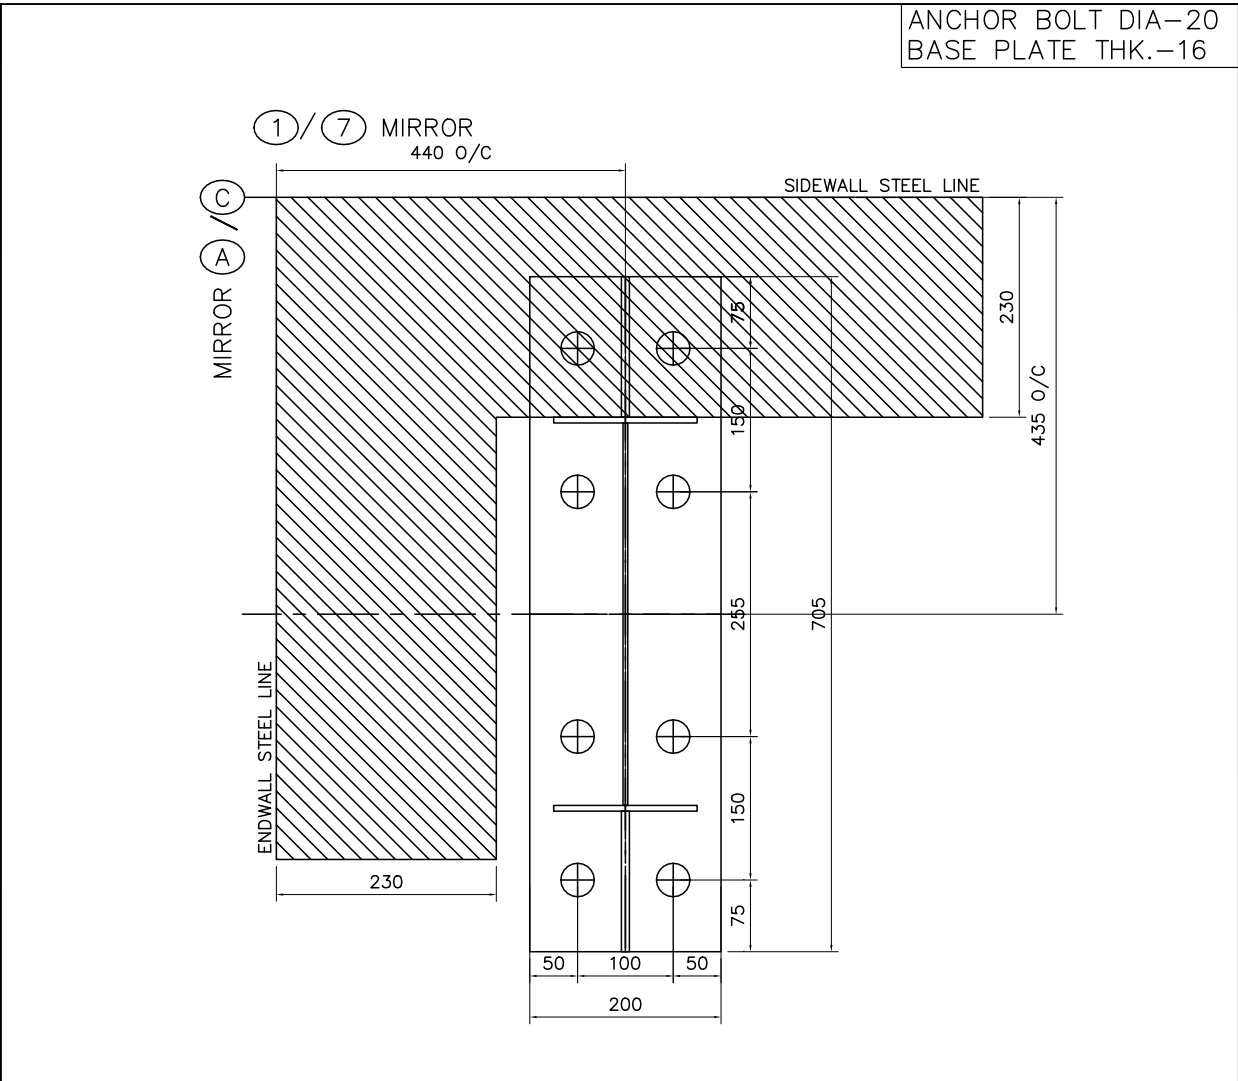

DETAIL-B

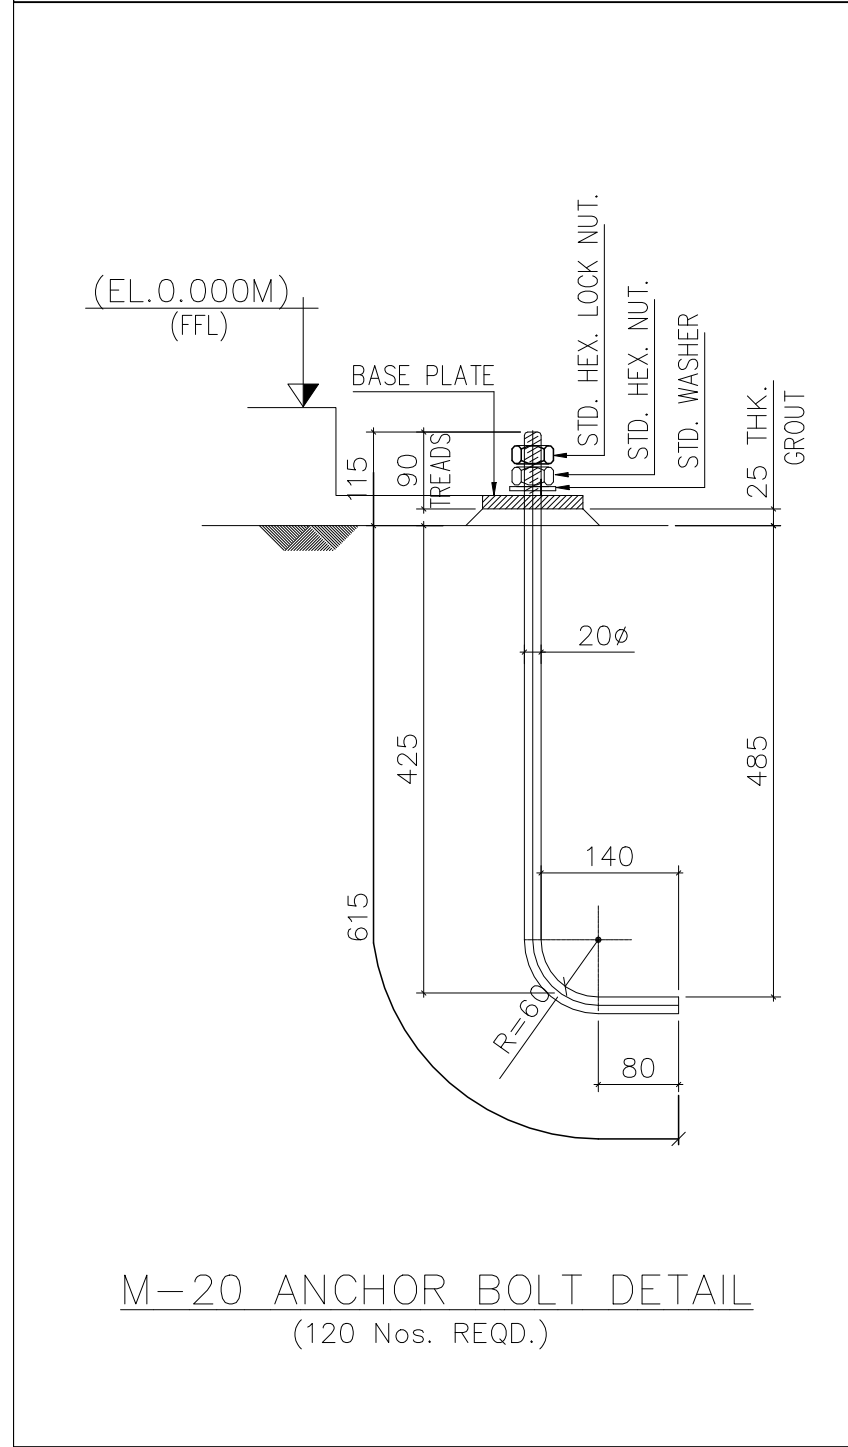

M-20 ANCHOR BOLT DETAIL
(120 Nos. REQD.)

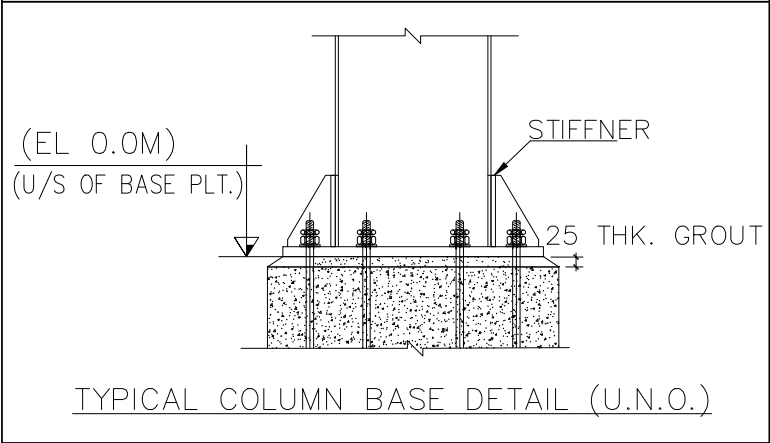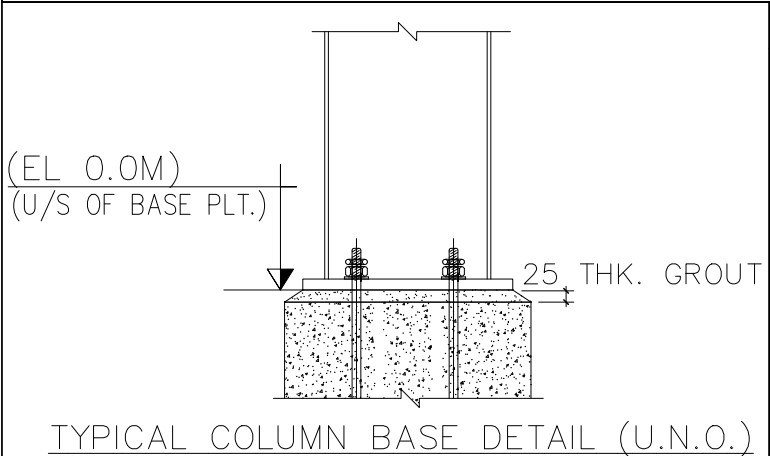

- NOTES
1. THIS DRAWING IS TO BE READ IN CONJUNCTION WITH ALL OTHER RELEVANT ARCHITECTURAL AND STRUCTURAL DRAWINGS.
 2. ALL DIMENSIONS ARE IN MILLIMETERS AND LEVELS ARE IN METERS UNLESS NOTED OTHERWISE.
 3. DO NOT SCALE THE DRAWING.
 4. ALL HOT ROLLED MEMBERS SHALL CONFORM TO BSEN 10025-S275 OR EQUIVALENT.
 5. ALL THE BUILT UP MEMBERS SHALL CONFORM TO ASTM A572 OR BSEN 10025-S355
 6. ALL WELDS ARE AWS STANDARD UNLESS OTHERWISE NOTED.
 7. BOLTS FOR MAIN STRUCTURAL CONNECTIONS ARE ASTM A325
 8. BOLTS FOR BRACINGS, PURLINS, GIRTS ETC.. ARE GRADE 8.8
 9. PAINTING SYSTEM AND ALL OTHER TERMS AS PER CONTRACTS.

NOTE-THE DRAWING ARE INTENDED SOLELY FOR APPROVAL PURPOSES. CERTAIN PARTS OR DIMENSIONS MAY NOT BE TO SCALE AND THEREFORE MUST NOT BE USED FOR CONSTRUCTION OR ANY OTHER PURPOSE

RECLA INTERNATIONALS PRIVATE LIMITED		
PROJECT	SHED	ANCHOR BOLT DETAILS
ID	C323-153	DESIGN: AAB DRAFT: AAB CHECK: VVJ
PROJECT	PUNE	DATE: 07/AUG/2025
ADDRESS		C323-153_A02



RECLA