EXTENSION/CANOPY BOLTS ROOF PLAN				
MARK	QUAN	TYPE	DIA	LENGTH
EB-1	8	Gr8.8	20	90
EB-3	8	Gr8.8	20	90
EB-4	8	Gr8.8	20	90

MEMBER TABLE ROOF PLAN		
MARK	PART	LENGTH
EB-1	BEAM	2272
EB-3	BEAM	1830
EB-4	BEAM	2272
P-1	150Z	6570
P-2	150Z	6740
P-3	150Z	6895
P-4	150Z	6450
P-5	150Z	6750
P-6	150Z	6620
P-7	150Z	6570
P-8	150Z	6620
P-9	250Z	12235
P-10	250Z	12235
E-1	150Z	6570
E-2	150Z	6740
E-3	150Z	6895
E-4	150Z	6450
E-5	150Z	6750
E-6	150Z	6620
E-7	150Z	6570
E-8	150Z	6620
E-9	250Z	12240
E-10	250Z	12240
CB-4	ROD	7770
CB-5	ROD	8080
CB-6	ROD	7780
CB-7	ROD	8090
SP-1	SROD	697
SI-1	SROD	1474
SE-1	SROD	1394
SI-	SROD	1519

ANGLE TABLE ROOF PLAN		
◇ID	MARK	LENGTH
	GA	3000

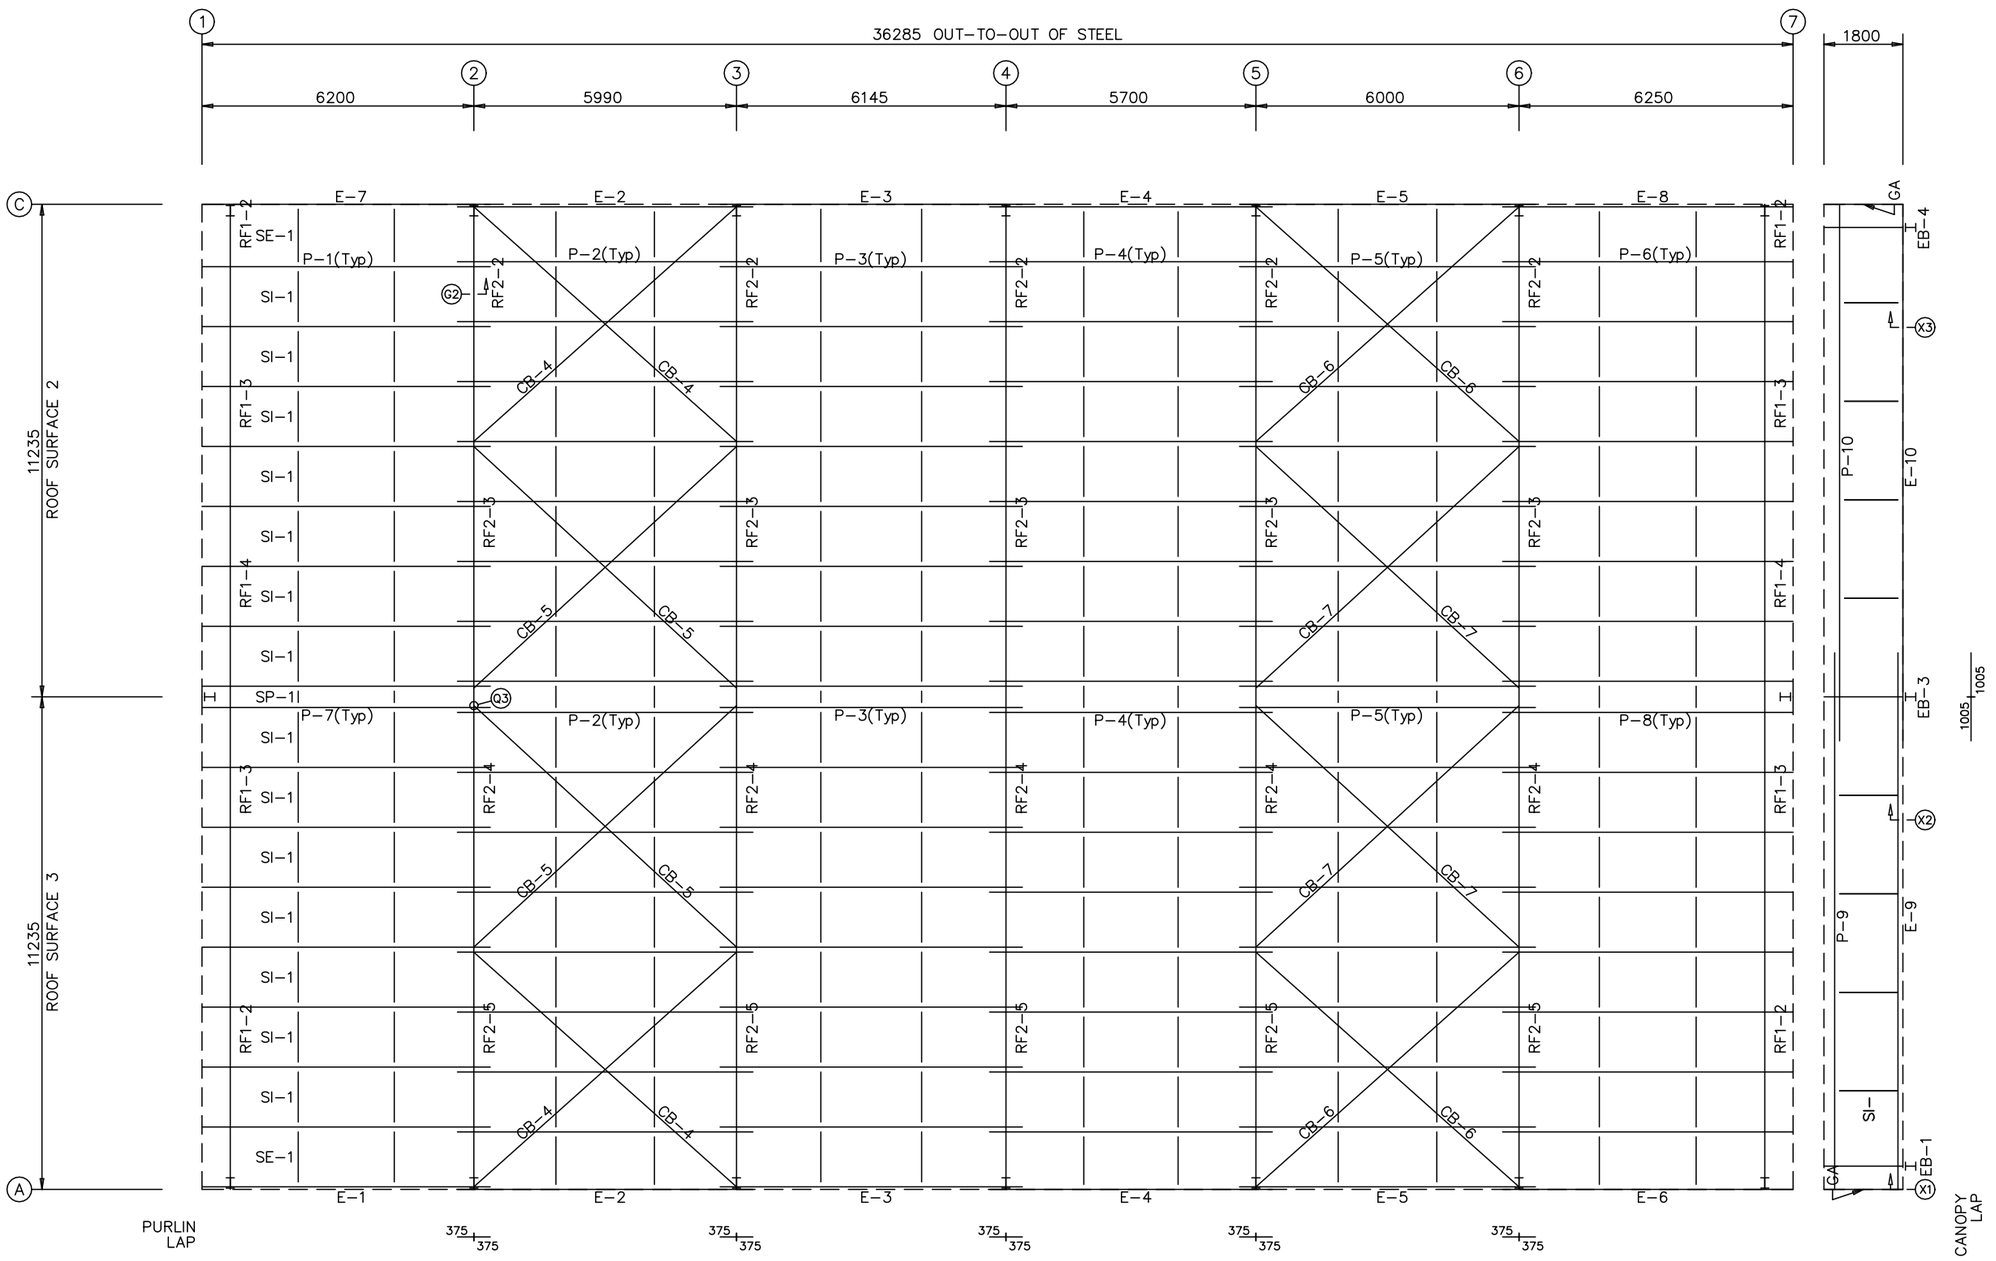

COLUMNS & RAFTERS MARKING PLAN

RECLA INTERNATIONAL PRIVATE LIMITED				
PROJECT	Warehouse	ROOF FRAMING		
ID	C323-153	DESIGN: AAB	DRAFT: SSP	CHECK: VVJ
PROJECT ADDRESS	PUNE	DATE: 7/AUG/2025		
		C323-153-A06		