



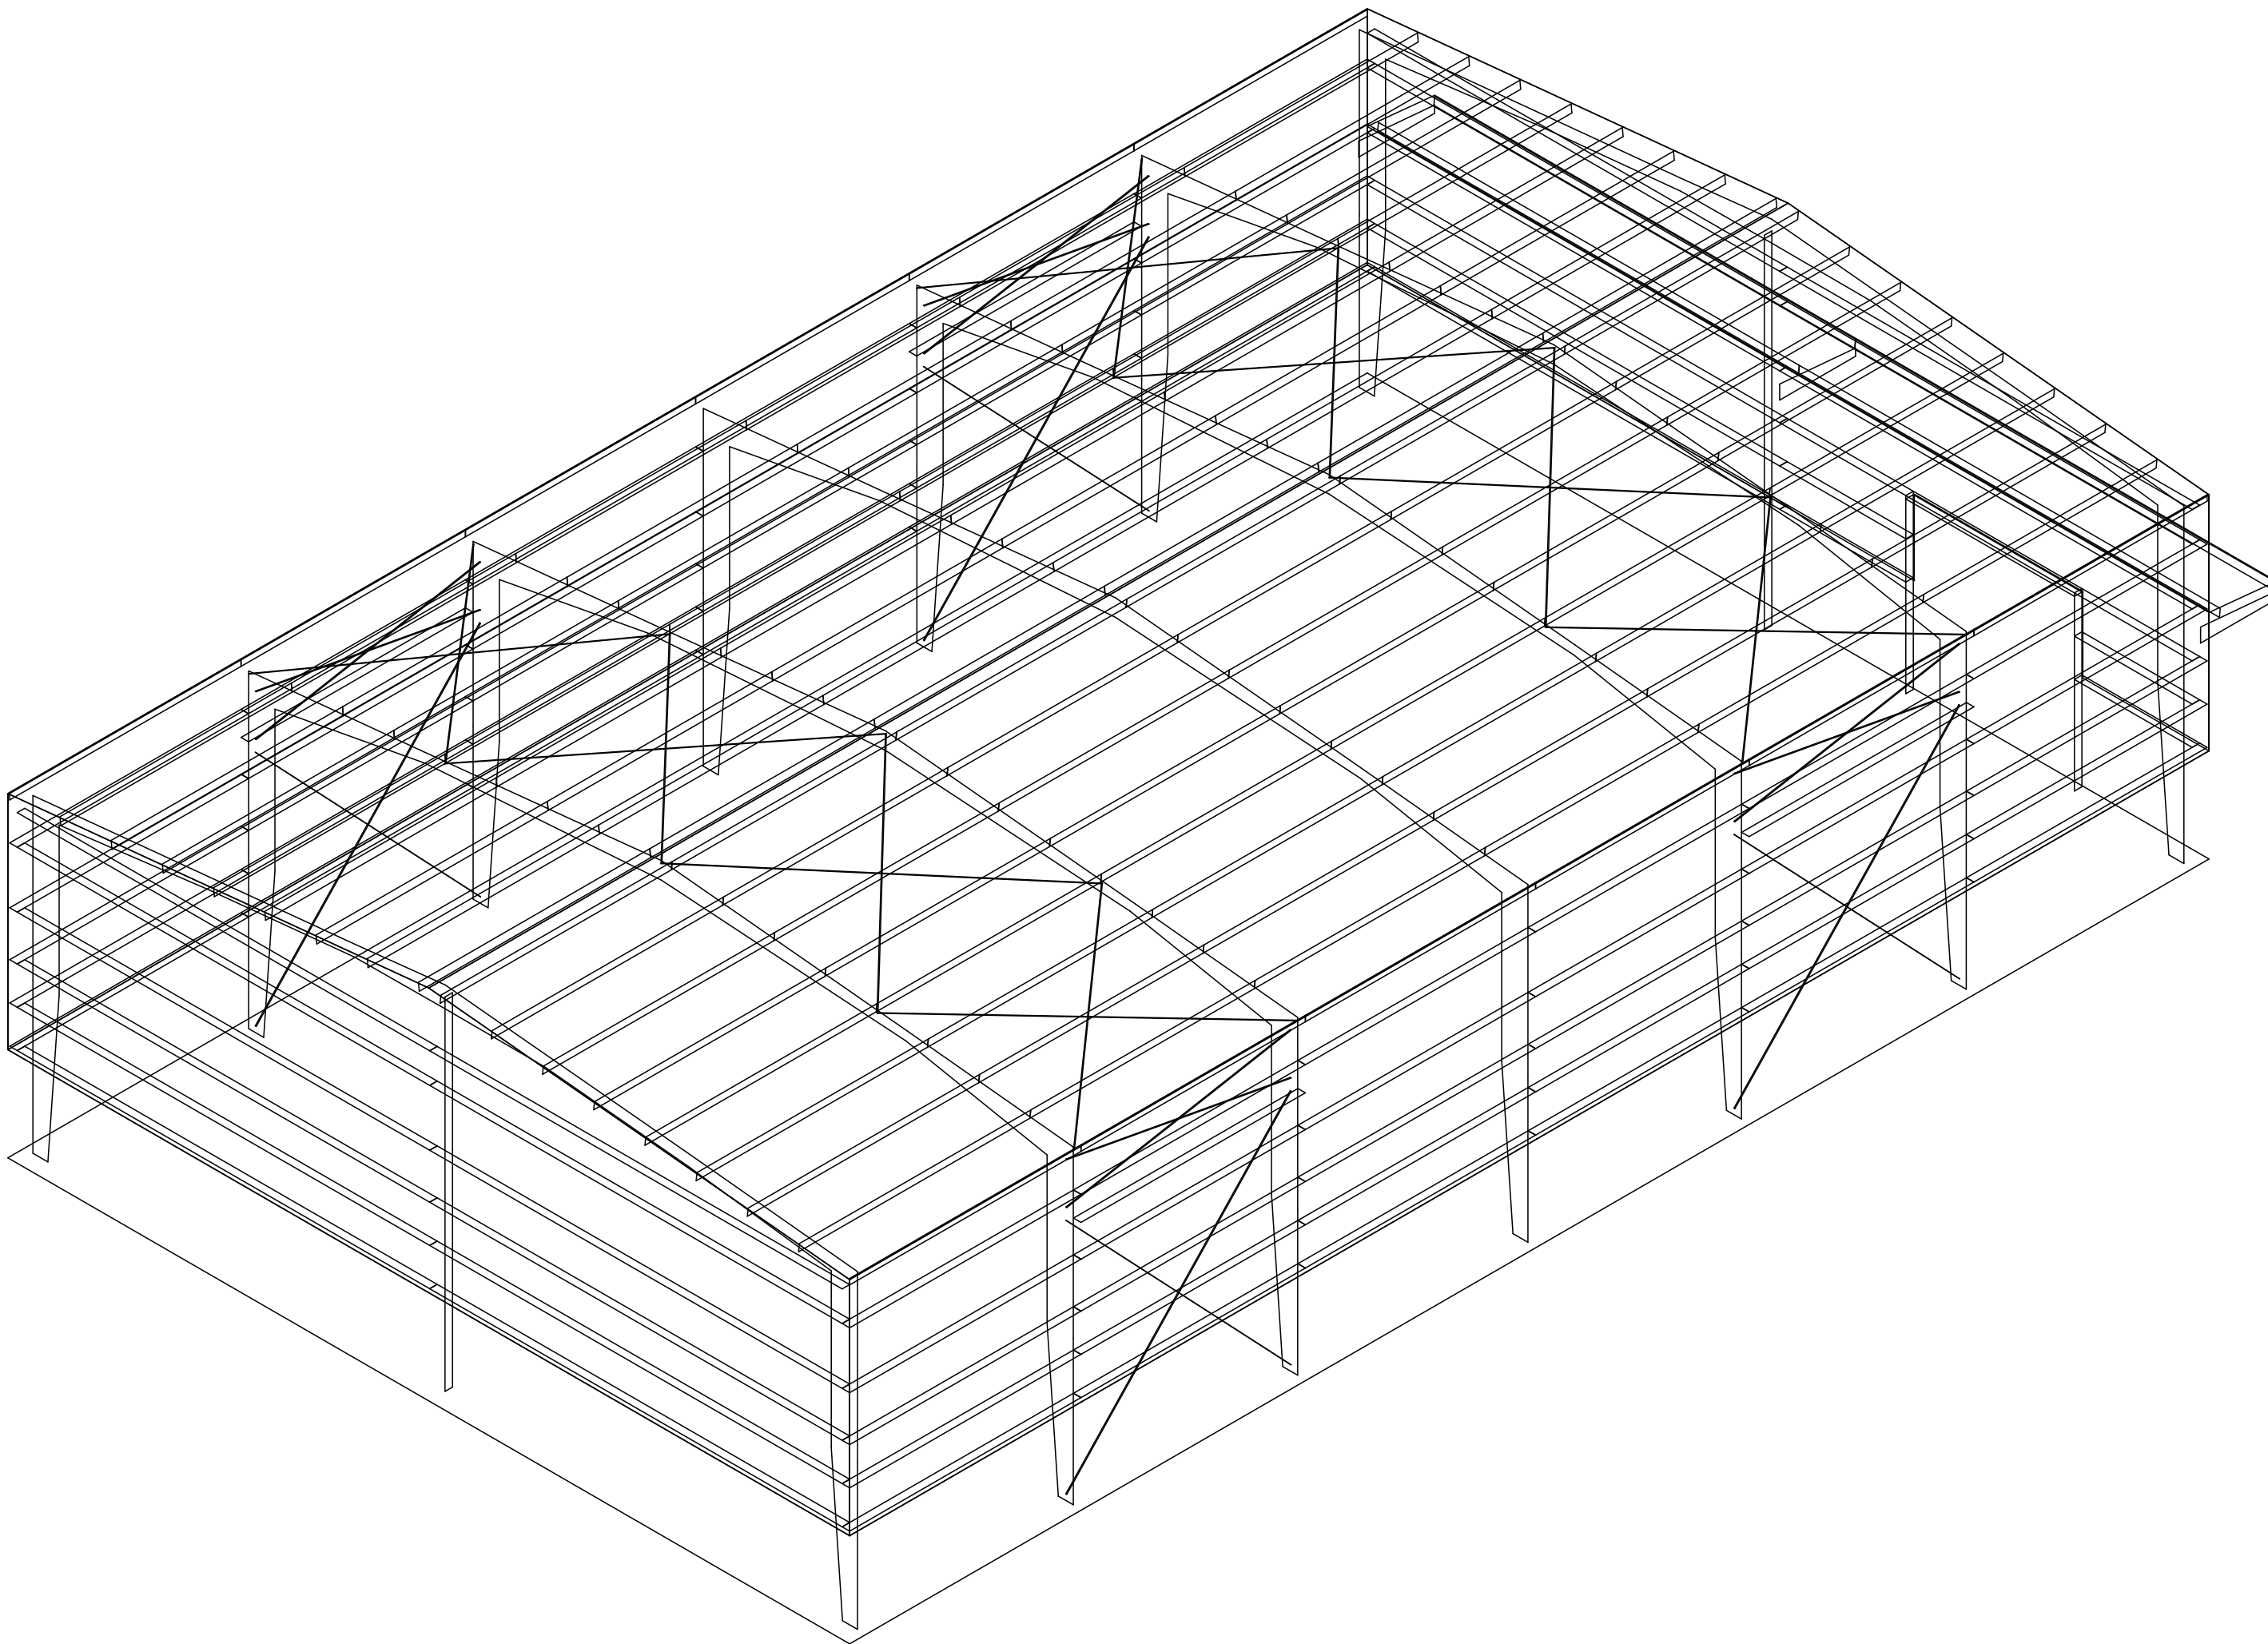

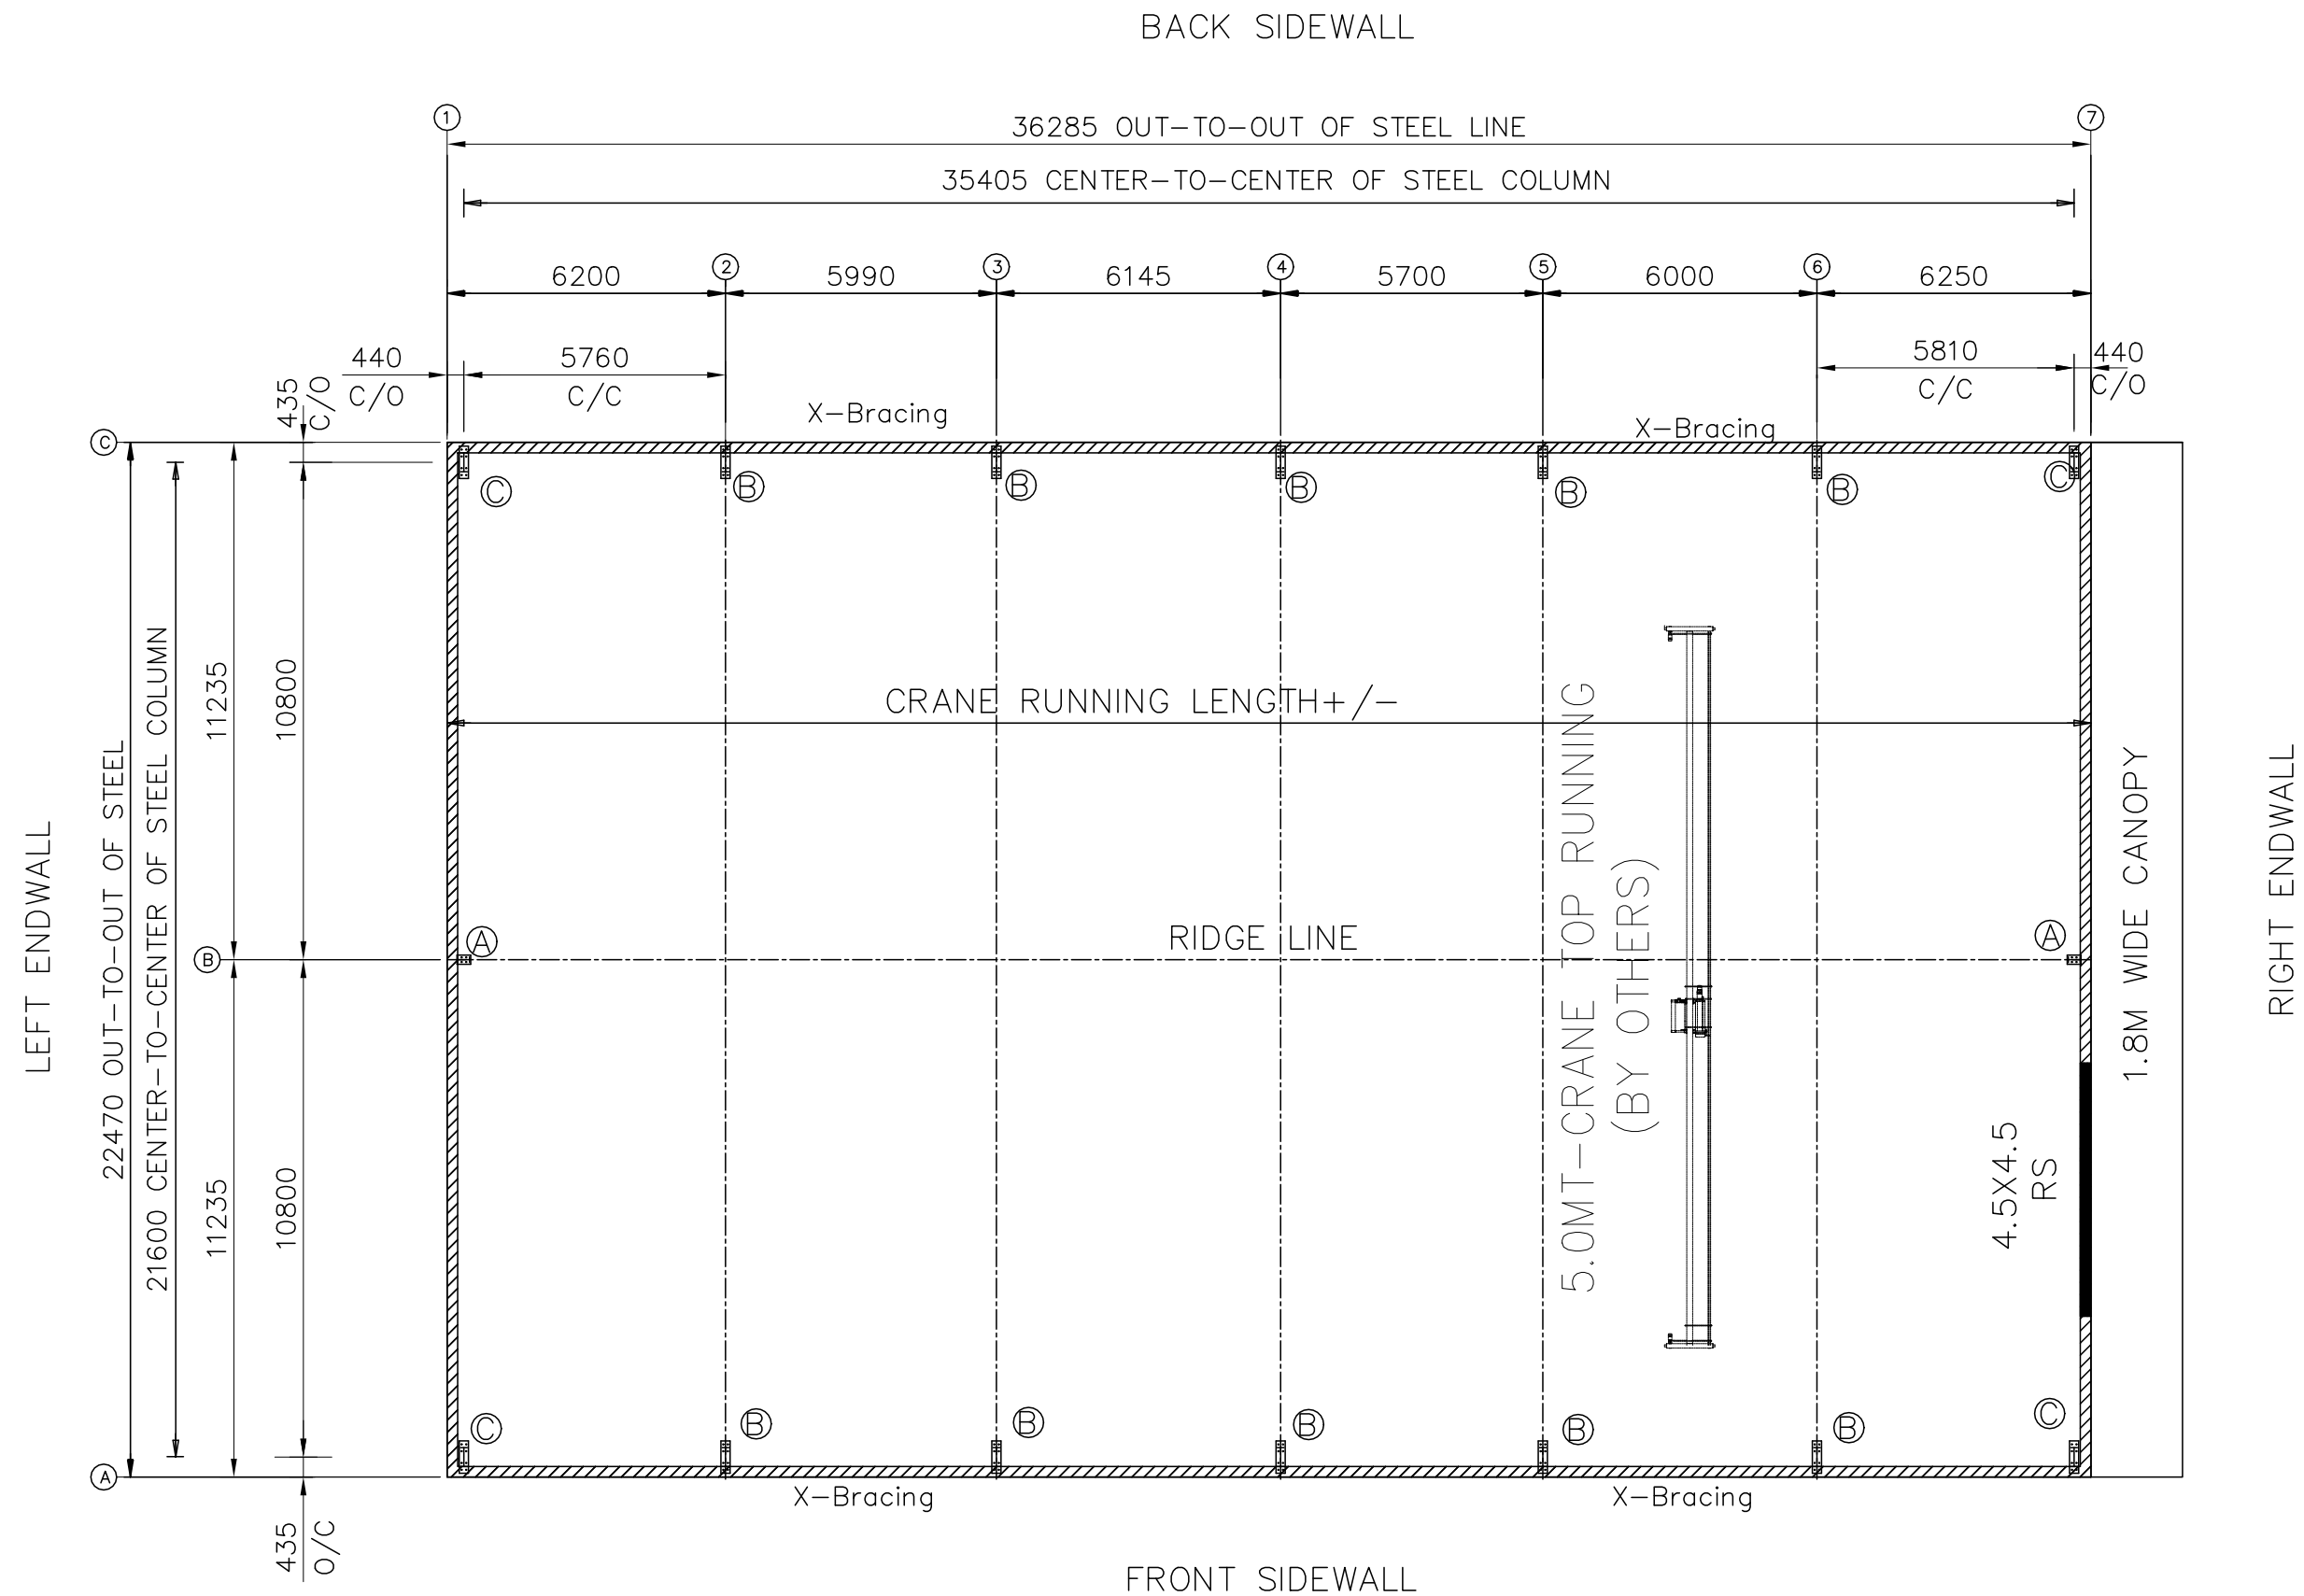

ANCHOR BOLT PLAN

NOTE: All Base Plates @ 0 (U.N.)



2.5M B/W AND ABOVE SHEETING


NOTE: CRANE IS IN FUTURE




RECLA

NOTE-THE DRAWING ARE INTENDED SOLELY FOR APPROVAL PURPOSES. CERTAIN PARTS OR DIMENSIONS MAY NOT BE TO SCALE AND THEREFORE MUST NOT BE USED FOR CONSTRUCTION OR ANY OTHER PURPOSE


| RECLA INTERNATIONALS PRIVATE LIMITED |                    |                   |            |            |
|--------------------------------------|--------------------|-------------------|------------|------------|
| PROJECT                              | Proposed Warehouse | ANCHOR BOLT PLAN  |            |            |
| ID                                   | C323-153           | DESIGN: AAB       | DRAFT: AAB | CHECK: VVJ |
| PROJECT ADDRESS                      | PUNE               | DATE: 09/JUN/2025 |            |            |
|                                      |                    | C323-153_A01      |            |            |

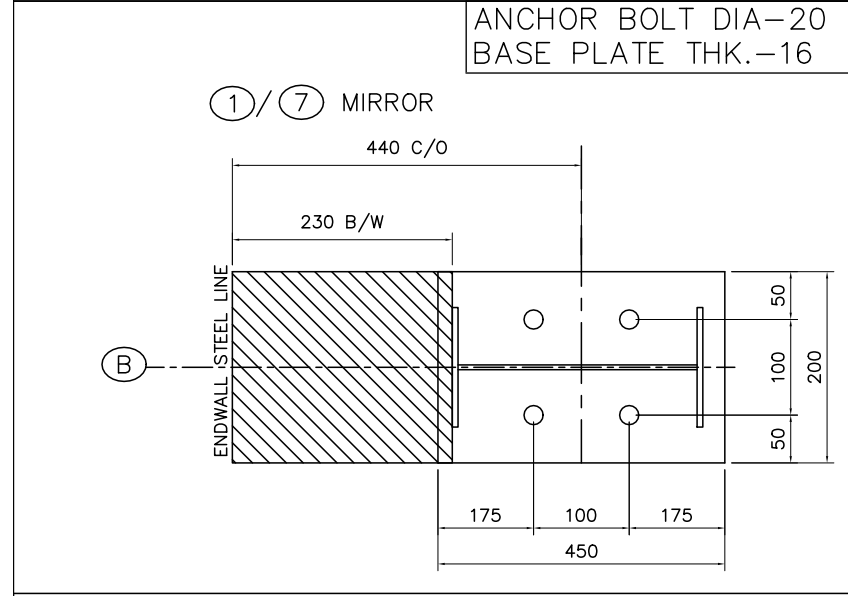


DETAIL-A

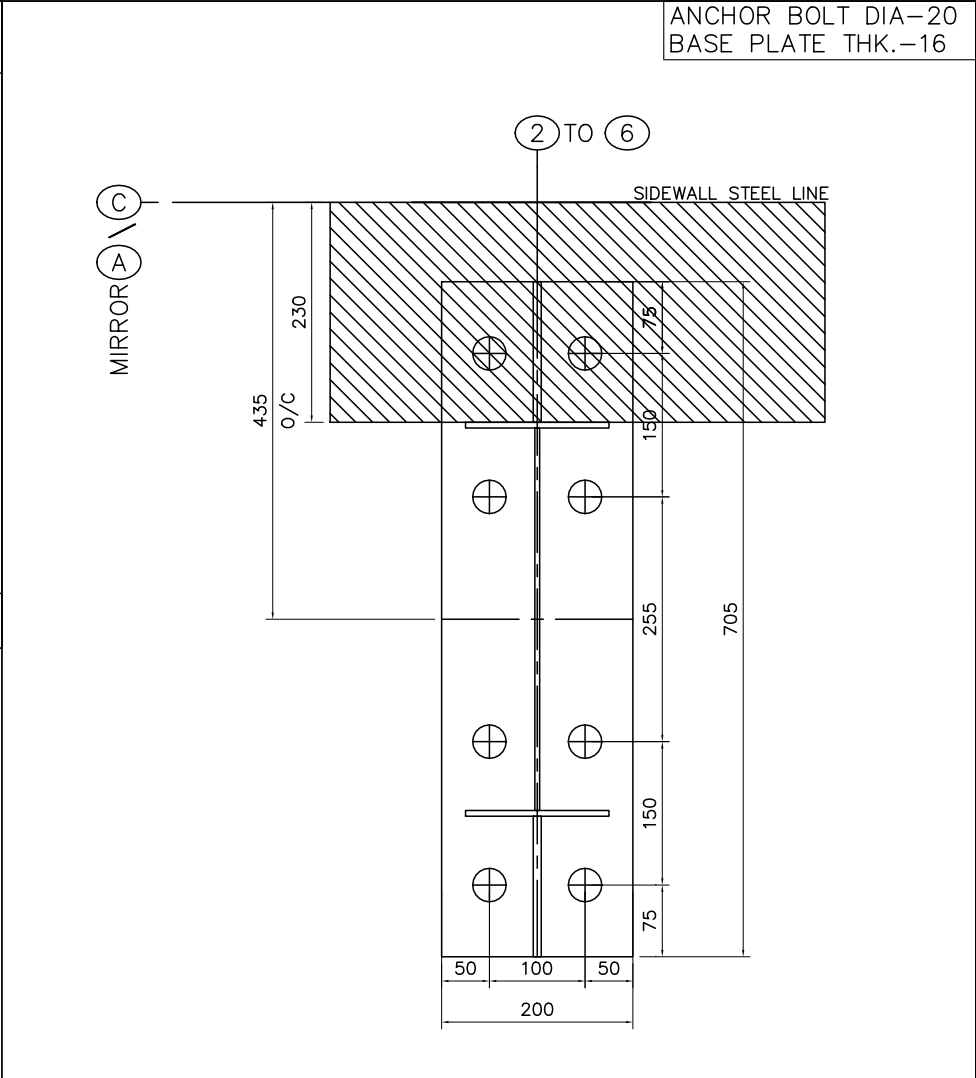


DETAIL-C

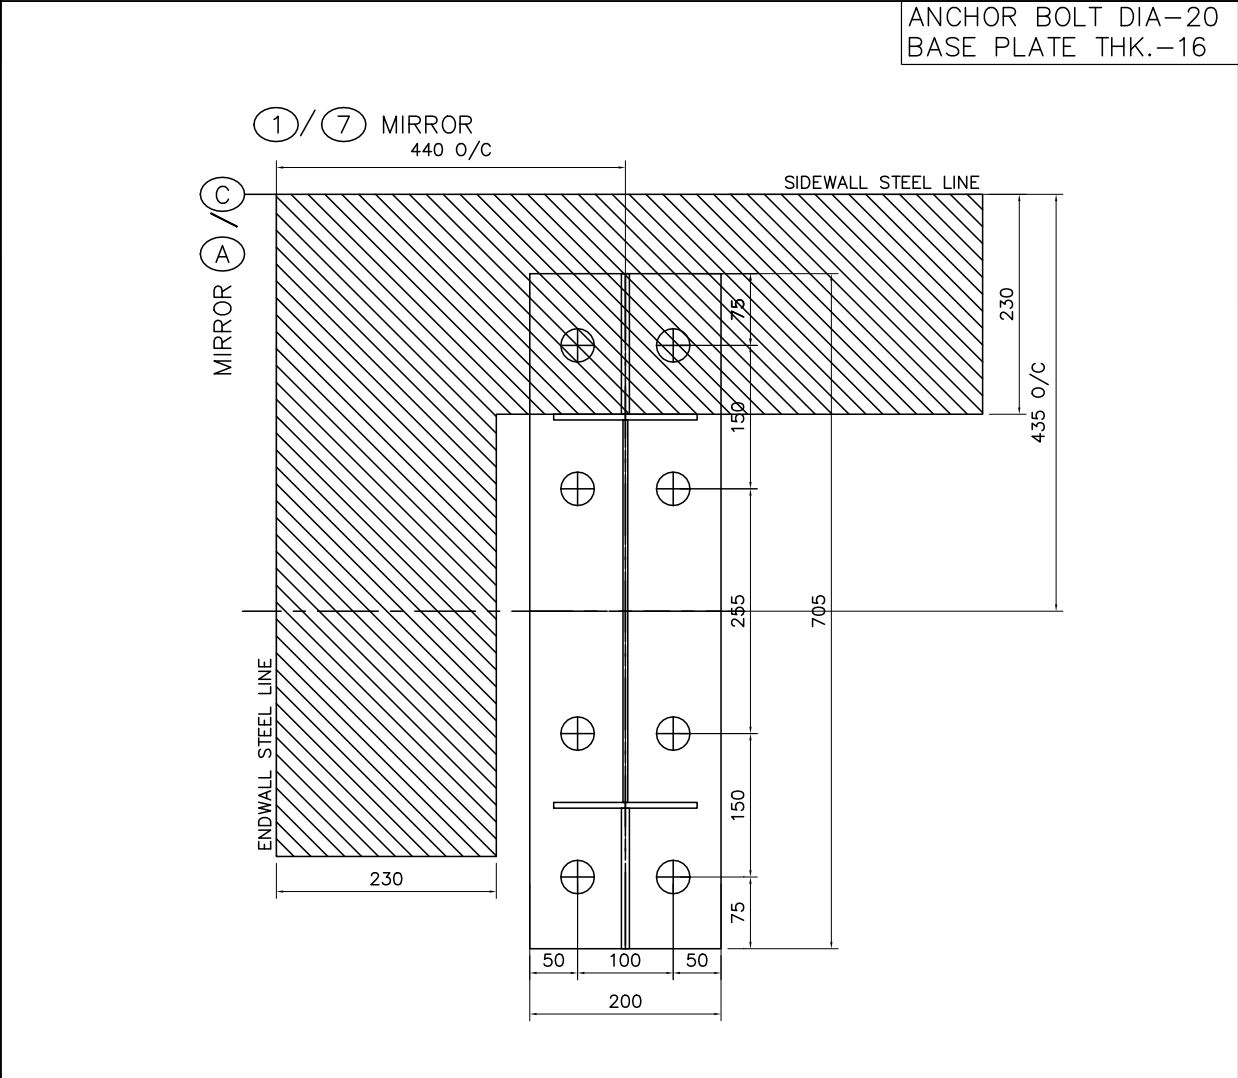


DETAIL-B

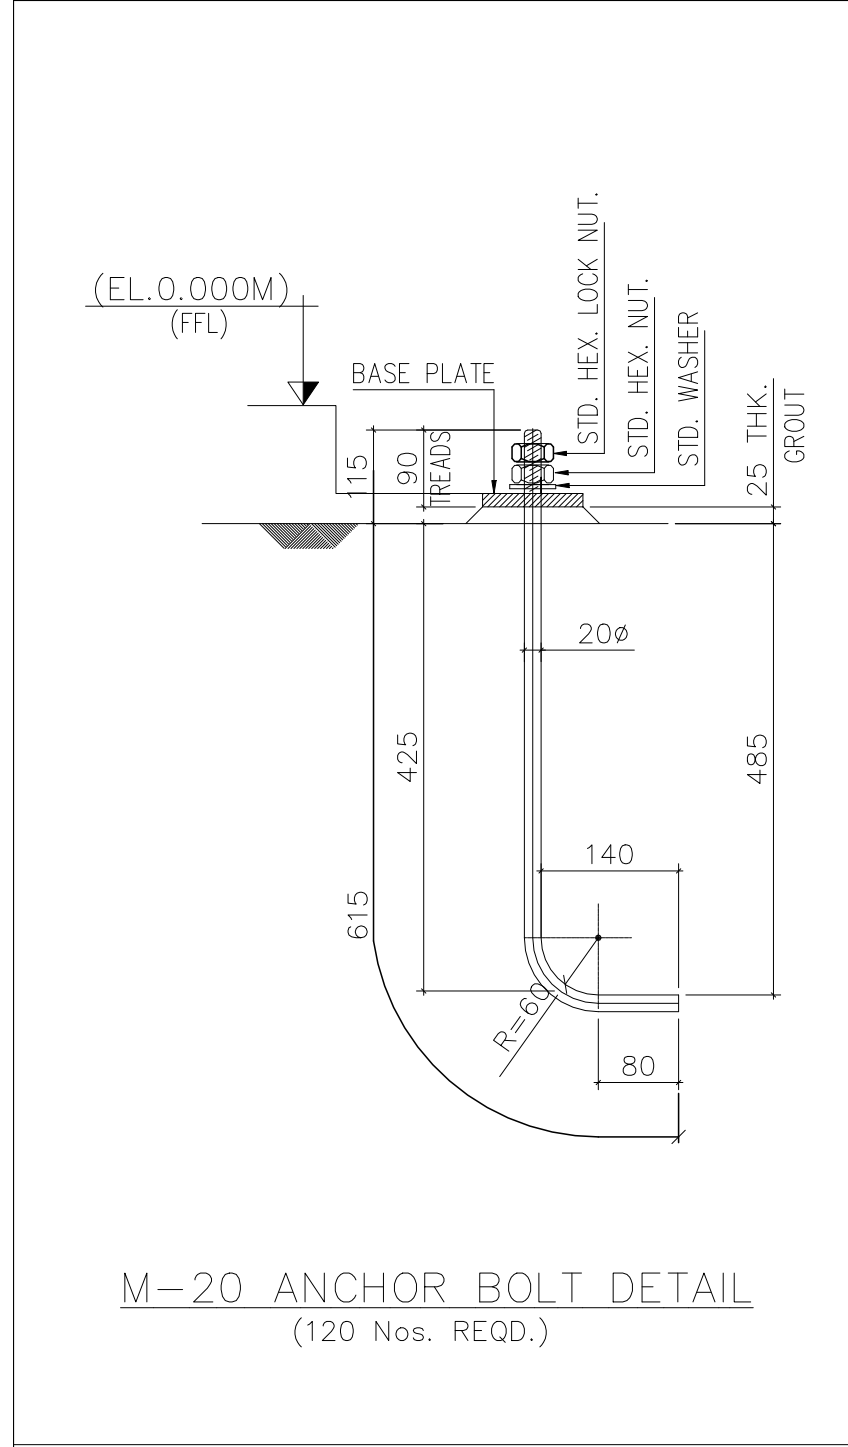

M-20 ANCHOR BOLT DETAIL  
(120 Nos. REQD.)

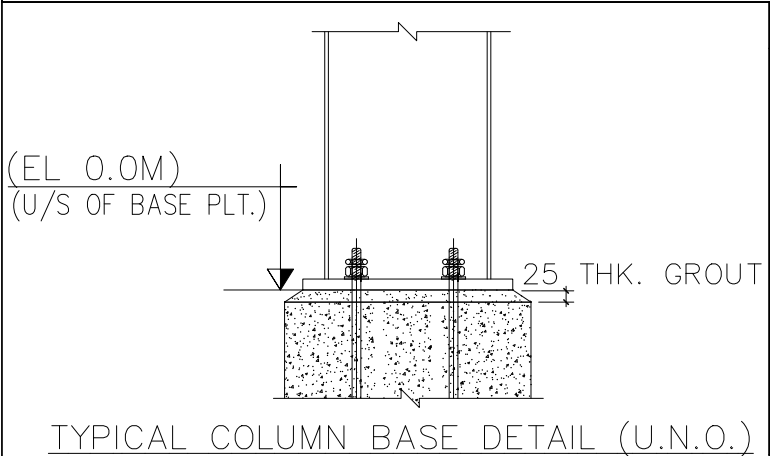

TYPICAL COLUMN BASE DETAIL (U.N.O.)

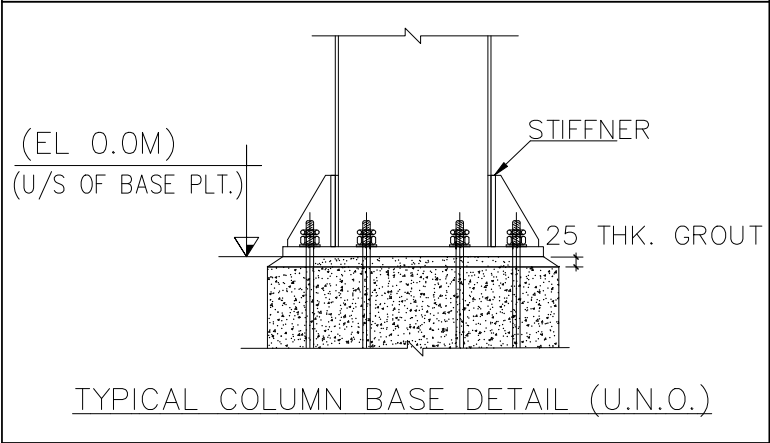

TYPICAL COLUMN BASE DETAIL (U.N.O.)

NOTES

1. THIS DRAWING IS TO BE READ IN CONJUNCTION WITH ALL OTHER RELEVANT ARCHITECTURAL AND STRUCTURAL DRAWINGS.
2. ALL DIMENSIONS ARE IN MILLIMETERS AND LEVELS ARE IN METERS UNLESS NOTED OTHERWISE.
3. DO NOT SCALE THE DRAWING.
4. ALL HOT ROLLED MEMBERS SHALL CONFORM TO BSEN 10025-S275 OR EQUIVALENT.
5. ALL THE BUILT UP MEMBERS SHALL CONFORM TO ASTM A572 OR BSEN 10025-S355
6. ALL WELDS ARE AWS STANDARD UNLESS OTHERWISE NOTED.
7. BOLTS FOR MAIN STRUCTURAL CONNECTIONS ARE ASTM A325
8. BOLTS FOR BRACINGS, PURLINS, GIRTS ETC.. ARE GRADE 8.8
9. PAINTING SYSTEM AND ALL OTHER TERMS AS PER CONTRACTS.



NOTE-THE DRAWING ARE INTENDED SOLELY FOR APPROVAL PURPOSES. CERTAIN PARTS OR DIMENSIONS MAY NOT BE TO SCALE AND THEREFORE MUST NOT BE USED FOR CONSTRUCTION OR ANY OTHER PURPOSE

RECLA INTERNATIONALS PRIVATE LIMITED

|         |          |                     |            |            |
|---------|----------|---------------------|------------|------------|
| PROJECT | SHED     | ANCHOR BOLT DETAILS |            |            |
| ID      | C323-153 | DESIGN: AAB         | DRAFT: AAB | CHECK: VVJ |
| PROJECT | PUNE     | DATE: 07/AUG/2025   |            |            |
| ADDRESS |          | C323-153_A02        |            |            |



RECLA

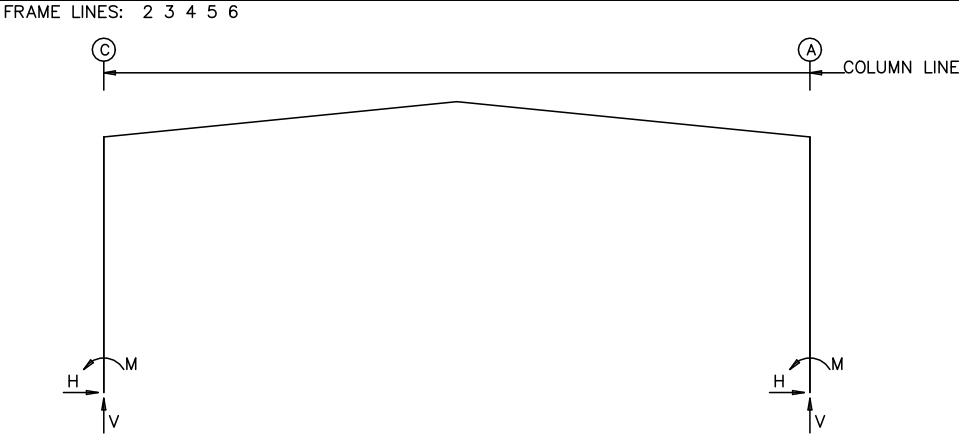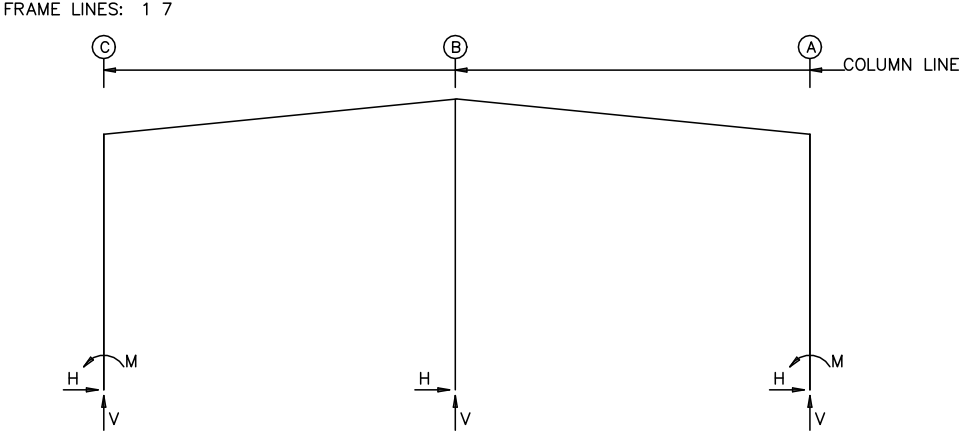

NOTES FOR REACTIONS

- All loading conditions are examined and only maximum/minimum H or V and the corresponding H or V are reported.
- Positive reactions are as shown in the sketch. Foundation loads are in opposite directions.
- Bracing reactions are in the plane of the brace with the H pointing away from the braced bay. The vertical reaction is downward.
- Building reactions are based on the following building data:

Width (mm)= 22470

Length (mm)= 35390

Eave Height (mm)= 8170/ 8170

Roof Slope (rise/100) =10.00/10.00

Roof Dead Load (kN/m2) = 0.10

Wall Dead Load

Left Endwall (kN/m2) = 0.10

Right Endwall (kN/m2) = 0.10

Front Sidewall (kN/m2) = 0.10

Back Sidewall (kN/m2) = 0.10

Live Load (kN/m2) = 0.57

Collateral Load (kN/m2) = 0.05

Wind Speed (m/s) = 39.0

Wind Code =MBMA10

Exposure =B

Closure =Enclosed

Internal Wind Coeff =-0.18, +0.18

Risk Category =-

Importance – Wind = 1.00

Importance – Seismic = 1.00

Seismic Design Category =B

Seismic Coeff (Sms) = 0.16

Temperature Change = 20
- Loading conditions are:

1 Dead+Collateral+Live

2 Dead+Collateral+0.75Live+0.75Wind\_Right2+0.75Floor\_Live

3 Dead+Collateral+0.75Live+0.75Wind\_Long2L+0.75Floor\_Live+0.75LWIND2\_L2E

4 0.6Dead+Wind\_Left1

5 0.6Dead+Wind\_Right1

6 0.6Dead+Wind\_Left2

7 0.6Dead+Wind\_Right2

8 0.6Dead+Wind\_Long1L+LWIND1\_L2E

9 0.6Dead+Wind\_Long1L+LWIND1\_R2E

10 Dead+Collateral+F1CRANEA2

11 Dead+Collateral+F1CRANEA3

12 Dead+Wind\_Left1/2+F1CRANEA1

13 Dead+Wind\_Right1/2+F1CRANEA4

14 Dead+Collateral+F2CRANEA2

15 Dead+Collateral+F2CRANEA3

16 0.6Dead+Wind\_Right1+Wind\_Suction

17 0.6Dead+Wind\_Pressure+Wind\_Long1L

RIGID FRAME: BASIC COLUMN REACTIONS (kN,kN-m)

| Frame Line | Column Line | ---Dead--- |      |       | ---Collateral--- |      |       | ---Live--- |      |       | ---Wind_Left1--- |       |       |
|------------|-------------|------------|------|-------|------------------|------|-------|------------|------|-------|------------------|-------|-------|
|            |             | Horz       | Vert | Mom   | Horz             | Vert | Mom   | Horz       | Vert | Mom   | Horz             | Vert  | Mom   |
| 1*         | C           | 1.3        | 7.5  | -2.07 | 0.5              | 1.7  | -0.81 | 5.4        | 19.3 | -9.17 | -17.1            | -25.5 | 39.42 |
| 1*         | A           | -1.3       | 7.5  | 2.08  | -0.5             | 1.7  | 0.81  | -5.4       | 19.3 | 9.22  | -9.4             | -12.1 | 25.08 |
| 1*         | B           | 0.0        | 10.7 | 0.00  | 0.0              | 3.3  | 0.00  | -0.8a      | 37.2 | 0.00  | 0.0              | -34.9 | 0.00  |

| Frame Line | Column Line | ---Wind_Right1--- |       |        | ---Wind_Left2--- |       |       | ---Wind_Right2--- |       |        | ---Wind_Press--- |      |      |
|------------|-------------|-------------------|-------|--------|------------------|-------|-------|-------------------|-------|--------|------------------|------|------|
|            |             | Horz              | Vert  | Mom    | Horz             | Vert  | Mom   | Horz              | Vert  | Mom    | Horz             | Vert | Mom  |
| 1*         | C           | 9.4               | -12.0 | -25.14 | -20.5            | -18.1 | 42.71 | 6.0               | -4.7  | -21.85 | 0.0              | 0.0  | 0.00 |
| 1*         | A           | 17.1              | -25.4 | -39.45 | -6.0             | -4.7  | 21.80 | 20.5              | -18.1 | -42.72 | 0.0              | 0.0  | 0.00 |
| 1*         | B           | 0.0               | -34.9 | 0.00   | 0.0              | -23.1 | 0.00  | 0.0               | -23.1 | 0.00   | -27.8a           | 0.0  | 0.00 |

| Frame Line | Column Line | ---Wind_Suct--- |      |      | ---Wind_Long1--- |       |       | ---Wind_Long2--- |       |       | ---Seismic_Left--- |      |      |
|------------|-------------|-----------------|------|------|------------------|-------|-------|------------------|-------|-------|--------------------|------|------|
|            |             | Horz            | Vert | Mom  | Horz             | Vert  | Mom   | Horz             | Vert  | Mom   | Horz               | Vert | Mom  |
| 1*         | C           | 0.0             | 0.0  | 0.00 | 4.8              | -17.4 | -3.62 | 1.3              | -10.1 | -0.33 | -1.3               | -0.2 | 8.20 |
| 1*         | A           | 0.0             | 0.0  | 0.00 | -4.8             | -17.4 | 3.58  | -1.3             | -10.1 | 0.31  | -1.3               | 0.2  | 8.20 |
| 1*         | B           | 32.6a           | 0.0  | 0.00 | 0.0              | -29.3 | 0.00  | 0.0              | -17.5 | 0.00  | 0.0                | 0.0  | 0.00 |

| Frame Line | Column Line | ---Seismic_Right--- |      |       | ---Temp--- |      |       | ---F1CRANEA1--- |      |       | ---F1CRANEA2--- |      |        |
|------------|-------------|---------------------|------|-------|------------|------|-------|-----------------|------|-------|-----------------|------|--------|
|            |             | Horz                | Vert | Mom   | Horz       | Vert | Mom   | Horz            | Vert | Mom   | Horz            | Vert | Mom    |
| 1*         | C           | 1.3                 | 0.2  | -8.20 | 0.9        | 0.4  | -4.92 | 0.3             | 59.3 | 27.94 | 8.1             | 60.0 | -11.21 |
| 1*         | A           | 1.3                 | -0.2 | -8.20 | -0.9       | 0.4  | 4.92  | -8.1            | 18.1 | 36.23 | -0.3            | 17.4 | -2.91  |
| 1*         | B           | 0.0                 | 0.0  | 0.00  | 0.0        | -0.7 | 0.00  | 0.0             | -0.7 | 0.00  | 0.0             | -0.7 | 0.00   |

| Frame Line | Column Line | ---F1CRANEA3--- |      |       | ---F1CRANEA4--- |      |        | ---LWIND1_L2E--- |      |       | ---LWIND1_R2E--- |      |      |
|------------|-------------|-----------------|------|-------|-----------------|------|--------|------------------|------|-------|------------------|------|------|
|            |             | Horz            | Vert | Mom   | Horz            | Vert | Mom    | Horz             | Vert | Mom   | Horz             | Vert | Mom  |
| 1*         | C           | 0.3             | 17.4 | 3.01  | 8.1             | 18.1 | -36.14 | -0.2             | -5.1 | -3.83 | -0.8             | 0.0  | 5.34 |
| 1*         | A           | -8.1            | 60.0 | 11.28 | -0.3            | 59.3 | -27.86 | 0.8              | 0.0  | -5.35 | 0.2              | -5.1 | 3.82 |
| 1*         | B           | 0.0             | -0.7 | 0.00  | 0.0             | -0.7 | 0.00   | 0.0              | -0.4 | 0.00  | 0.0              | -0.5 | 0.00 |

| Frame Line | Column Line | ---LWIND2_L2E--- |      |       | ---LWIND2_R2E--- |      |      | ---F1PAT_LL_1--- |      |       | ---F1PAT_LL_2--- |      |        |
|------------|-------------|------------------|------|-------|------------------|------|------|------------------|------|-------|------------------|------|--------|
|            |             | Horz             | Vert | Mom   | Horz             | Vert | Mom  | Horz             | Vert | Mom   | Horz             | Vert | Mom    |
| 1*         | C           | -0.2             | -5.1 | -3.83 | -0.8             | 0.0  | 5.34 | 2.7              | 21.4 | 16.52 | 2.7              | -2.1 | -25.69 |
| 1*         | A           | 0.8              | 0.0  | -5.35 | 0.2              | -5.1 | 3.82 | -2.7             | -2.1 | 25.73 | -2.7             | 21.4 | -16.51 |
| 1*         | B           | 0.0              | -0.4 | 0.00  | 0.0              | -0.5 | 0.00 | 0.0              | 18.4 | 0.00  | 0.0              | 18.8 | 0.00   |

| Frame Line | Column Line | ---Dead--- |      |        | ---Collateral--- |      |       | ---Live--- |      |        | ---Wind_Left1--- |       |       |
|------------|-------------|------------|------|--------|------------------|------|-------|------------|------|--------|------------------|-------|-------|
|            |             | Horz       | Vert | Mom    | Horz             | Vert | Mom   | Horz       | Vert | Mom    | Horz             | Vert  | Mom   |
| 2*         | C           | 5.8        | 12.2 | -12.93 | 2.1              | 3.4  | -4.76 | 24.0       | 39.0 | -53.97 | -27.0            | -31.6 | 69.23 |
| 2*         | A           | -5.8       | 12.2 | 12.98  | -2.1             | 3.4  | 4.78  | -24.0      | 39.0 | 54.20  | -0.1             | -22.5 | 3.10  |

| Frame Line | Column Line | ---Wind_Right1--- |       |        | ---Wind_Left2--- |       |       | ---Wind_Right2--- |       |        | ---Wind_Long1--- |       |        |
|------------|-------------|-------------------|-------|--------|------------------|-------|-------|-------------------|-------|--------|------------------|-------|--------|
|            |             | Horz              | Vert  | Mom    | Horz             | Vert  | Mom   | Horz              | Vert  | Mom    | Horz             | Vert  | Mom    |
| 2*         | C           | 0.1               | -22.5 | -3.25  | -27.5            | -18.0 | 62.31 | -0.4              | -8.9  | -10.16 | -9.6             | -48.3 | 31.21  |
| 2*         | A           | 27.0              | -31.6 | -69.39 | 0.4              | -8.9  | 10.09 | 27.5              | -18.0 | -62.40 | 9.6              | -48.6 | -31.39 |

| Frame Line | Column Line | ---Wind_Long2--- |       |        | ---Seismic_Left--- |      |      | ---Seismic_Right--- |      |       | ---Seismic_Long1--- |      |      |
|------------|-------------|------------------|-------|--------|--------------------|------|------|---------------------|------|-------|---------------------|------|------|
|            |             | Horz             | Vert  | Mom    | Horz               | Vert | Mom  | Horz                | Vert | Mom   | Horz                | Vert | Mom  |
| 2*         | C           | -7.3             | -34.6 | 20.51  | -1.2               | -0.2 | 7.15 | 1.2                 | 0.2  | -7.15 | 0.0                 | -2.0 | 0.00 |
| 2*         | A           | 7.3              | -35.0 | -20.61 | -1.2               | 0.2  | 7.16 | 1.2                 | -0.2 | -7.16 | 0.0                 | -2.0 | 0.00 |

| Frame Line | Column Line | ---Seismic_Long2--- |      |      | ---Temp--- |      |       | ---F2CRANEA1--- |      |       | ---F2CRANEA2--- |      |        |
|------------|-------------|---------------------|------|------|------------|------|-------|-----------------|------|-------|-----------------|------|--------|
|            |             | Horz                | Vert | Mom  | Horz       | Vert | Mom   | Horz            | Vert | Mom   | Horz            | Vert | Mom    |
| 2*         | C           | 0.0                 | 2.0  | 0.00 | 0.5        | 0.0  | -4.00 | 0.2             | 62.1 | 27.37 | 8.2             | 63.1 | -10.76 |
| 2*         | A           | 0.0                 | 2.0  | 0.00 | -0.5       | 0.0  | 4.00  | -8.2            | 20.4 | 34.57 | -0.2            | 19.5 | -3.57  |

| Frame Line | Column Line | ---F2CRANEA3--- |      |       | ---F2CRANEA4--- |      |        | ---LWIND1_L2E--- |      |       | ---LWIND1_R2E--- |      |      |
|------------|-------------|-----------------|------|-------|-----------------|------|--------|------------------|------|-------|------------------|------|------|
|            |             | Horz            | Vert | Mom   | Horz            | Vert | Mom    | Horz             | Vert | Mom   | Horz             | Vert | Mom  |
| 2*         | C           | 0.2             | 19.5 | 3.66  | 8.2             | 20.4 | -34.47 | -0.4             | -5.4 | -3.36 | -1.0             | -0.3 | 5.94 |
| 2*         | A           | -8.2            | 63.1 | 10.83 | -0.2            | 62.2 | -27.31 | 1.0              | -0.3 | -5.95 | 0.4              | -5.4 | 3.36 |

| Frame Line | Column Line | ---LWIND2_L2E--- |      |       | ---LWIND2_R2E--- |      |      |  |  |  |  |  |  |
|------------|-------------|------------------|------|-------|------------------|------|------|--|--|--|--|--|--|
|            |             | Horz             | Vert | Mom   | Horz             | Vert | Mom  |  |  |  |  |  |  |
| 2*         | C           | -0.4             | -5.4 | -3.36 | -1.0             | -0.3 | 5.94 |  |  |  |  |  |  |
| 2*         | A           | 1.0              | -0.3 | -5.95 | 0.4              | -5.4 | 3.36 |  |  |  |  |  |  |

1\* Frame lines: 1 7

2\* Frame lines: 2 3 4 5 6

a – Out-Of-Plane Horizontal Load

RIGID FRAME: ANCHOR BOLTS & BASE PLATES

| Frm Line | Col Line | Anc. Bolt Qty | Dia | Base_Plate (mm) |        |       | Grout (mm) |                               |
|----------|----------|---------------|-----|-----------------|--------|-------|------------|-------------------------------|
|          |          |               |     | Width           | Length | Thick |            |                               |
| 1*       | C        | 8             | 20  | 200             | 705    | 16    | 0          | Moment connection. See table. |
| 1*       | A        | 8             | 20  | 200             | 705    | 16    | 0          |                               |
| 1*       | B        | 4             | 20  | 200             | 450    | 16    | 0          |                               |

1\* Frame lines: 1 7

RIGID FRAME: ANCHOR BOLTS & BASE PLATES

| Frm Line | Col Line | Anc. Bolt Qty | Dia | Base_Plate (mm) |        |       | Grout (mm) |                               |
|----------|----------|---------------|-----|-----------------|--------|-------|------------|-------------------------------|
|          |          |               |     | Width           | Length | Thick |            |                               |
| 2*       | C        | 8             | 20  | 200             | 705    | 16    | 0          | Moment connection. See table. |
| 2*       | A        | 8             | 20  | 200             | 705    | 16    | 0          |                               |

2\* Frame lines: 2 3 4 5 6

BUILDING BRACING REACTIONS

| Loc  | Wall Line | Col Line | Reactions in plane of wall |              | Panel Shear (N/m) | Note |
|------|-----------|----------|----------------------------|--------------|-------------------|------|
|      |           |          | Wind Horz                  | Seismic Horz |                   |      |
| L_EW | 1         |          |                            |              |                   | (h)  |
| F_SW | A         | 2,3 5,6  | *                          | 12.2         | 2.0               |      |
| R_EW | 7         |          |                            |              |                   | (h)  |
| B_SW | C         | 6,5 3,2  | *                          | 11.9         | 2.0               |      |

(h)Rigid frame at endwall

\*See RF reactions table for vertical and horizontal reactions in plane of the rigid frame.

Reactions for seismic represent shear force, Eh  
Reaction values shown are unfactored



RECLA

|   |          |                  |            |            |
|---|----------|------------------|------------|------------|
| NOTE-THE DRAWING ARE INTENDED SOLELY FOR APPROVAL PURPOSES. CERTAIN PARTS OR DIMENSIONS MAY NOT BE TO SCALE AND THEREFORE MUST NOT BE USED FOR CONSTRUCTION OR ANY OTHER PURPOSE |          |                  |            |            |
| RECLA INTERNATIONALS PRIVATE LIMITED   |          |                  |            |            |
| PROJECT   | SLED     |                  |            |            |
| ID   | C323-153 | DESIGN: AAB      | DRAFT: AAB | CHECK: VVJ |
| PROJECT   | PUNE     | DATE: 7/AUG/2025 |            |            |
| ADDRESS   |          | C323-153_A03     |            |            |



| SPLICE PLATES & BOLTS |      |         |     |       |          |     |            |       |        |
|-----------------------|------|---------|-----|-------|----------|-----|------------|-------|--------|
| Splice Mark           | Quan | Top/Bot | Int | Type  | Bolt Dia | Len | Plate Size |       |        |
|                       |      |         |     |       |          |     | Wid        | Thick | Length |
| SP1                   | 4    | 4       |     | Gr8.8 | 20       |     | 90         | 200   | 16     |
| SP2                   | 4    | 4       |     | Gr8.8 | 20       |     | 90         | 200   | 16     |

900  
500

| CAP PLATES |     |       |          |     |            |       |        |  |  |
|------------|-----|-------|----------|-----|------------|-------|--------|--|--|
| Col Id     | Qnt | Type  | Bolt Dia | Len | Plate Size |       |        |  |  |
|            |     |       |          |     | Width      | Thick | Length |  |  |
| EC-1       | 4   | Gr8.8 | 20       | 90  | 200        | 16    | 410    |  |  |

| MEMBER TABLE |           |           |           |              |                  |                  |
|--------------|-----------|-----------|-----------|--------------|------------------|------------------|
| Mark         | Web Depth | Start/End | Web Thick | Plate Length | Outside Flange   | Inside Flange    |
|              |           |           |           |              | W x Thk x Length | W x Thk x Length |
| CL1-1        | 400/      | 700       | 5         | 4000         | 150 x 6 x 7918   | 150 x 6 x 4011   |
| RF1-2        | 700/      | 700       | 5         | 3918         |                  | 150 x 6 x 3918   |
|              | 401/      | 300       | 4         | 4483         | 125 x 5 x 322    | 125 x 5 x 3685   |
| RF1-3        | 300/      | 300       | 4         | 4000         | 125 x 5 x 4677   |                  |
|              | 302/      | 553       | 4         | 5053         | 125 x 5 x 4000   | 125 x 5 x 4000   |
| CL1-5        | 700/      | 700       | 5         | 3918         | 150 x 5 x 2539   | 150 x 5 x 4992   |
|              | 700/      | 400       | 5         | 4000         | 150 x 5 x 2539   | 150 x 5 x 2539   |
| EC-1         | W40b      | 155       |           |              | 150 x 6 x 7918   | 150 x 6 x 4011   |

▽FLANGE BRACES: FBxx (1 or 2)  
xx=length(mm)  
(1) One Side; (2) Two Sides  
A - L40X40X4

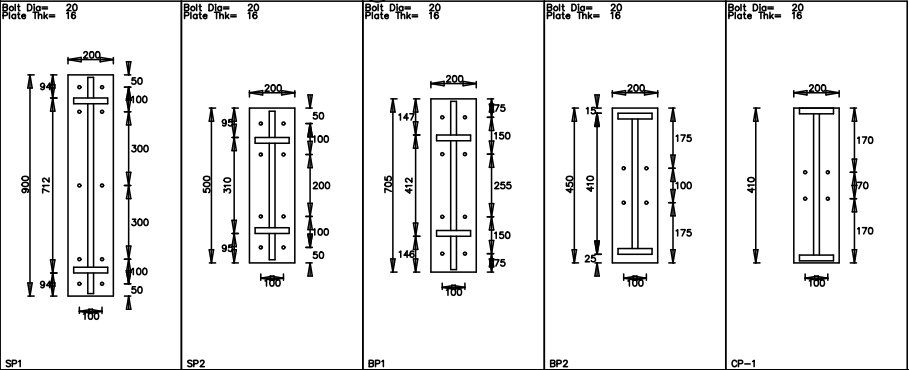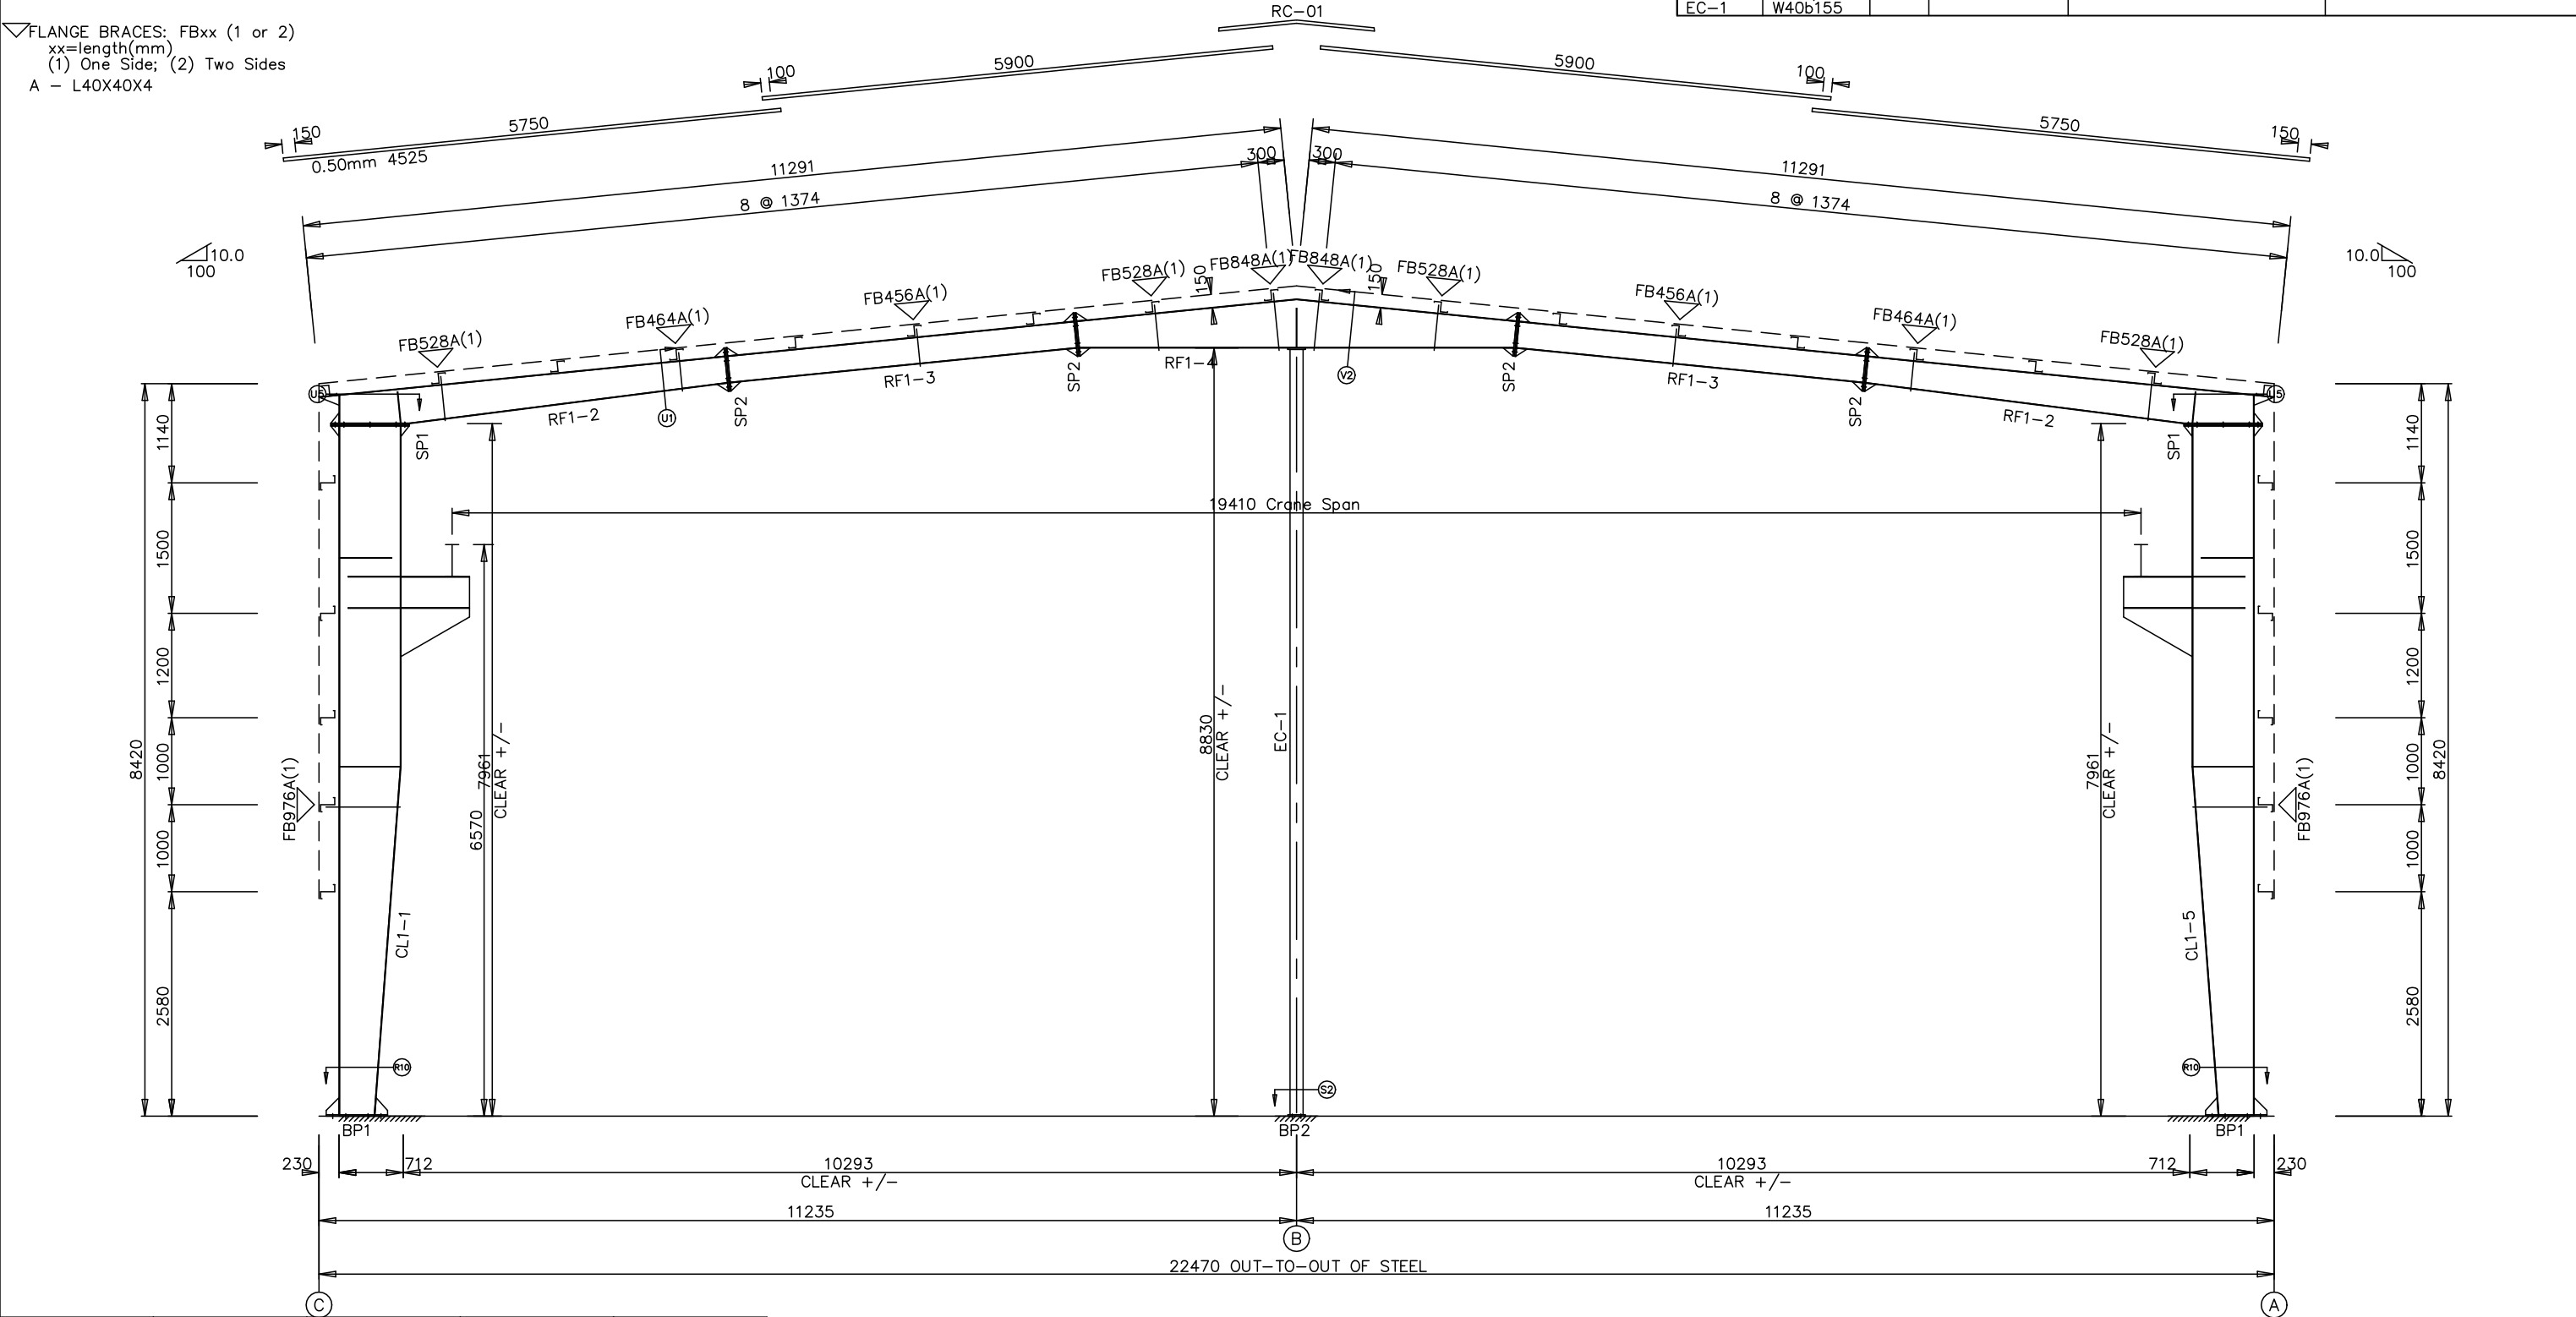


RIGID FRAME ELEVATION: FRAME LINE 1

| INFINITI SOLUTION |                    |                            |        |        |
|-------------------|--------------------|----------------------------|--------|--------|
| PROJECT           | Proposed Warehouse | RIGID FRAME ELEVATION      |        |        |
| ID                | C323-153-Final     | DESIGN:                    | DRAFT: | CHECK: |
| PROJECT ADDRESS   | Proposed Warehouse | DATE: 11/AUG/2025 SHEET OF |        |        |


| SPLICE PLATES & BOLTS |         |     |       |     |     |            |       |        |  |
|-----------------------|---------|-----|-------|-----|-----|------------|-------|--------|--|
| Splice Mark           | Quan    |     | Bolt  |     |     | Plate Size |       |        |  |
|                       | Top/Bot | Int | Type  | Dia | Len | Wid        | Thick | Length |  |
| SP1                   | 4       | 4   | ⌀r8.8 | 20  | 90  | 200        | 16    | 900    |  |
| SP2                   | 4       | 4   | ⌀r8.8 | 20  | 90  | 200        | 16    | 450    |  |
| SP3                   | 4       | 4   | ⌀r8.8 | 20  | 90  | 200        | 16    | 653    |  |

| MEMBER TABLE |           |       |           |  |                                    |
|--------------|-----------|-------|-----------|--|------------------------------------|
| Mark         | Web Depth |       | Web Plate |  | Outside Flange<br>W x Thk x Length |
|              | Start/End | Thick | Length    |  |                                    |
| CL2-1        | 400 / 700 | 5     | 4000      |  | 150 x 6 x 7716                     |
|              | 700 / 700 | 5     | 3716      |  | 150 x 6 x 4011                     |
| RF2-2        | 521 / 601 | 5     | 799       |  | 125 x 6 x 523                      |
|              | 601 / 252 | 4     | 3715      |  | 125 x 6 x 4689                     |
| RF2-3        | 250 / 450 | 4     | 6543      |  | 125 x 5 x 6543                     |
|              |           |       |           |  | 125 x 5 x 6501                     |

▽ FLANGE BRACES: FBxx (1 or 2)  
xx=length(mm)  
(1) One Side; (2) Two Sides  
A - L40X40X4

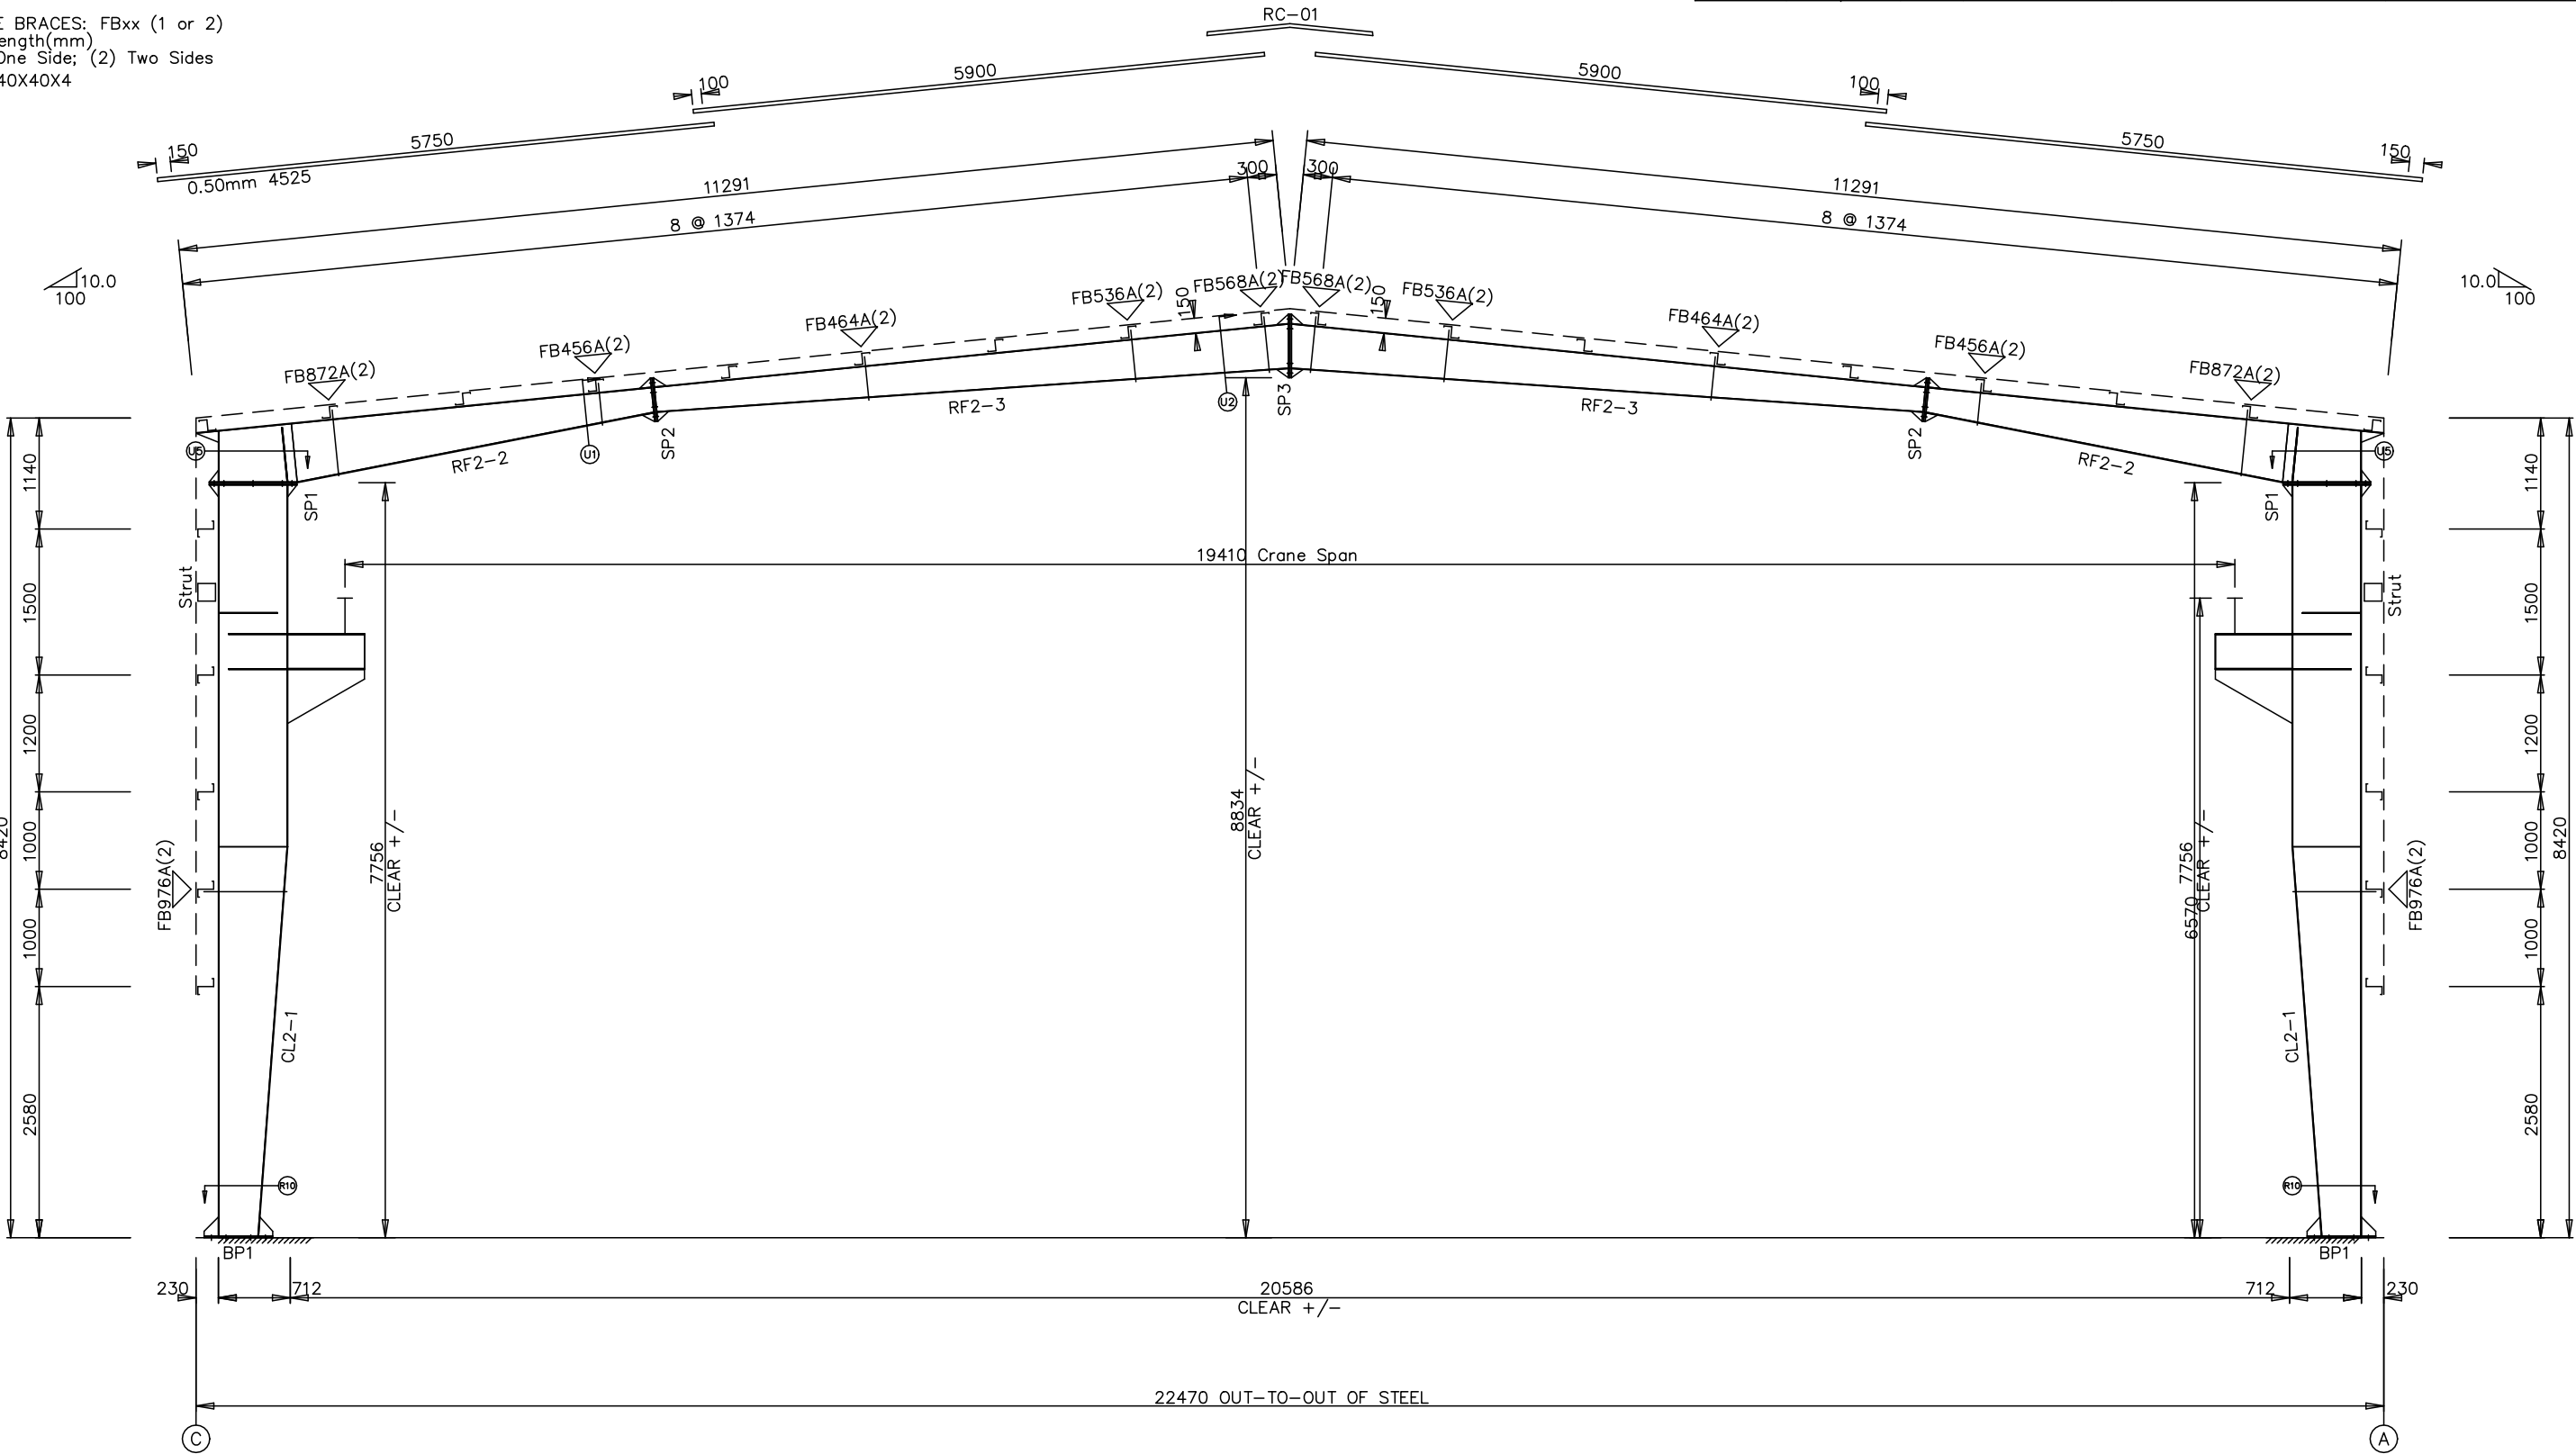

RIGID FRAME ELEVATION: FRAME LINE 2 3 5

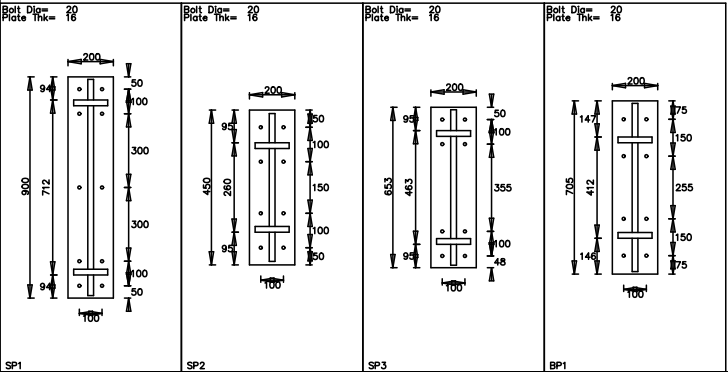


| INFINITI SOLUTION |                    |                            |        |        |
|-------------------|--------------------|----------------------------|--------|--------|
| PROJECT           | Proposed Warehouse | RIGID FRAME ELEVATION      |        |        |
| ID                | C323-153-Final     | DESIGN:                    | DRAFT: | CHECK: |
| PROJECT ADDRESS   | Proposed Warehouse | DATE: 11/AUG/2025 SHEET OF |        |        |



| MEMBER |                        | TABLE        |                 |                                    |            |                                   |            |  |  |
|--------|------------------------|--------------|-----------------|------------------------------------|------------|-----------------------------------|------------|--|--|
| Mark   | Web Depth<br>Start/End | Web<br>Thick | Plate<br>Length | Outside Flange<br>W x Thk x Length |            | Inside Flange<br>W x Thk x Length |            |  |  |
| CL3-1  | 400/ 700               | 5            | 4000            | 150                                | x 6 x 7716 | 150                               | x 6 x 4011 |  |  |
|        | 700/ 700               | 5            | 3716            |                                    |            | 150                               | x 6 x 3716 |  |  |
| RF3-2  | 521/ 601               | 5            | 799             | 125                                | x 6 x 523  | 125                               | x 6 x 3731 |  |  |
|        | 601/ 252               | 4            | 3715            | 125                                | x 6 x 4689 |                                   |            |  |  |
| RF3-3  | 250/ 450               | 4            | 6543            | 125                                | x 5 x 6543 | 125                               | x 5 x 6501 |  |  |

Figure 1 displays four technical drawings of bolted connections, labeled SP1, SP2, SP3, and BP1. Each drawing shows a side view of a connection with dimensions and bolt specifications.


- SP1:** Bolt Dia = 20, Plate Thk = 16. Dimensions: 200 (width), 50 (top plate), 100 (middle plate), 300 (bottom plate), 50 (bottom plate), 100 (bottom plate). Bolt spacing: 90, 712, 90.
- SP2:** Bolt Dia = 20, Plate Thk = 16. Dimensions: 200 (width), 50 (top plate), 100 (middle plate), 150 (bottom plate), 50 (bottom plate), 100 (bottom plate). Bolt spacing: 90, 260, 90.
- SP3:** Bolt Dia = 20, Plate Thk = 16. Dimensions: 200 (width), 50 (top plate), 100 (middle plate), 355 (bottom plate), 50 (bottom plate), 100 (bottom plate). Bolt spacing: 90, 463, 90.
- BP1:** Bolt Dia = 20, Plate Thk = 16. Dimensions: 200 (width), 75 (top plate), 150 (middle plate), 255 (bottom plate), 150 (bottom plate), 75 (bottom plate). Bolt spacing: 147, 412, 146.

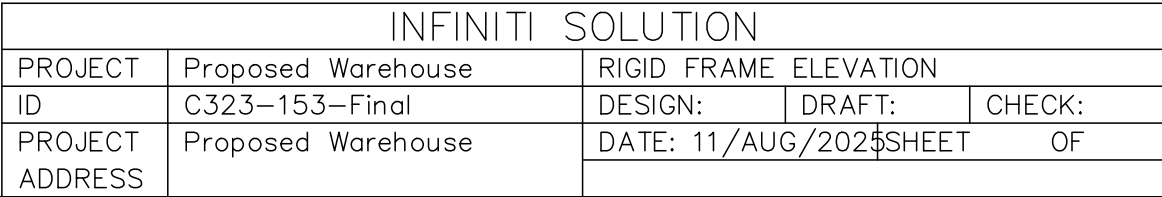


| SPLICE PLATES & BOLTS |         |     |       |     |     |            |       |        |
|-----------------------|---------|-----|-------|-----|-----|------------|-------|--------|
| Splice Mark           | Quan    |     | Bolt  |     |     | Plate Size |       |        |
|                       | Top/Bot | Int | Type  | Dia | Len | Wid        | Thick | Length |
| SP1                   | 4       | 4   | Ør8.8 | 20  | 90  | 200        | 16    | 900    |
| SP2                   | 4       | 4   | Ør8.8 | 20  | 90  | 200        | 16    | 450    |
| SP3                   | 4       | 4   | Ør8.8 | 20  | 90  | 200        | 16    | 653    |

| MEMBER TABLE |           |       |           |  |                                    |
|--------------|-----------|-------|-----------|--|------------------------------------|
| Mark         | Web Depth |       | Web Plate |  | Outside Flange<br>W x Thk x Length |
|              | Start/End | Thick | Length    |  |                                    |
| CL4-1        | 400 / 700 | 5     | 4000      |  | 150 x 6 x 7716                     |
|              | 700 / 700 | 5     | 3716      |  | 150 x 6 x 4011                     |
| RF4-2        | 521 / 601 | 5     | 799       |  | 125 x 6 x 523                      |
|              | 601 / 252 | 4     | 3715      |  | 125 x 6 x 4689                     |
| RF4-3        | 250 / 450 | 4     | 6543      |  | 125 x 5 x 6543                     |
|              |           |       |           |  | 125 x 5 x 6501                     |

▽ FLANGE BRACES: FBxx (1 or 2)  
xx=length(mm)  
(1) One Side; (2) Two Sides  
A - L40X40X4

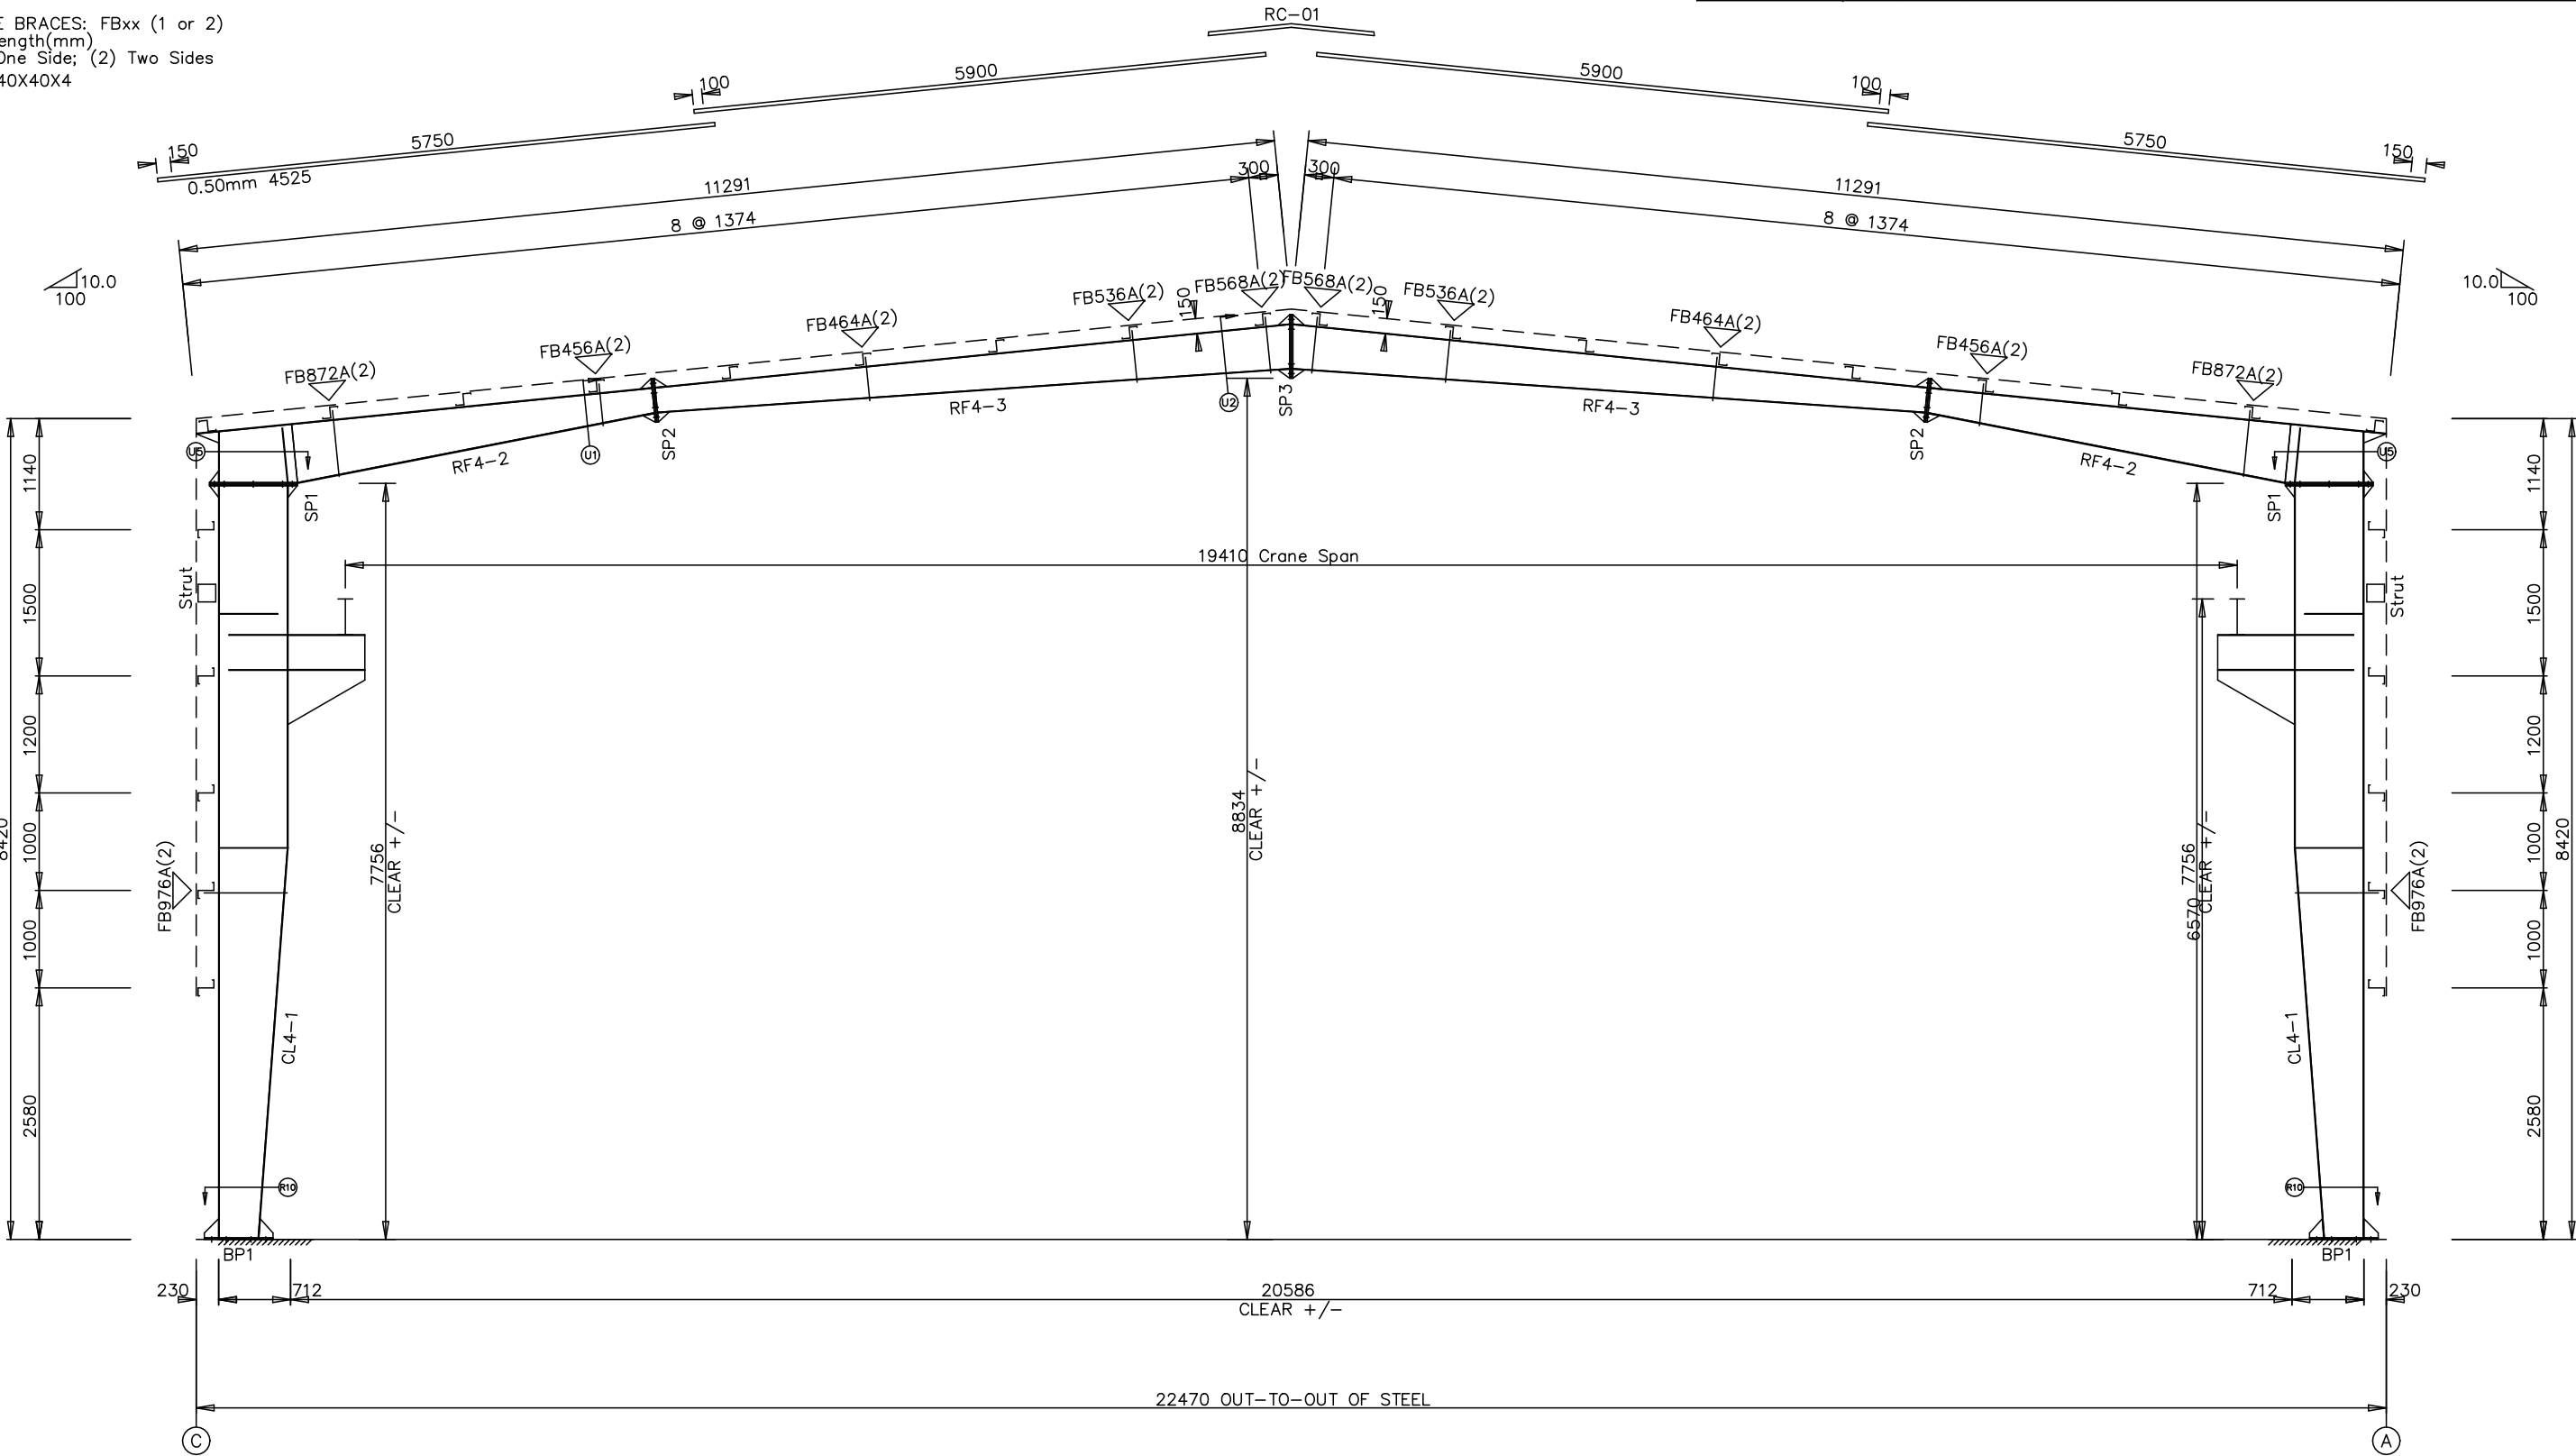

RIGID FRAME ELEVATION: FRAME LINE 6

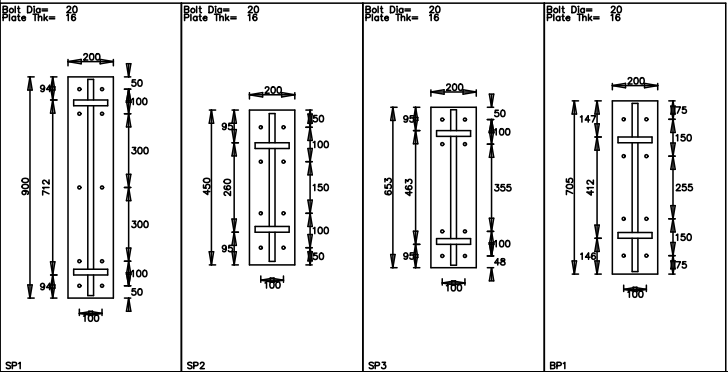

| INFINITI SOLUTION |                    |                            |        |        |
|-------------------|--------------------|----------------------------|--------|--------|
| PROJECT           | Proposed Warehouse | RIGID FRAME ELEVATION      |        |        |
| ID                | C323-153-Final     | DESIGN:                    | DRAFT: | CHECK: |
| PROJECT ADDRESS   | Proposed Warehouse | DATE: 11/AUG/2025 SHEET OF |        |        |





| SPLICE PLATES & BOLTS |      |         |     |       |          |     |     |       |        |
|-----------------------|------|---------|-----|-------|----------|-----|-----|-------|--------|
| Splice Mark           | Quan | Top/Bot | Int | Type  | Bolt Dia | Len | Wid | Thick | Length |
| SP1                   | 4    | 4       |     | Gr8.8 | 20       | 20  | 90  | 200   | 16     |
| SP2                   | 4    | 4       |     | Gr8.8 | 20       | 20  | 90  | 200   | 16     |

| CAP PLATES |     |       |          |     |       |       |        |  |  |
|------------|-----|-------|----------|-----|-------|-------|--------|--|--|
| Col Id     | Qnt | Type  | Bolt Dia | Len | Width | Thick | Length |  |  |
| EC-2       | 4   | Gr8.8 | 20       | 90  | 200   | 16    | 410    |  |  |

▽FLANGE BRACES: FBxx (1 or 2)  
xx=length(mm)  
(1) One Side; (2) Two Sides  
A - L40X40X4

| MEMBER TABLE |           |           |              |                |                |  |
|--------------|-----------|-----------|--------------|----------------|----------------|--|
| Mark         | Web Depth | Web Thick | Plate Length | Outside Flange | Inside Flange  |  |
| CL5-1        | 400/ 700  | 5         | 4000         | 150 x 6 x 7918 | 150 x 6 x 4011 |  |
| RF5-2        | 700/ 700  | 5         | 3918         | 125 x 5 x 322  | 150 x 6 x 3918 |  |
| RF5-3        | 401/ 300  | 4         | 4483         | 125 x 5 x 4677 | 125 x 5 x 3685 |  |
| RF5-4        | 300/ 300  | 4         | 4000         | 125 x 5 x 4000 | 125 x 5 x 4000 |  |
| RF5-5        | 302/ 553  | 4         | 5053         | 150 x 5 x 2539 | 150 x 5 x 4992 |  |
| CL5-5        | 700/ 700  | 5         | 3918         | 150 x 5 x 2539 | 150 x 6 x 3918 |  |
| EC-2         | 700/ 400  | 5         | 4000         | 150 x 6 x 7918 | 150 x 6 x 4011 |  |

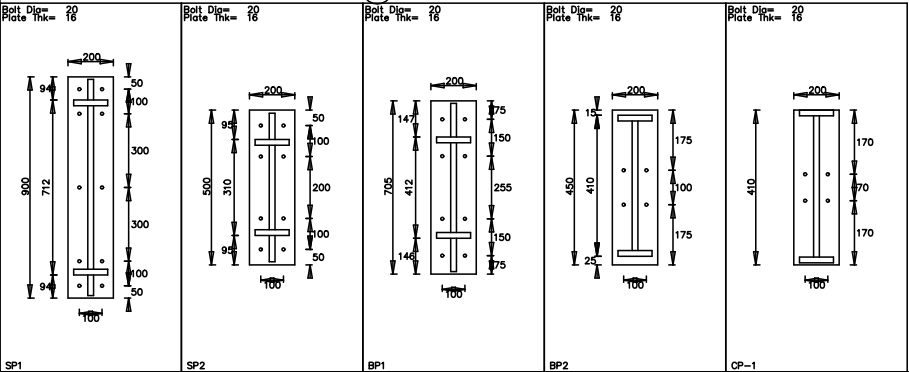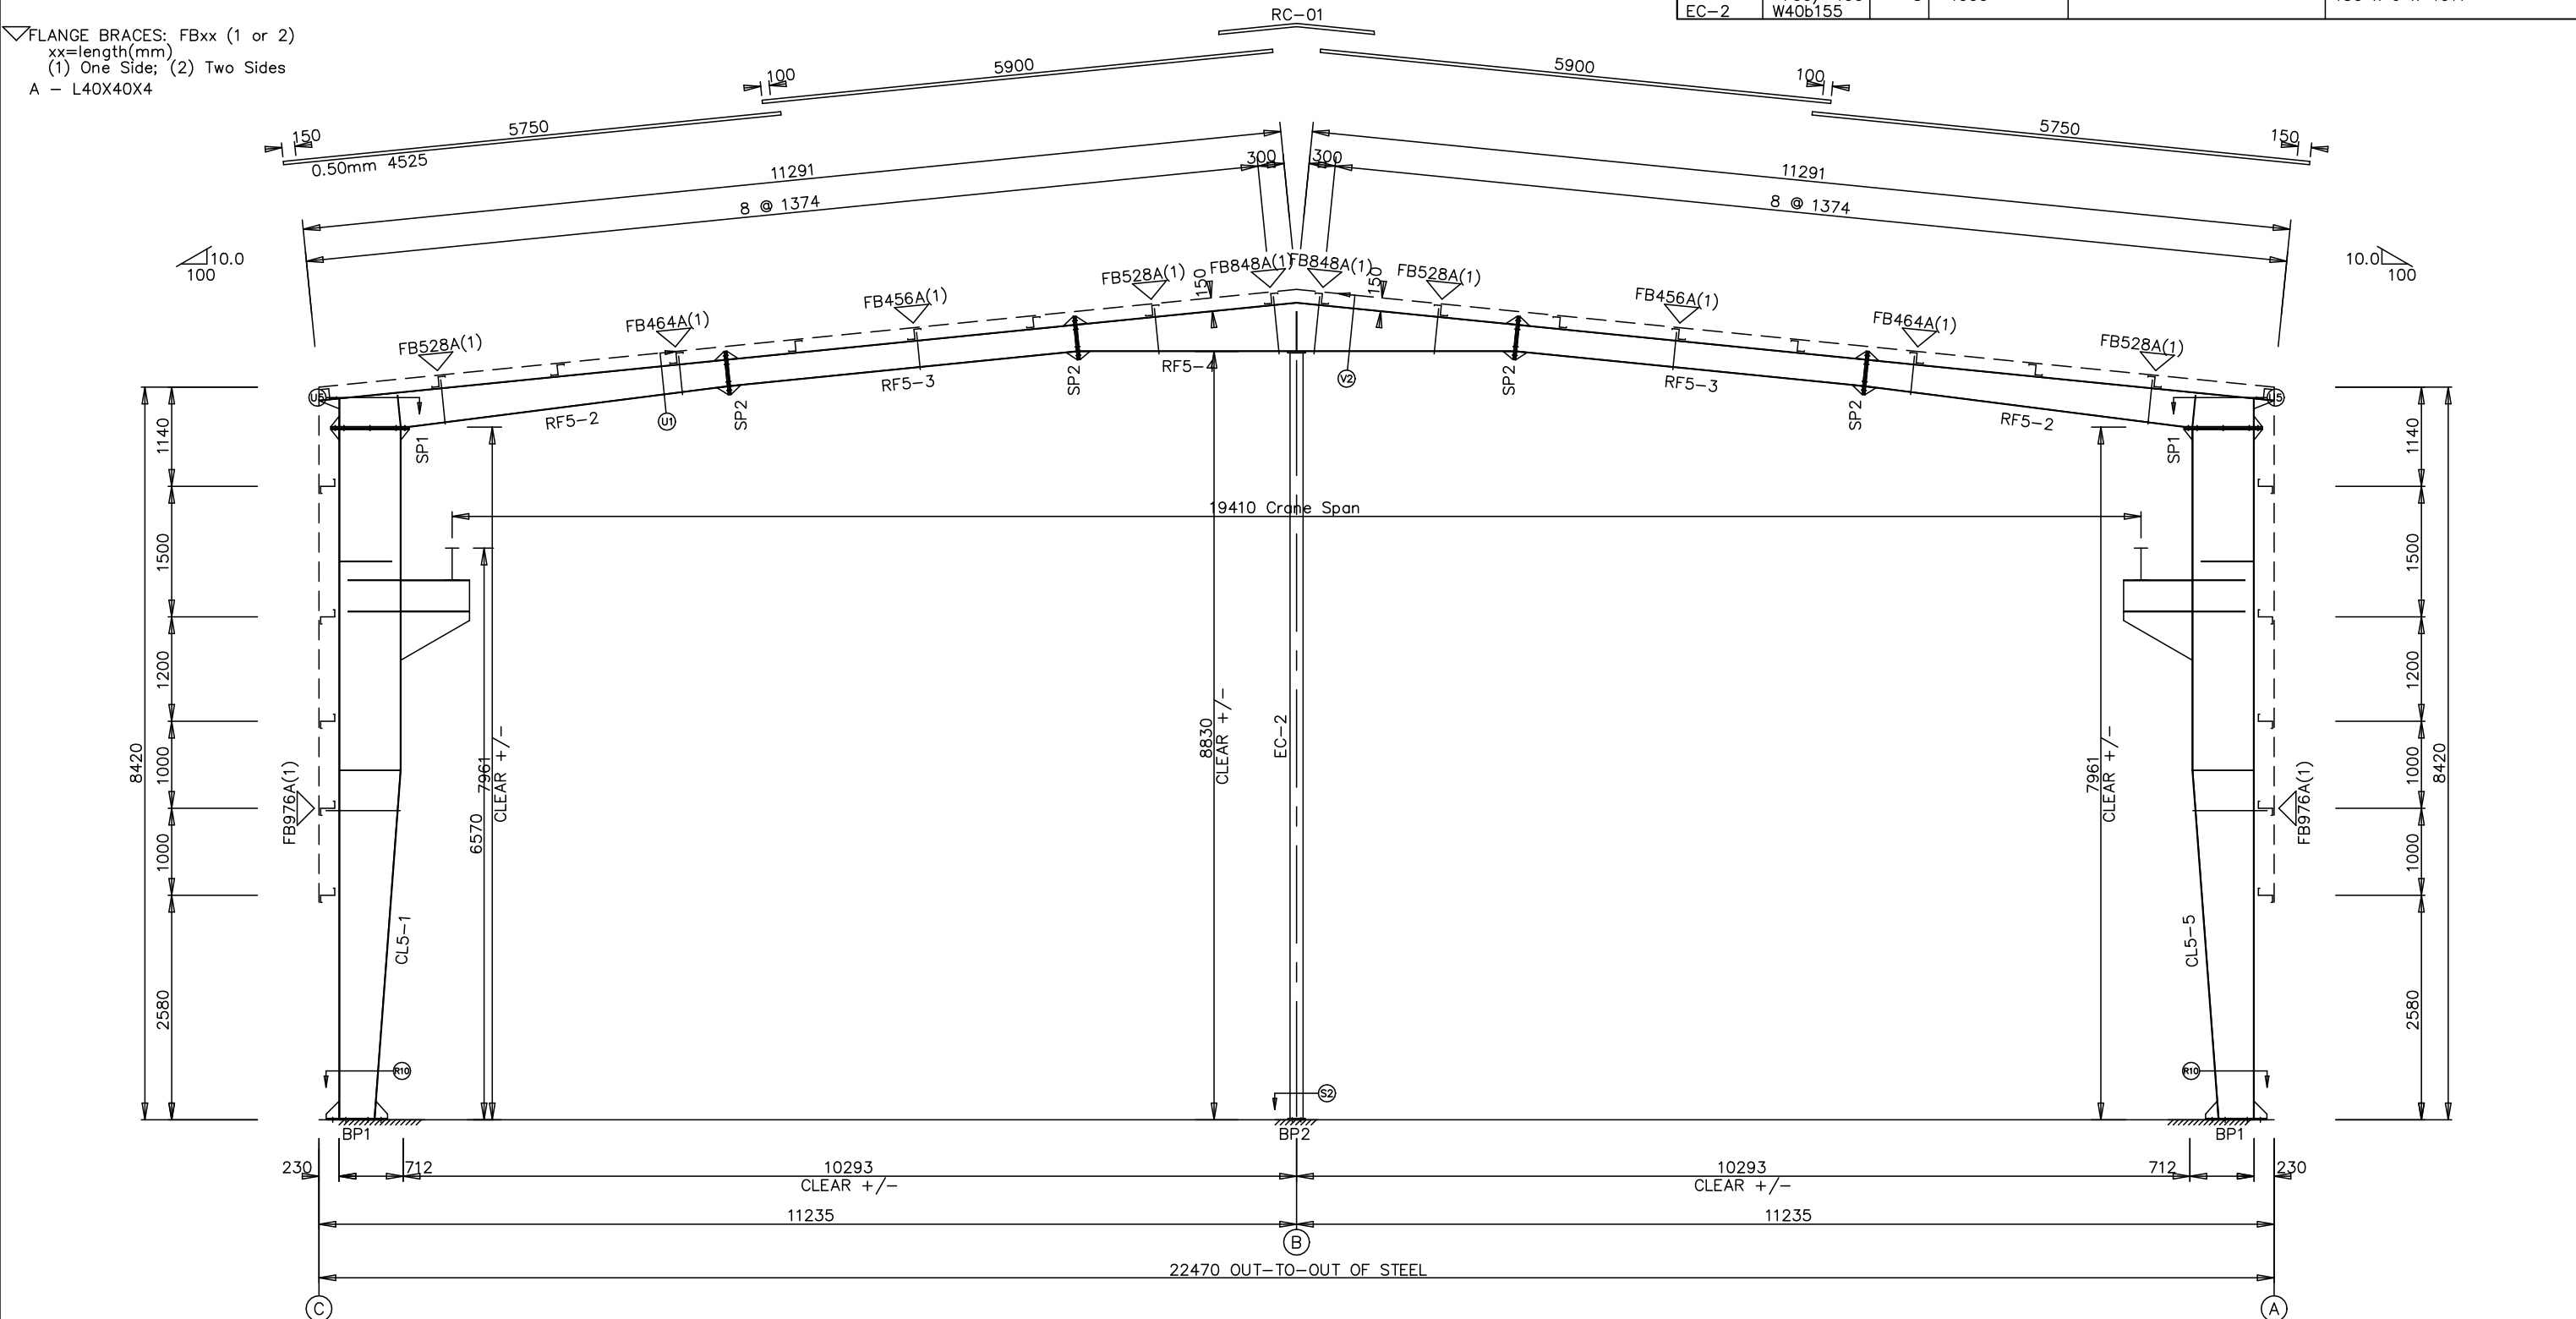


RIGID FRAME ELEVATION: FRAME LINE 7

| INFINITI SOLUTION |                    |                       |        |        |
|-------------------|--------------------|-----------------------|--------|--------|
| PROJECT           | Proposed Warehouse | RIGID FRAME ELEVATION |        |        |
| ID                | C323-153-Final     | DESIGN:               | DRAFT: | CHECK: |
| PROJECT ADDRESS   | Proposed Warehouse | DATE: 11/AUG/2025     | SHEET  | OF     |

| EXTENSION/CANOPY BOLTS |      |       |     |        |
|------------------------|------|-------|-----|--------|
| ROOF PLAN              |      |       |     |        |
| MARK                   | QUAN | TYPE  | DIA | LENGTH |
| EB-1                   | 8    | Gr8.8 | 20  | 90     |
| EB-3                   | 8    | Gr8.8 | 20  | 90     |
| EB-4                   | 8    | Gr8.8 | 20  | 90     |


| MEMBER TABLE |        |        |
|--------------|--------|--------|
| ROOF PLAN    |        |        |
| MARK         | PART   | LENGTH |
| EB-1         | BEAM   | 2272   |
| EB-3         | BEAM   | 1830   |
| EB-4         | BEAM   | 2272   |
| P-1          | 150Z15 | 6570   |
| P-2          | 150Z15 | 6740   |
| P-3          | 150Z15 | 6895   |
| P-4          | 150Z15 | 6450   |
| P-5          | 150Z15 | 6750   |
| P-6          | 150Z15 | 6620   |
| P-7          | 150Z15 | 6570   |
| P-8          | 150Z15 | 6620   |
| P-9          | 250Z18 | 12235  |
| P-10         | 250Z18 | 12235  |
| E-1          | 150Z15 | 6570   |
| E-2          | 150Z15 | 6740   |
| E-3          | 150Z15 | 6895   |
| E-4          | 150Z15 | 6450   |
| E-5          | 150Z15 | 6750   |
| E-6          | 150Z15 | 6620   |
| E-7          | 150Z15 | 6570   |
| E-8          | 150Z15 | 6620   |
| E-9          | 250Z18 | 12240  |
| E-10         | 250Z18 | 12240  |
| CB-5         | ROD20  | 7770   |
| CB-6         | ROD20  | 8080   |
| CB-7         | ROD20  | 7780   |
| CB-8         | ROD20  | 8090   |
| SP-1         | SROD12 | 697    |
| SI-1         | SROD12 | 1474   |
| SE-1         | SROD12 | 1394   |
| SI-          | SROD12 | 1519   |

| ANGLE TABLE |      |        |
|-------------|------|--------|
| ROOF PLAN   |      |        |
| ◊ID         | MARK | LENGTH |
|             | GA   | 3000   |

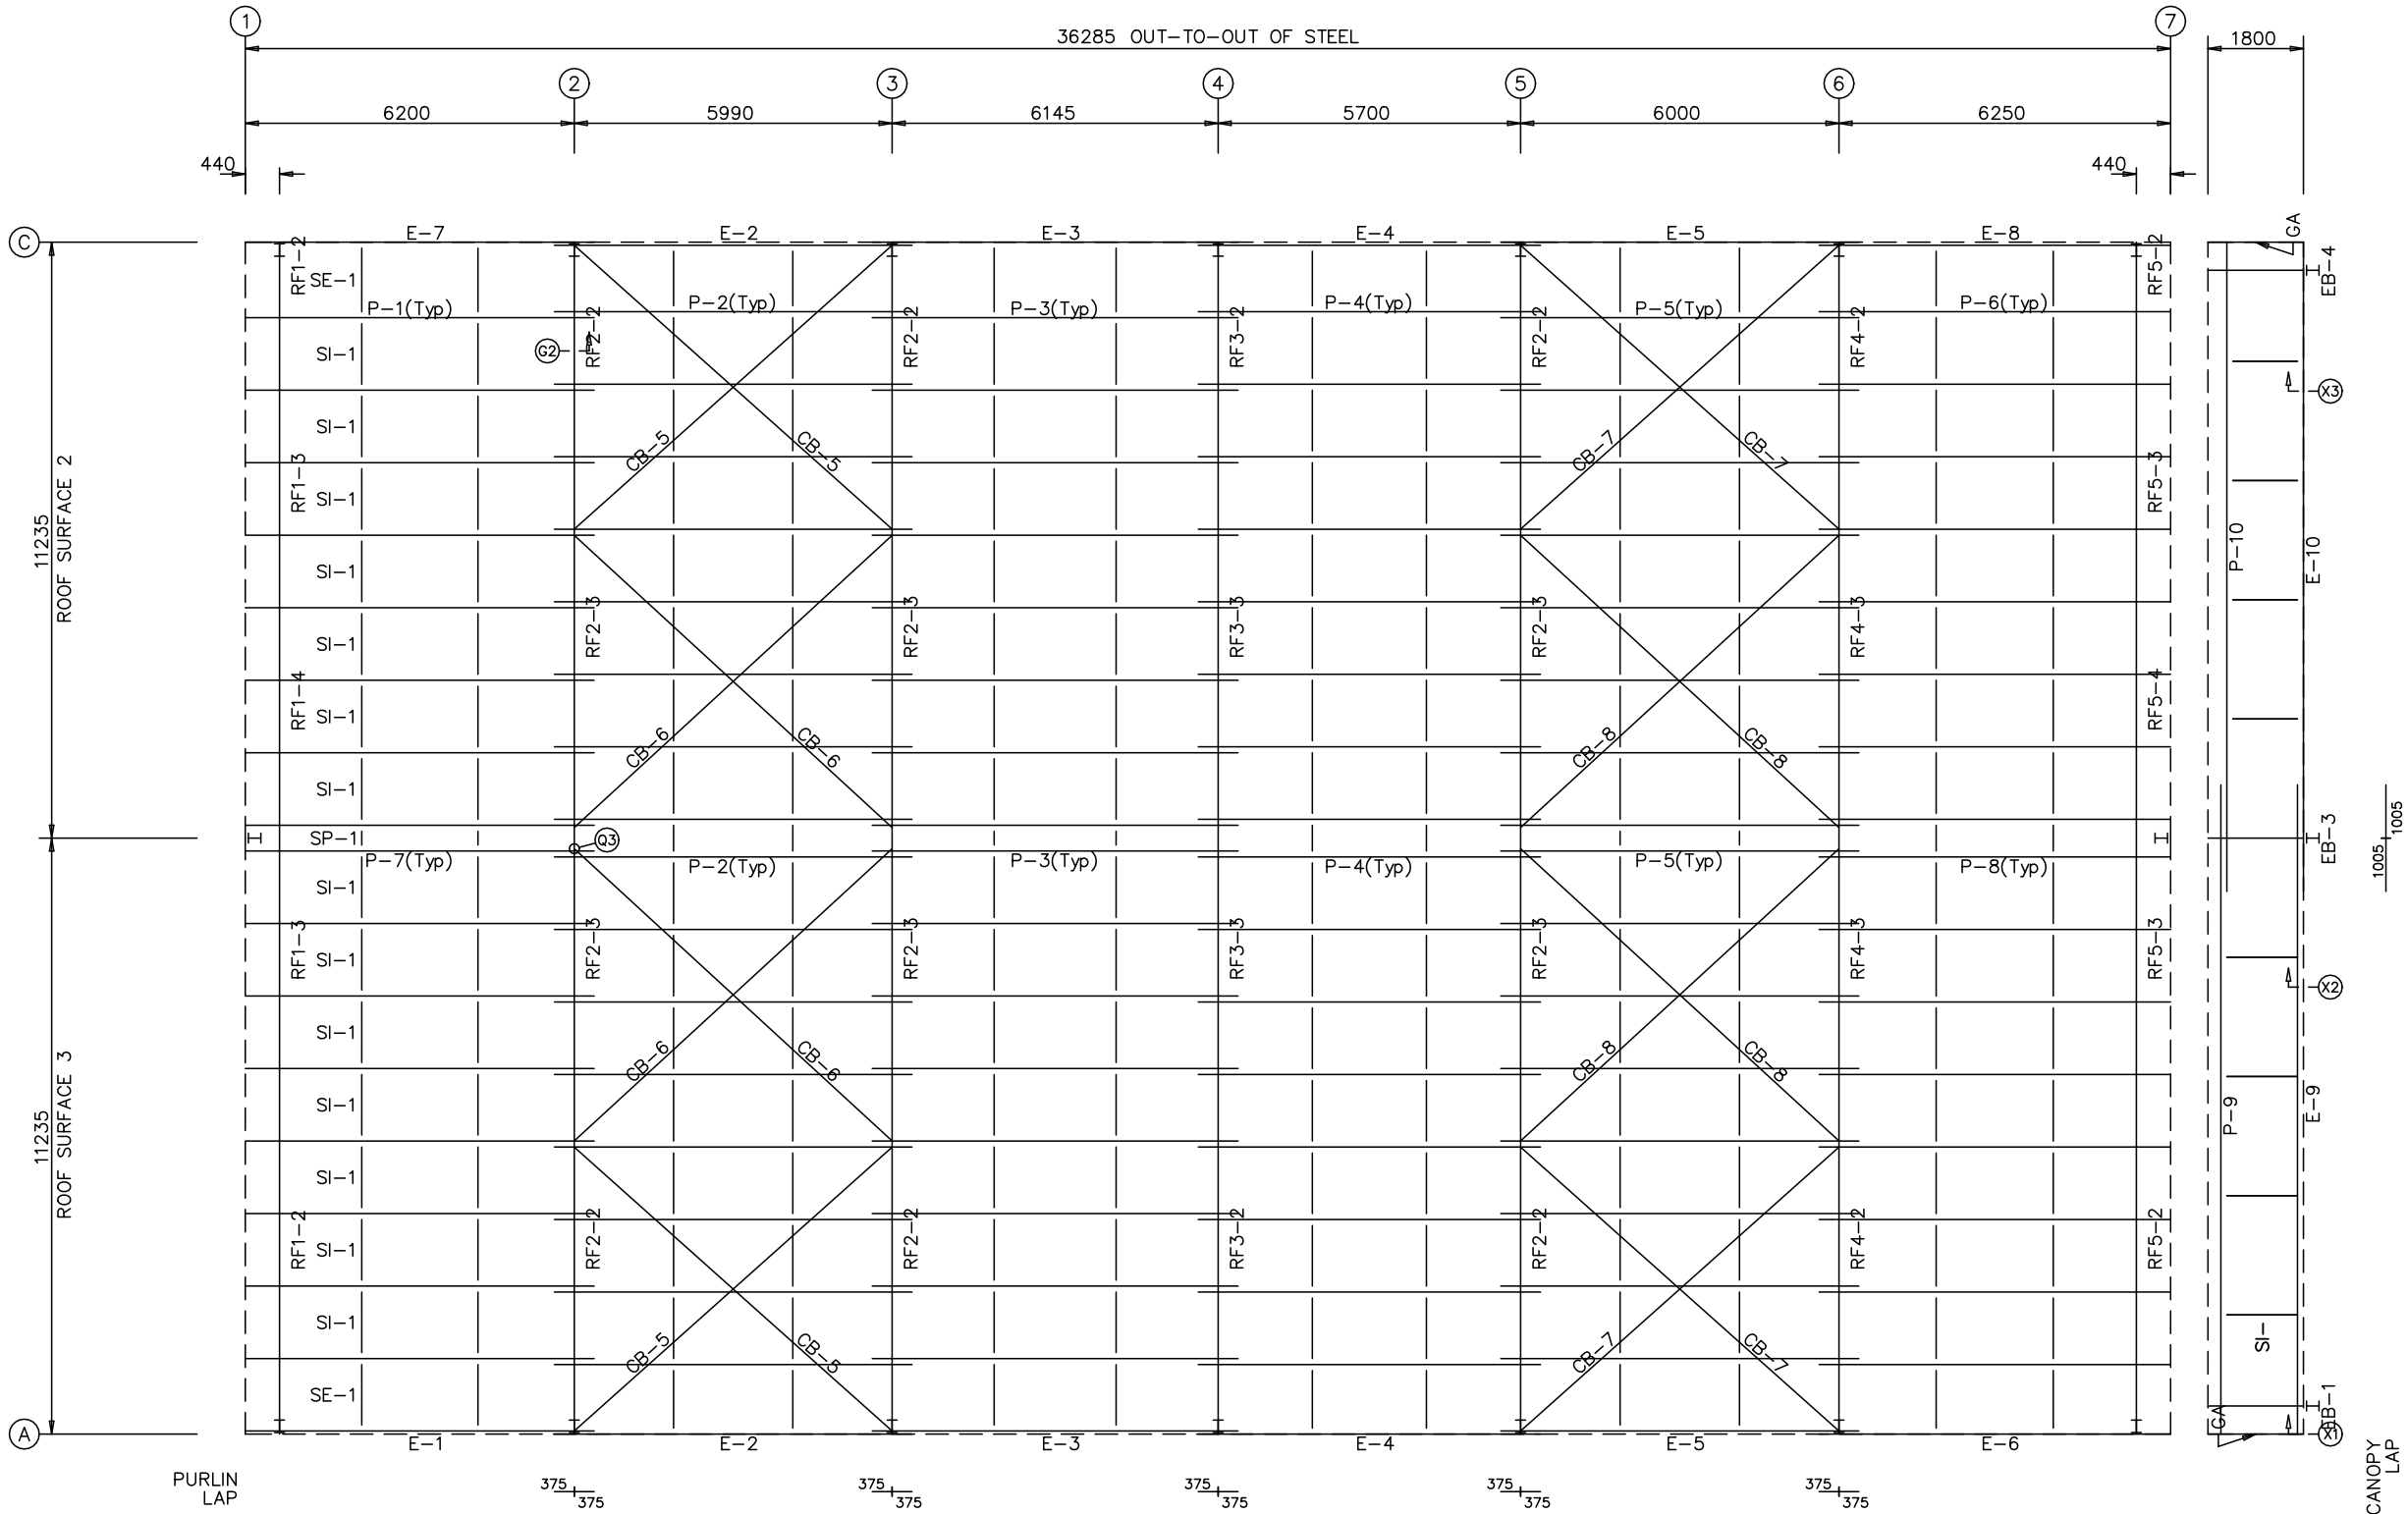

COLUMNS & RAFTERS MARKING PLAN

| INFINITI SOLUTION |                    |                            |        |        |
|-------------------|--------------------|----------------------------|--------|--------|
| PROJECT           | Proposed Warehouse | ROOF FRAMING               |        |        |
| ID                | C323-153-Final     | DESIGN:                    | DRAFT: | CHECK: |
| PROJECT ADDRESS   | Proposed Warehouse | DATE: 11/AUG/2025 SHEET OF |        |        |

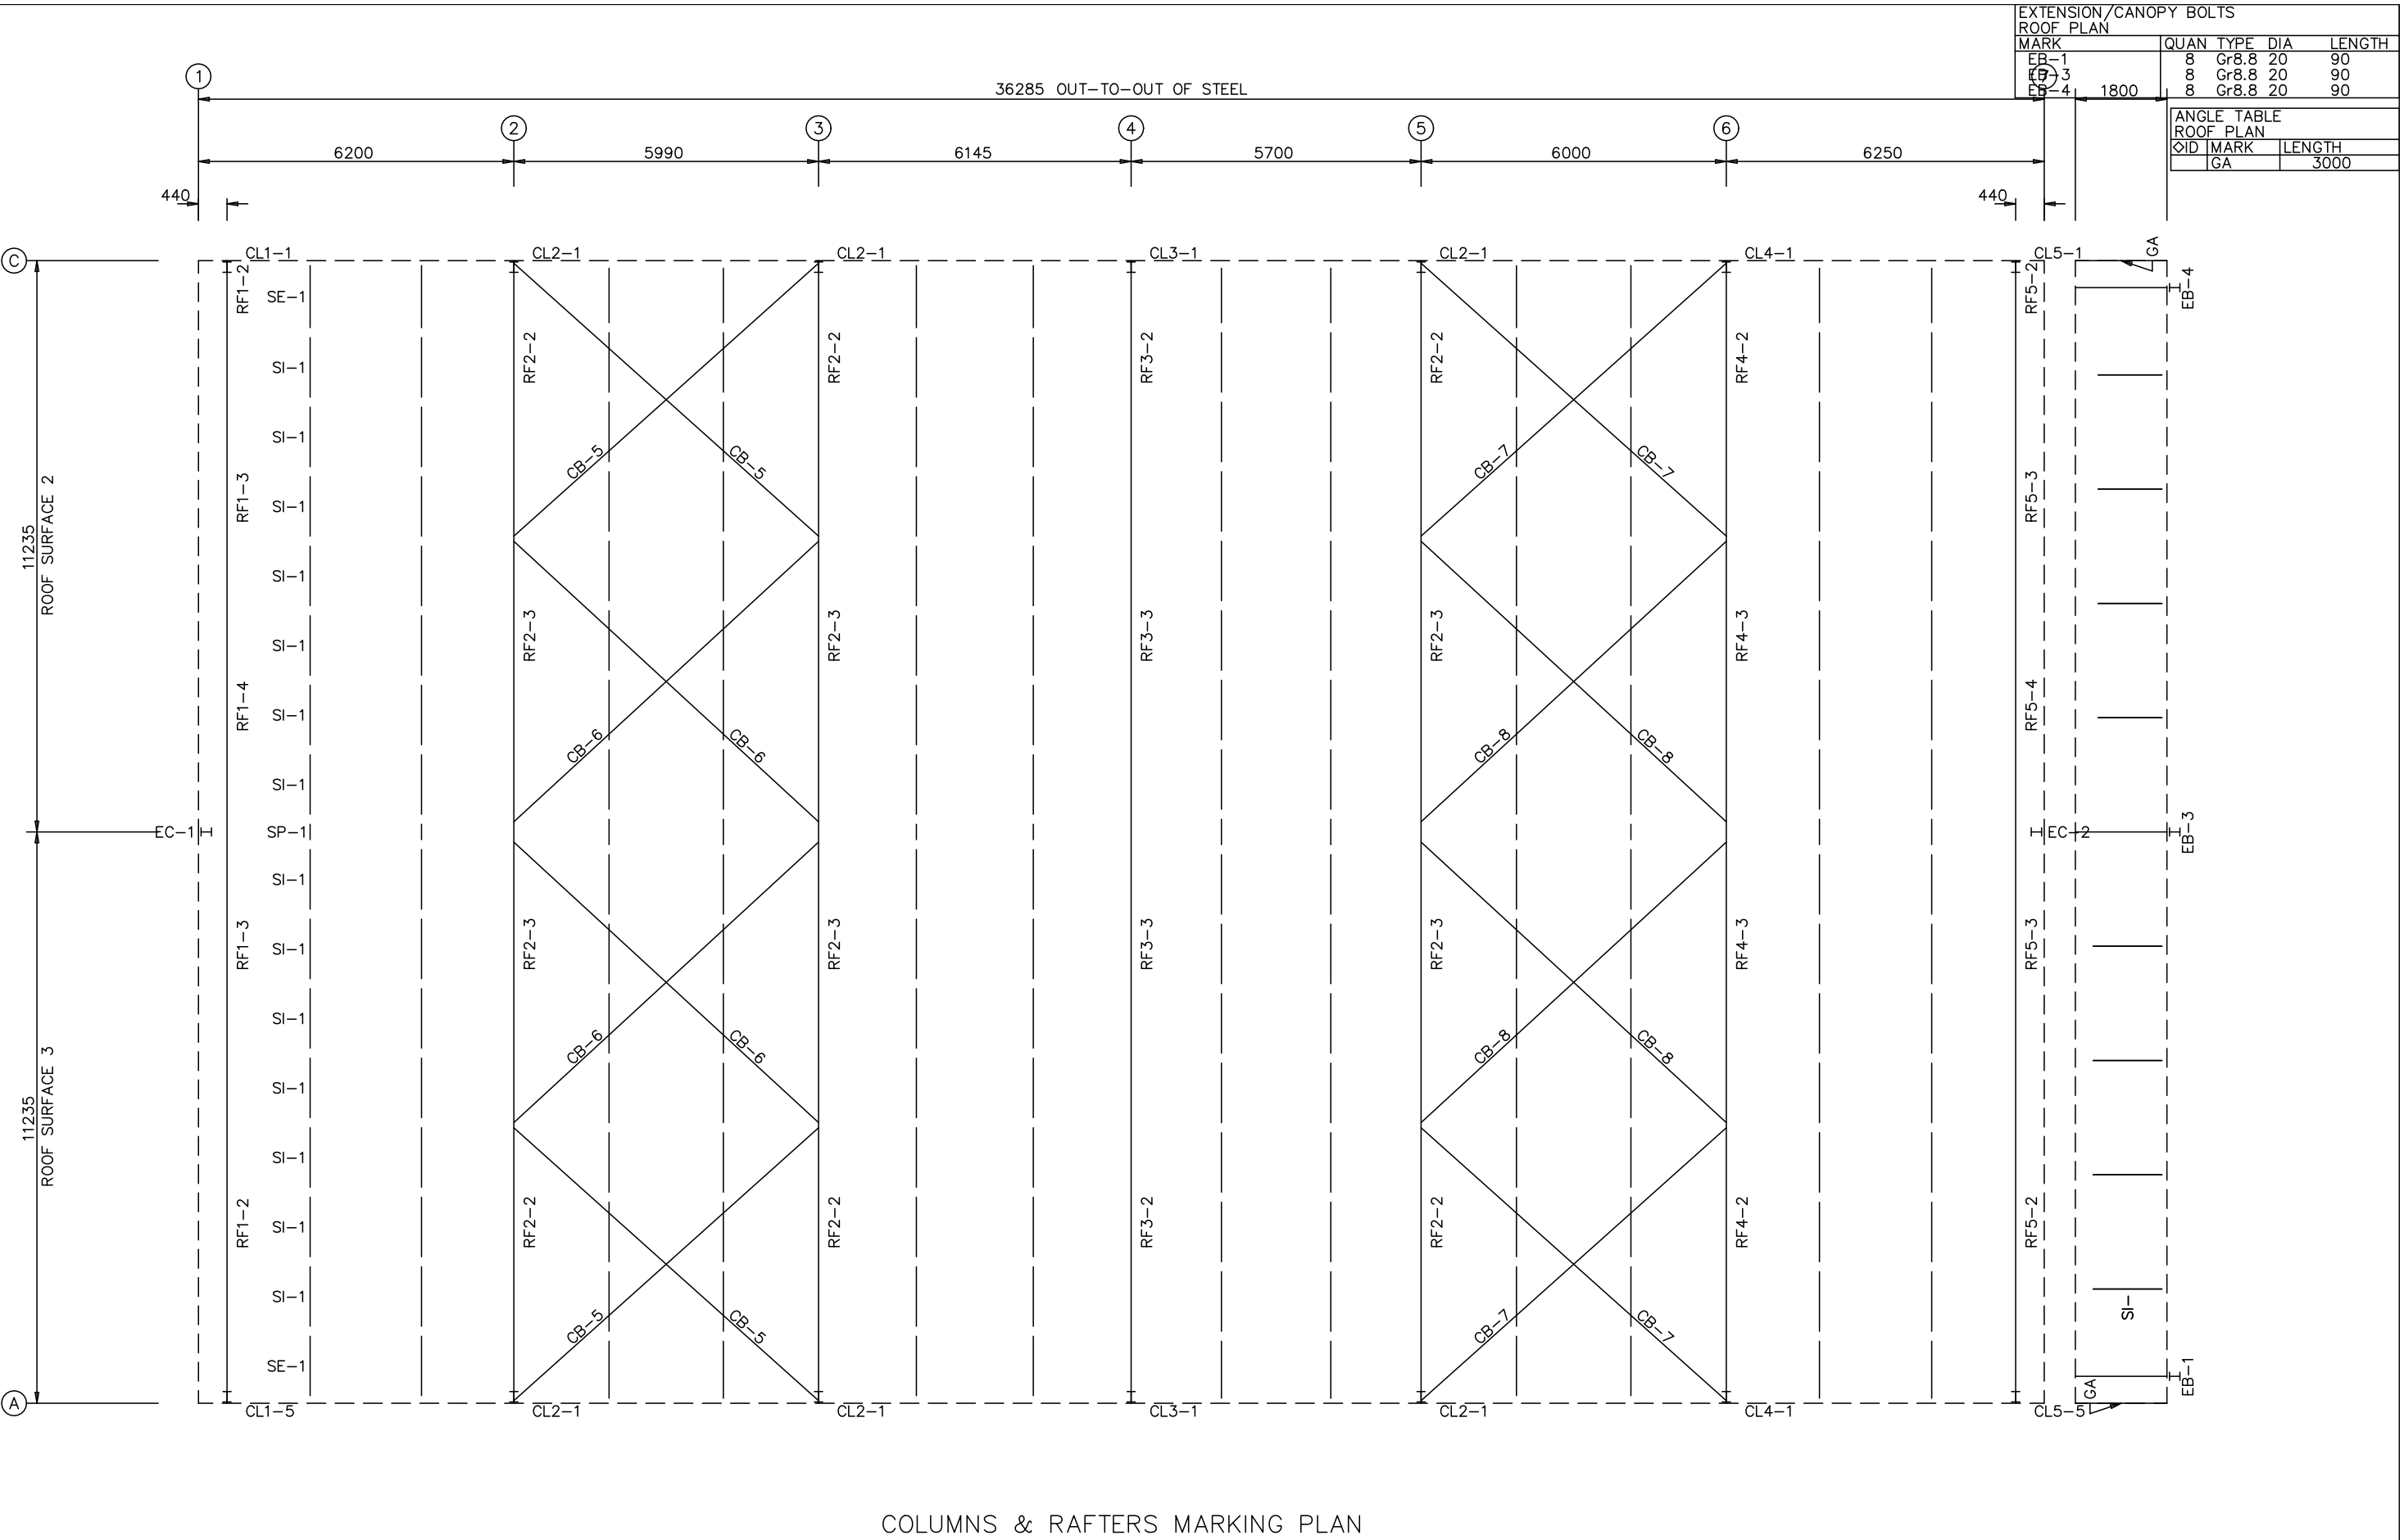

COLUMNS & RAFTERS MARKING PLAN


|                   |                    |  |                            |               |
|-------------------|--------------------|--|----------------------------|---------------|
| INFINITI SOLUTION |                    |  |                            |               |
| PROJECT           | Proposed Warehouse |  | ROOF FRAMING               |               |
| ID                | C323-153-Final     |  | DESIGN:                    | DRAFT: CHECK: |
| PROJECT ADDRESS   | Proposed Warehouse |  | DATE: 11/AUG/2025 SHEET OF |               |

| BOLT TABLE   |  |      |       |                 |
|--------------|--|------|-------|-----------------|
| FRAME LINE 1 |  |      |       |                 |
| LOCATION     |  | QUAN | TYPE  | DIA      LENGTH |
| Columns/Raf  |  | 4    | Gr8.8 | 20      90      |

| MEMBER TABLE |         |        |
|--------------|---------|--------|
| FRAME LINE 1 |         |        |
| MARK         | PART    | LENGTH |
| EC-1         | W40b155 | 8830   |
| G-1          | 200Z15  | 11730  |
| G-2          | 200Z20  | 11730  |
| G-3          | 200Z25  | 11730  |
| G-4          | 200Z25  | 11935  |
| G-5          | 200Z15  | 11730  |
| G-6          | 200Z20  | 11730  |
| G-7          | 200Z25  | 11730  |
| G-8          | 200Z25  | 11935  |
| JB-1         | SROD12  | 1100   |
| JB-2         | SROD12  | 1300   |
| JB-3         | SROD12  | 1600   |
| JB-4         | SROD12  | 900    |

| FLANGE BRACE TABLE |       |        |
|--------------------|-------|--------|
| FRAME LINE 1       |       |        |
| VID                | MARK  | LENGTH |
| 1                  | FB568 | 568    |

| CONNECTION PLATES |           |
|-------------------|-----------|
| FRAME LINE 1      |           |
| ID                | MARK/PART |
| 1                 | d1        |

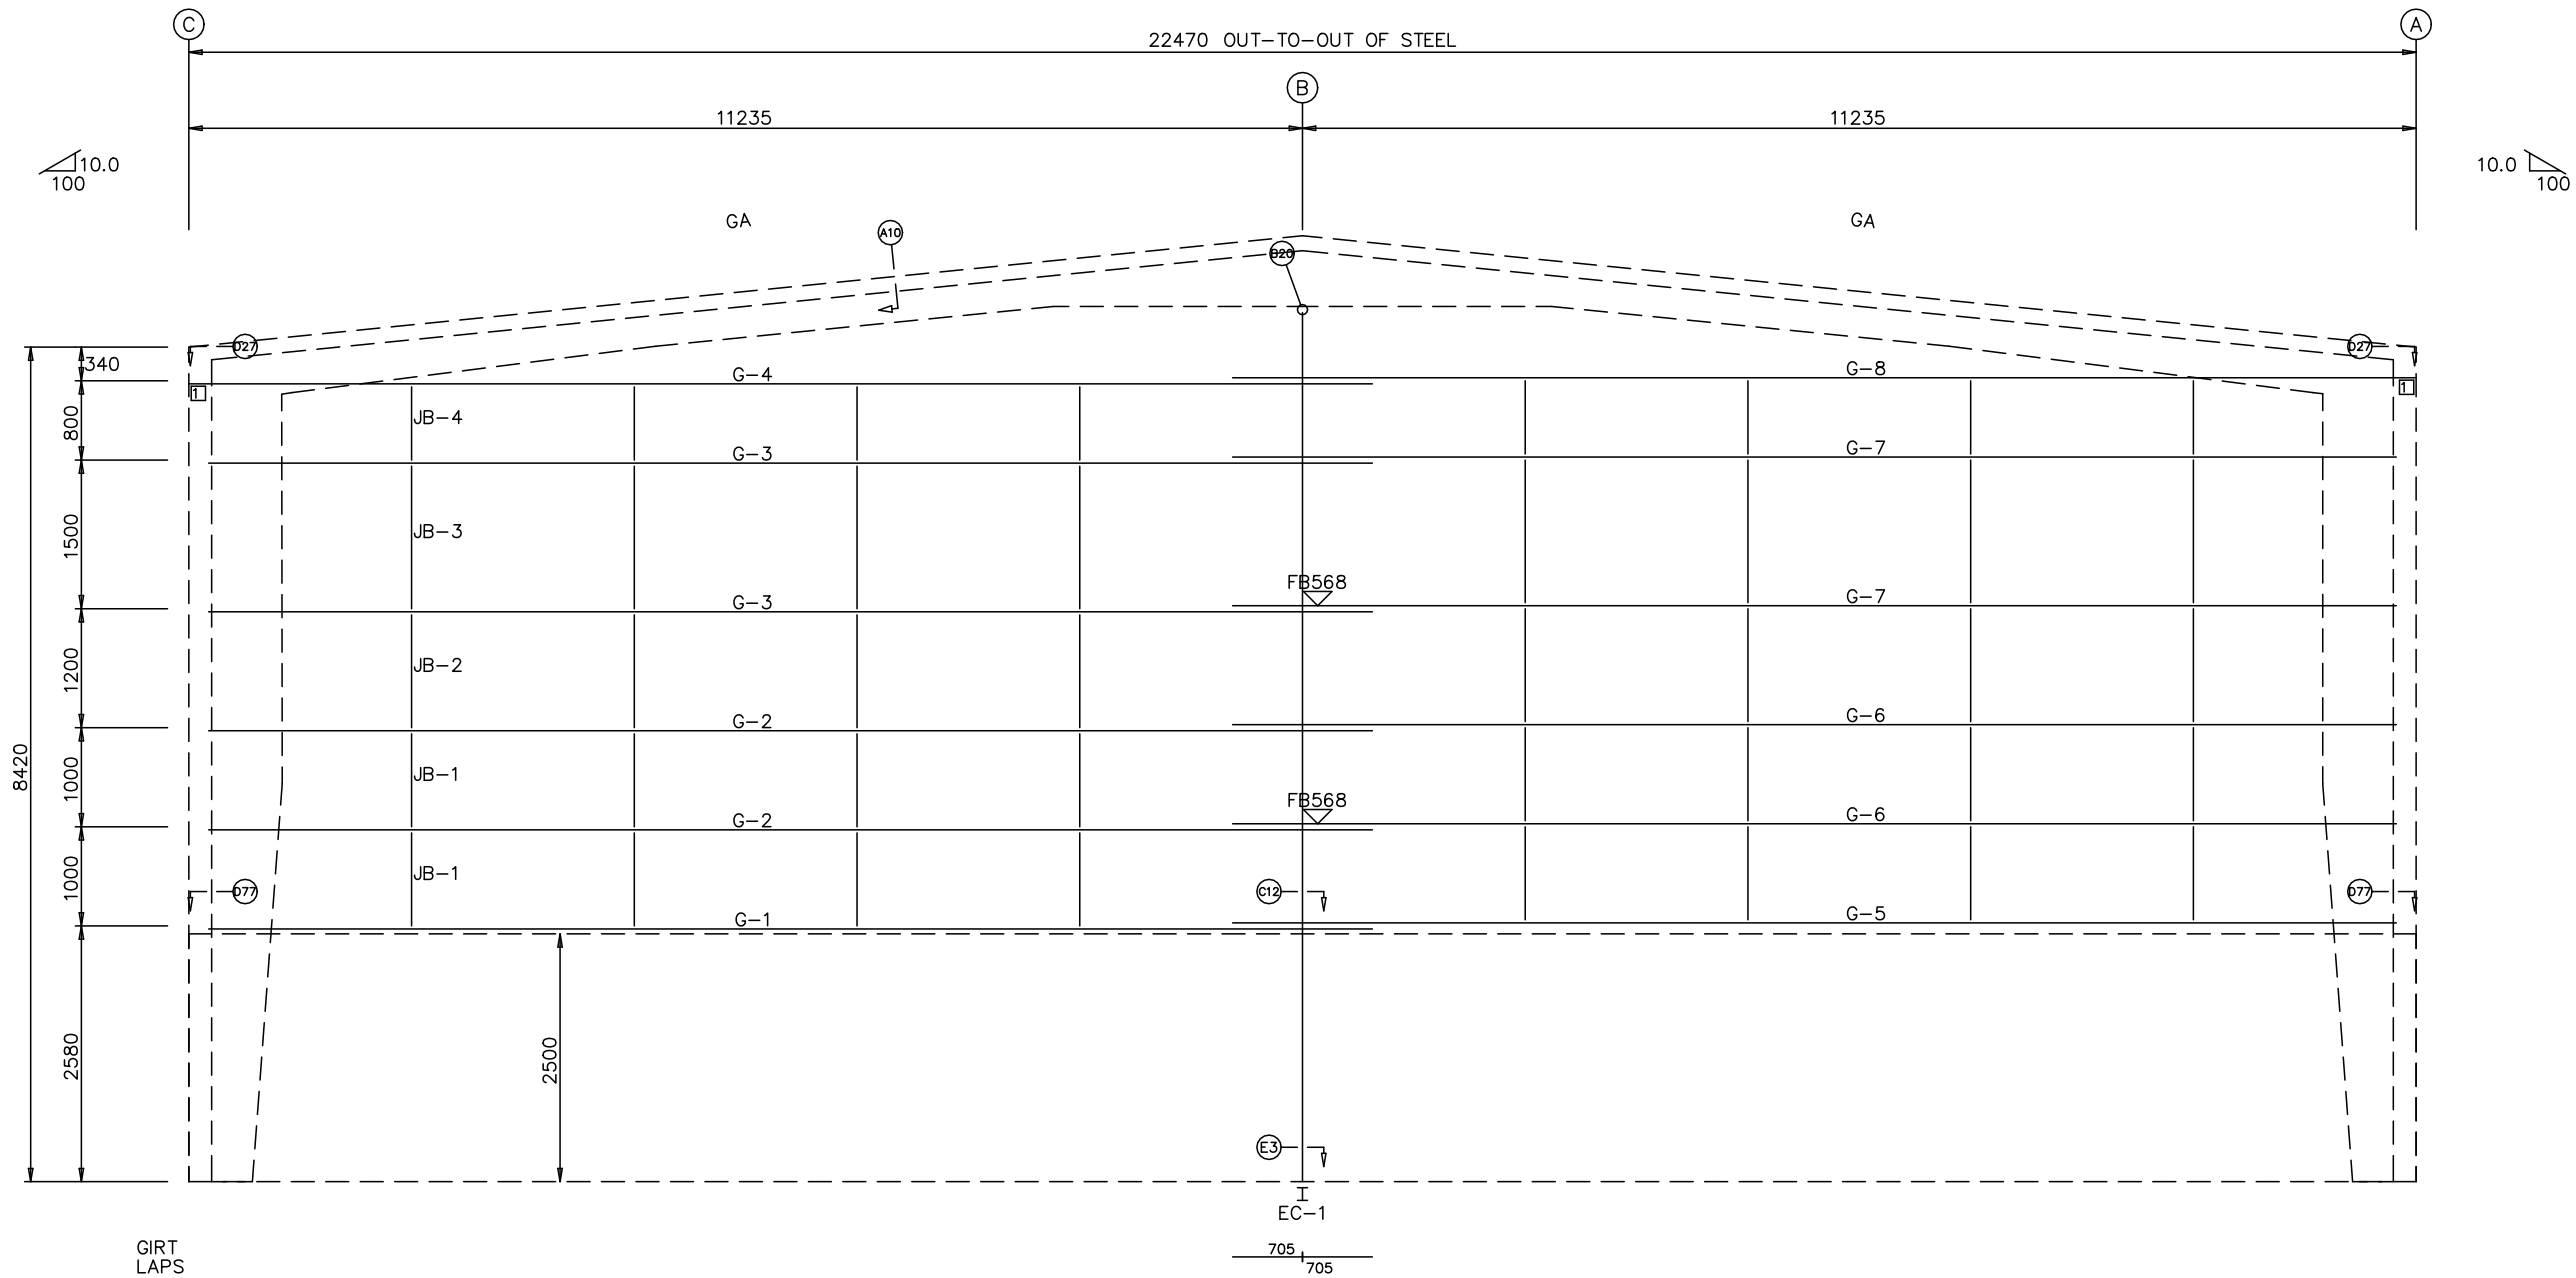

ENDWALL FRAMING: FRAME LINE 1


| INFINITI SOLUTION |                    |                                 |        |        |
|-------------------|--------------------|---------------------------------|--------|--------|
| PROJECT           | Proposed Warehouse | ENDWALL FRAMING                 |        |        |
| ID                | C323-153-Final     | DESIGN:                         | DRAFT: | CHECK: |
| PROJECT ADDRESS   | Proposed Warehouse | DATE: 11/AUG/2025 SHEET      OF |        |        |

| BOLT TABLE   |      |       |     |        |
|--------------|------|-------|-----|--------|
| FRAME LINE 7 |      |       |     |        |
| LOCATION     | QUAN | TYPE  | DIA | LENGTH |
| Columns/Raf  | 4    | Gr8.8 | 20  | 90     |

| MEMBER TABLE |         |        |
|--------------|---------|--------|
| FRAME LINE 7 |         |        |
| MARK         | PART    | LENGTH |
| EC-2         | W40b155 | 8830   |
| DJ-1         | 200C20  | 4480   |
| G-3          | 200Z25  | 11730  |
| G-4          | 200Z25  | 11935  |
| G-5          | 200Z15  | 11730  |
| G-7          | 200Z25  | 11730  |
| G-8          | 200Z25  | 11935  |
| G-9          | 200Z15  | 3066   |
| G-10         | 200Z25  | 11730  |
| G-11         | 200Z15  | 3980   |
| G-12         | 200Z18  | 3980   |
| G-13         | 200Z18  | 11730  |
| G-6          | 200Z20  | 11730  |
| JB-1         | SR0D12  | 1100   |
| JB-2         | SR0D12  | 1300   |
| JB-3         | SR0D12  | 1600   |
| JB-4         | SR0D12  | 900    |

| FLANGE BRACE TABLE |       |        |
|--------------------|-------|--------|
| FRAME LINE 7       |       |        |
| VID                | MARK  | LENGTH |
| 1                  | FB568 | 568    |

| CONNECTION PLATES |           |
|-------------------|-----------|
| FRAME LINE 7      |           |
| ID                | MARK/PART |
| 1                 | d1        |
| 2                 | f1        |
| 3                 | j1        |
| 4                 | b1        |

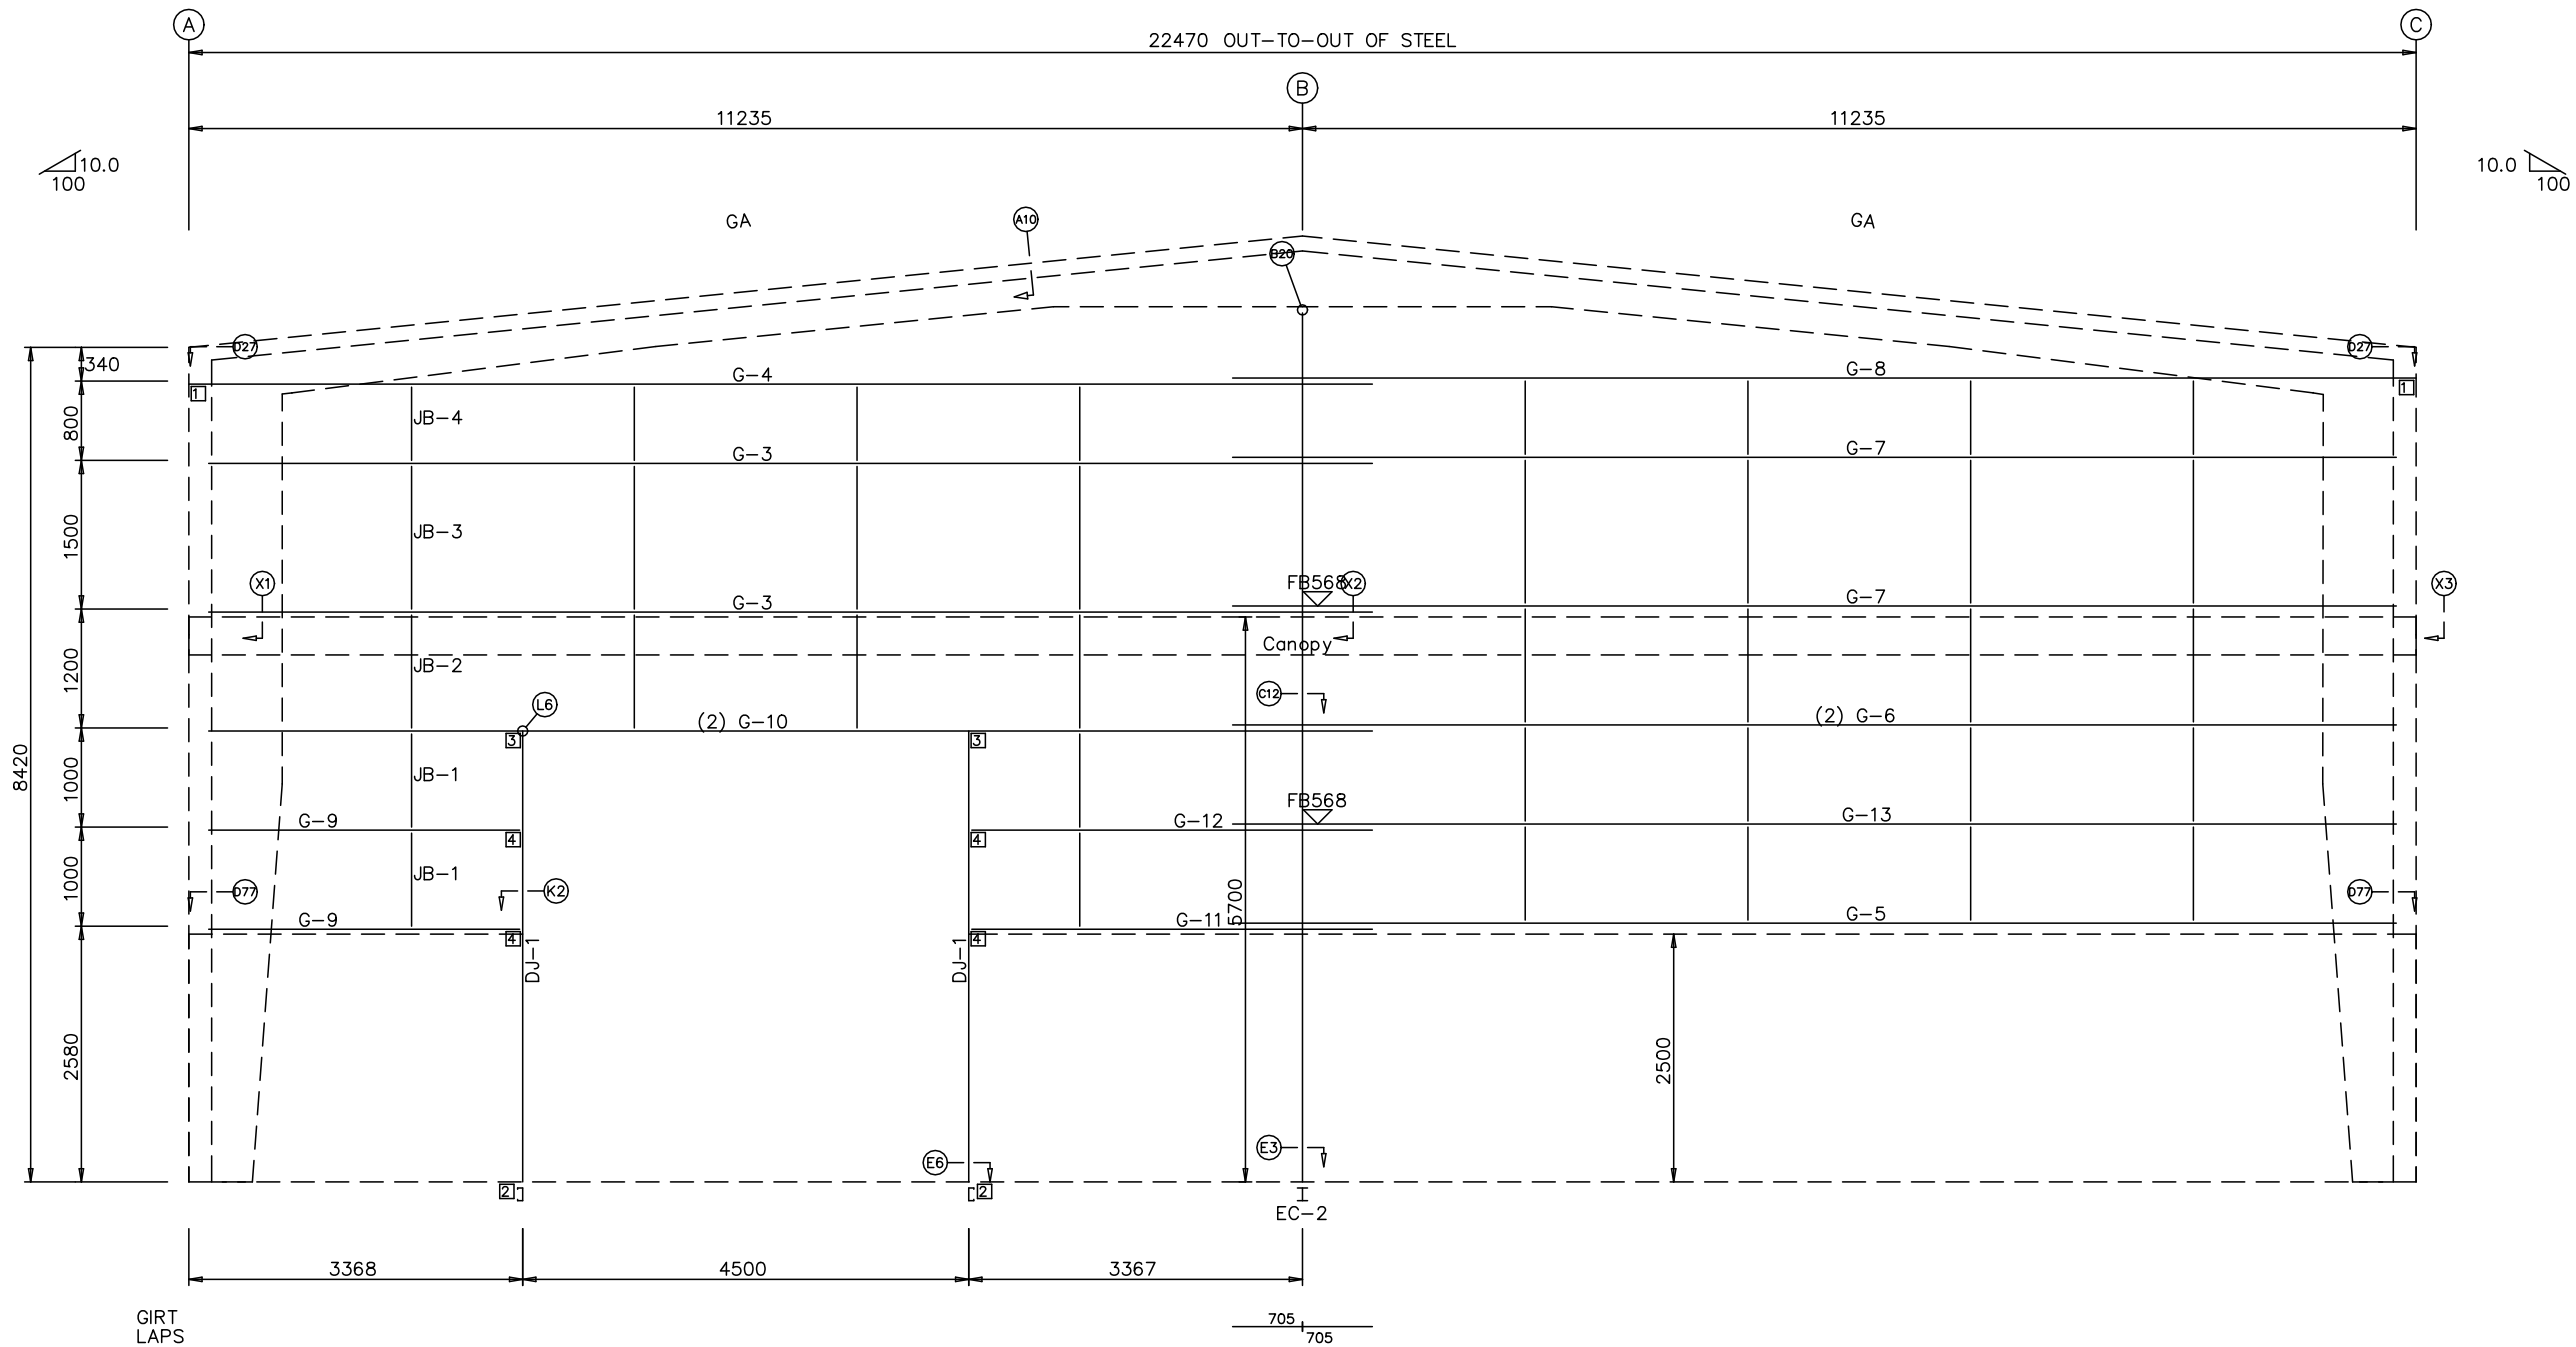


ENDWALL FRAMING: FRAME LINE 7

| INFINITI SOLUTION |                    |                            |        |        |
|-------------------|--------------------|----------------------------|--------|--------|
| PROJECT           | Proposed Warehouse | ENDWALL FRAMING            |        |        |
| ID                | C323-153-Final     | DESIGN:                    | DRAFT: | CHECK: |
| PROJECT ADDRESS   | Proposed Warehouse | DATE: 11/AUG/2025 SHEET OF |        |        |

| BOLT TABLE<br>FRAME LINE C |      |       |     |        |
|----------------------------|------|-------|-----|--------|
| LOCATION                   | QUAN | TYPE  | DIA | LENGTH |
| Strut                      | 2    | Gr8.8 | 16  | 70     |
| EB-2 (L)                   | 8    | Gr8.8 | 20  | 90     |
| EB-2 (R)                   | 4    | Gr8.8 | 16  |        |

| SPECIAL BOLTS |      |       |     |        |      |
|---------------|------|-------|-----|--------|------|
| Ø ID          | QUAN | TYPE  | DIA | LENGTH | WASH |
| 3             | 2    | Gr8.8 | 16  | 70     | 2    |

| MEMBER TABLE<br>FRAME LINE C |         |        |
|------------------------------|---------|--------|
| MARK                         | PART    | LENGTH |
| EB-2                         | W30x155 | 5805   |
| EB-4                         | BEAM    | 2272   |
| G-15                         | 200Z15  | 6740   |
| G-16                         | 200Z15  | 6895   |
| G-17                         | 200Z15  | 6450   |
| G-18                         | 200Z15  | 6750   |
| G-20                         | 200Z15  | 6620   |
| G-21                         | 200Z15  | 6570   |
| ST-1                         | T80x32  | 5945   |
| ST-2                         | T80x32  | 5955   |
| CB-1                         | ROD20   | 8630   |
| CB-2                         | ROD20   | 6120   |
| CB-3                         | ROD20   | 8640   |
| CB-4                         | ROD20   | 6130   |
| JB-1                         | SROD12  | 1100   |
| JB-2                         | SROD12  | 1300   |
| JB-3                         | SROD12  | 1600   |
| JB-5                         | SROD12  | 1090   |

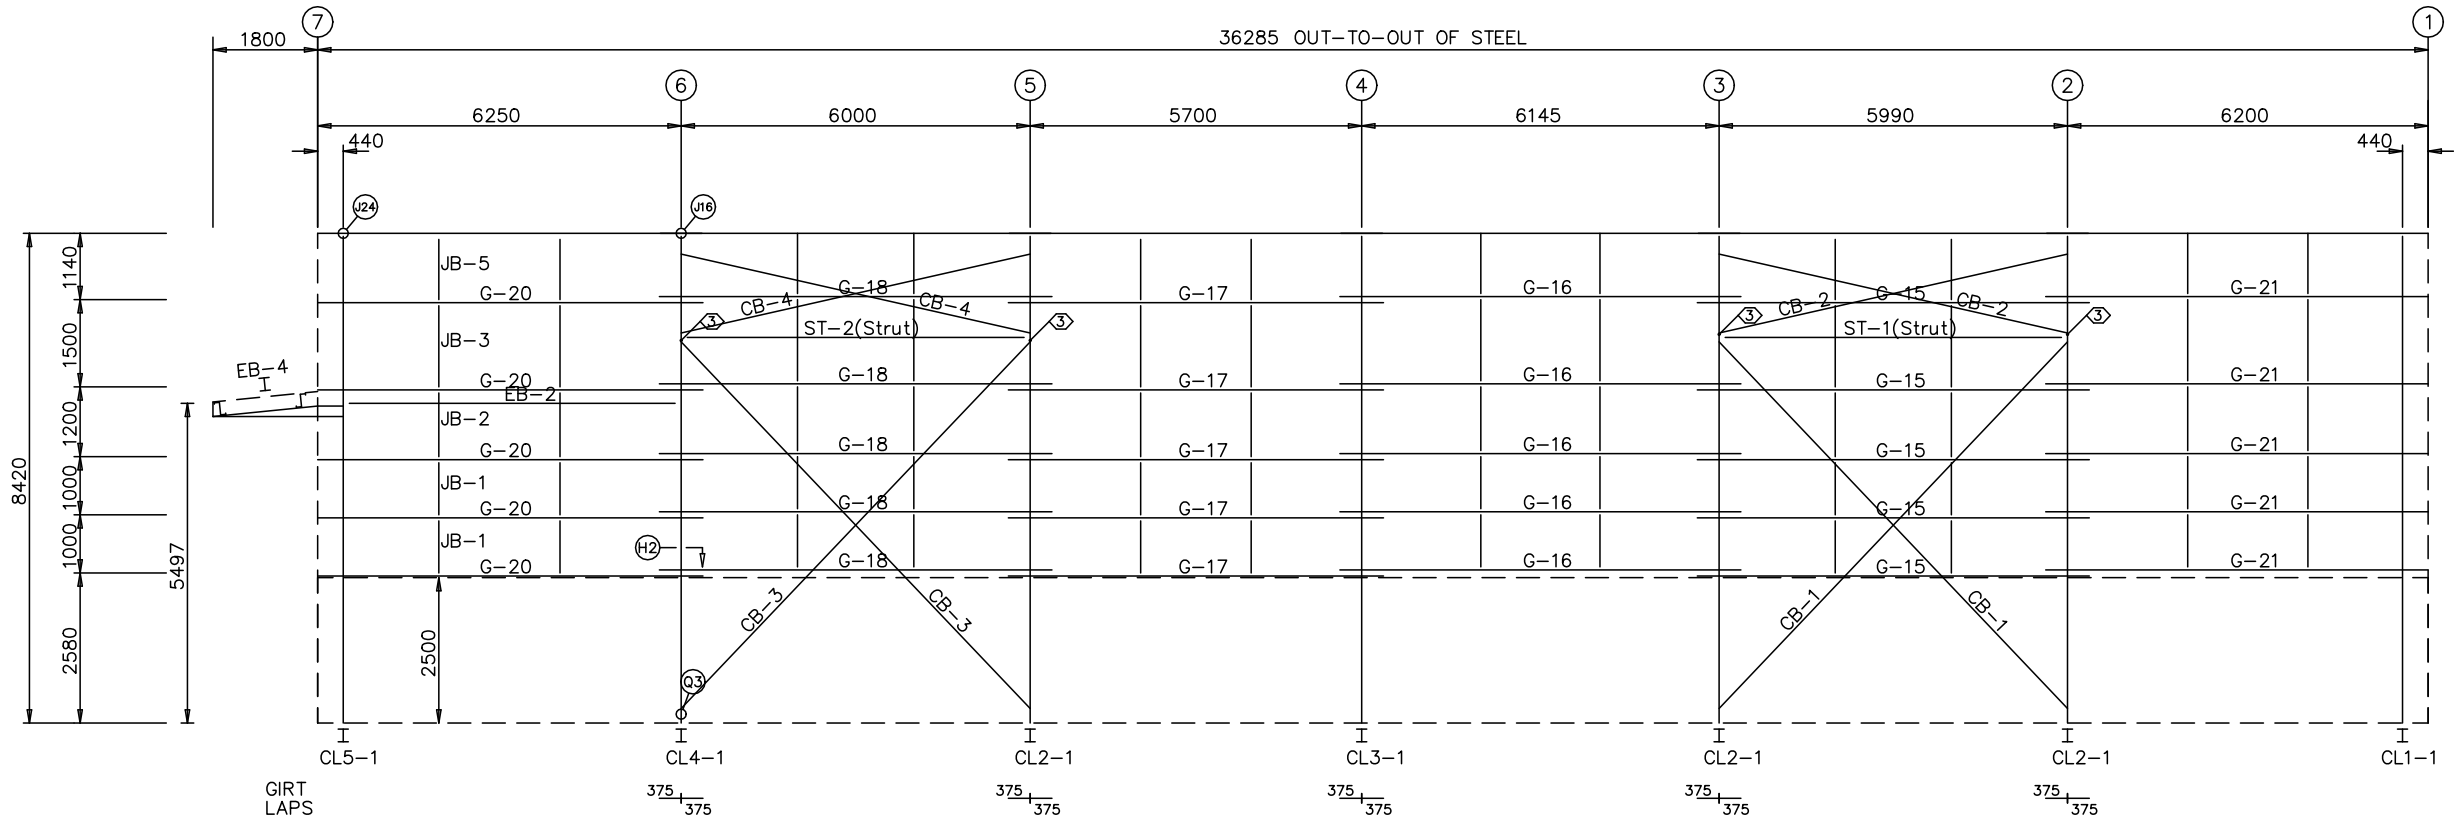

SIDEWALL FRAMING: FRAME LINE C


| INFINITI SOLUTION |                    |                            |        |        |
|-------------------|--------------------|----------------------------|--------|--------|
| PROJECT           | Proposed Warehouse | SIDEWALL FRAMING           |        |        |
| ID                | C323-153-Final     | DESIGN:                    | DRAFT: | CHECK: |
| PROJECT ADDRESS   | Proposed Warehouse | DATE: 11/AUG/2025 SHEET OF |        |        |



| BOLT TABLE   |      |       |     |        |
|--------------|------|-------|-----|--------|
| FRAME LINE A |      |       |     |        |
| LOCATION     | QUAN | TYPE  | DIA | LENGTH |
| Strut        | 2    | Gr8.8 | 16  | 70     |
| EB-2 (L)     | 4    | Gr8.8 | 16  |        |
| EB-2 (R)     | 8    | Gr8.8 | 20  | 90     |

| SPECIAL BOLTS |      |       |     |             |
|---------------|------|-------|-----|-------------|
| Ø ID          | QUAN | TYPE  | DIA | LENGTH WASH |
| 3             | 2    | Gr8.8 | 16  | 70 2        |

| MEMBER TABLE |         |        |
|--------------|---------|--------|
| FRAME LINE A |         |        |
| MARK         | PART    | LENGTH |
| EB-1         | BEAM    | 2272   |
| EB-2         | W30a155 | 5805   |
| G-14         | 200Z15  | 6570   |
| G-15         | 200Z15  | 6740   |
| G-16         | 200Z15  | 6895   |
| G-17         | 200Z15  | 6450   |
| G-18         | 200Z15  | 6750   |
| G-19         | 200Z15  | 6620   |
| ST-1         | T80x32  | 5945   |
| ST-2         | T80x32  | 5955   |
| CB-1         | ROD20   | 8630   |
| CB-2         | ROD20   | 6120   |
| CB-3         | ROD20   | 8640   |
| CB-4         | ROD20   | 6130   |
| JB-1         | SROD12  | 1100   |
| JB-2         | SROD12  | 1300   |
| JB-3         | SROD12  | 1600   |
| JB-5         | SROD12  | 1090   |

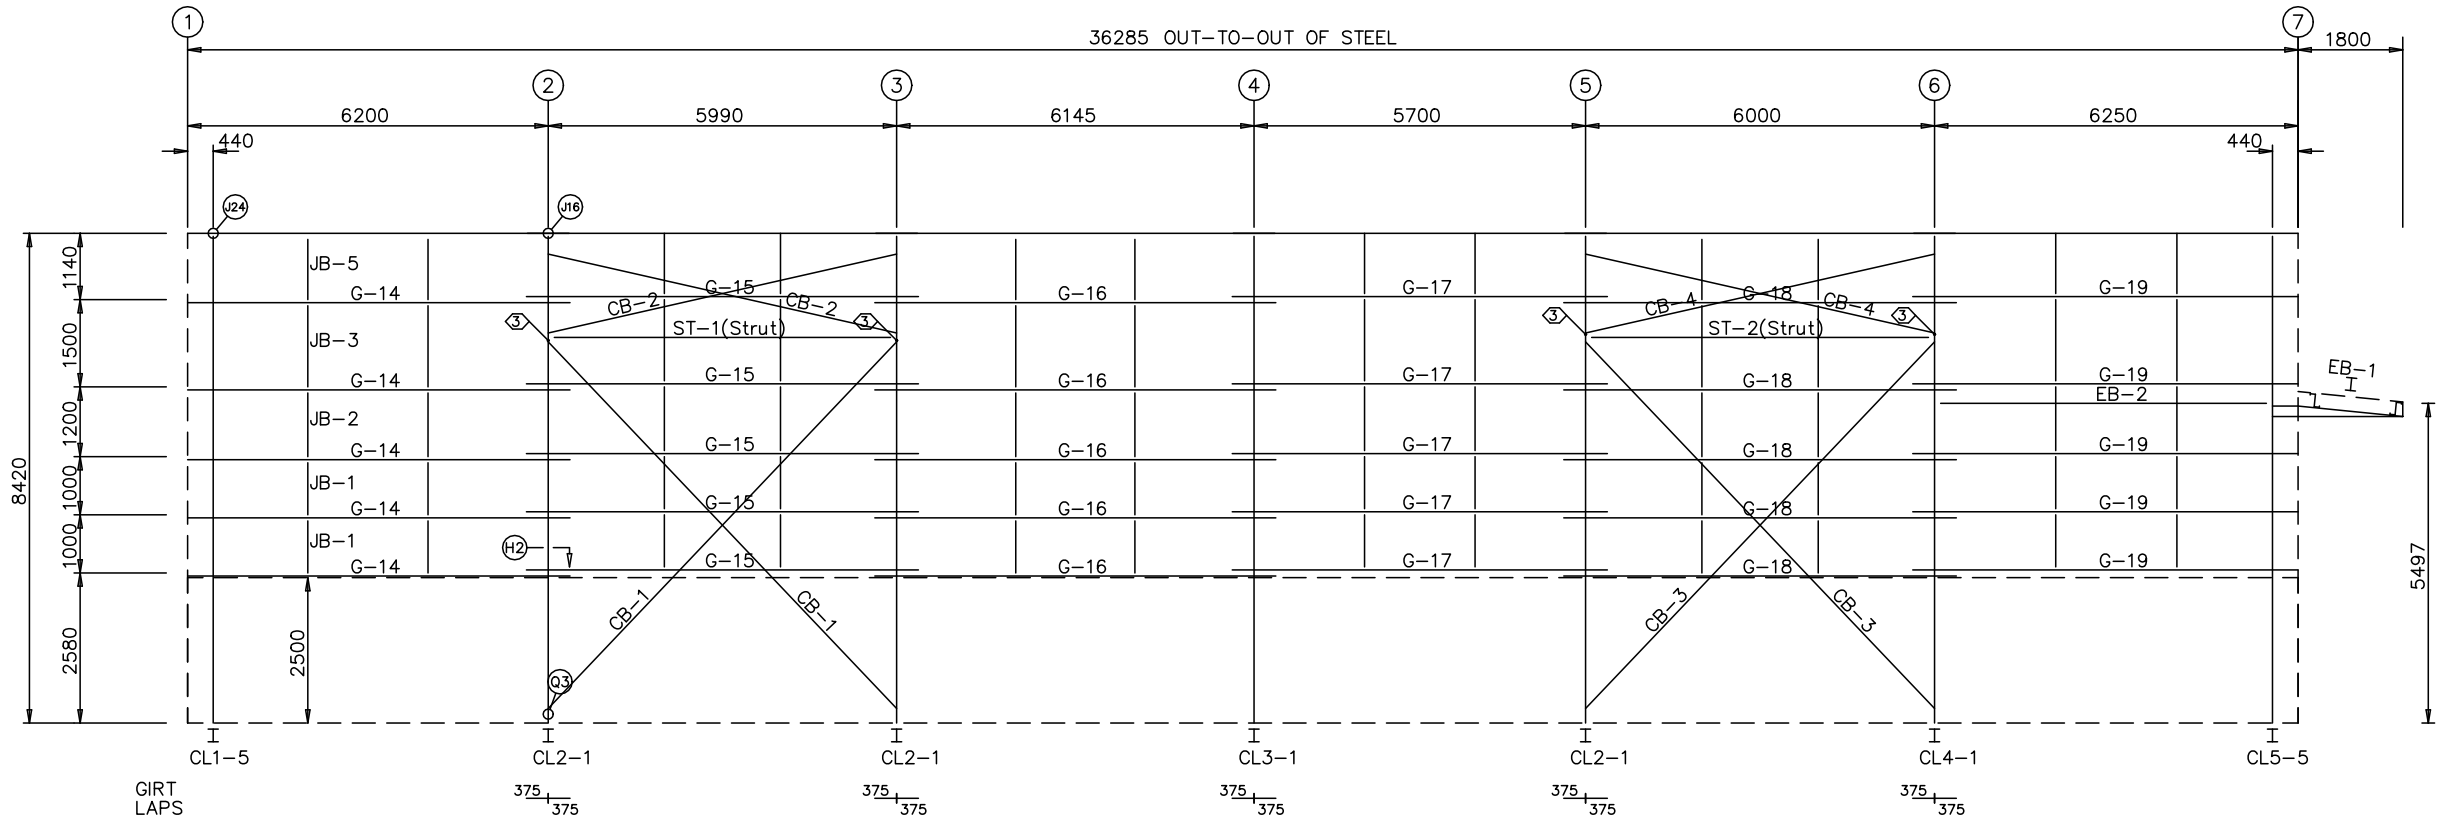

| INFINITI SOLUTION |                    |                   |        |        |
|-------------------|--------------------|-------------------|--------|--------|
| PROJECT           | Proposed Warehouse | SIDEWALL FRAMING  |        |        |
| ID                | C323-153-Final     | DESIGN:           | DRAFT: | CHECK: |
| PROJECT ADDRESS   | Proposed Warehouse | DATE: 11/AUG/2025 | SHEET  | OF     |