


BOLT TABLE				
FRAME LINE 1				
LOCATION	QUAN	TYPE	DIA	LENGTH
Columns/Raf	4	Gr8.8	20	90

MEMBER TABLE		
FRAME LINE 1		
MARK	PART	LENGTH
EC-1	W40b155	8830
G-1	200Z15	11730
G-2	200Z20	11730
G-3	200Z25	11730
G-4	200Z25	11935
G-5	200Z15	11730
G-6	200Z20	11730
G-7	200Z25	11730
G-8	200Z25	11935
JB-1	SROD12	1100
JB-2	SROD12	1300
JB-3	SROD12	1600
JB-4	SROD12	900

FLANGE BRACE TABLE		
FRAME LINE 1		
VID	MARK	LENGTH
1	FB568	568

CONNECTION PLATES	
FRAME LINE 1	
ID	MARK/PART
1	d1

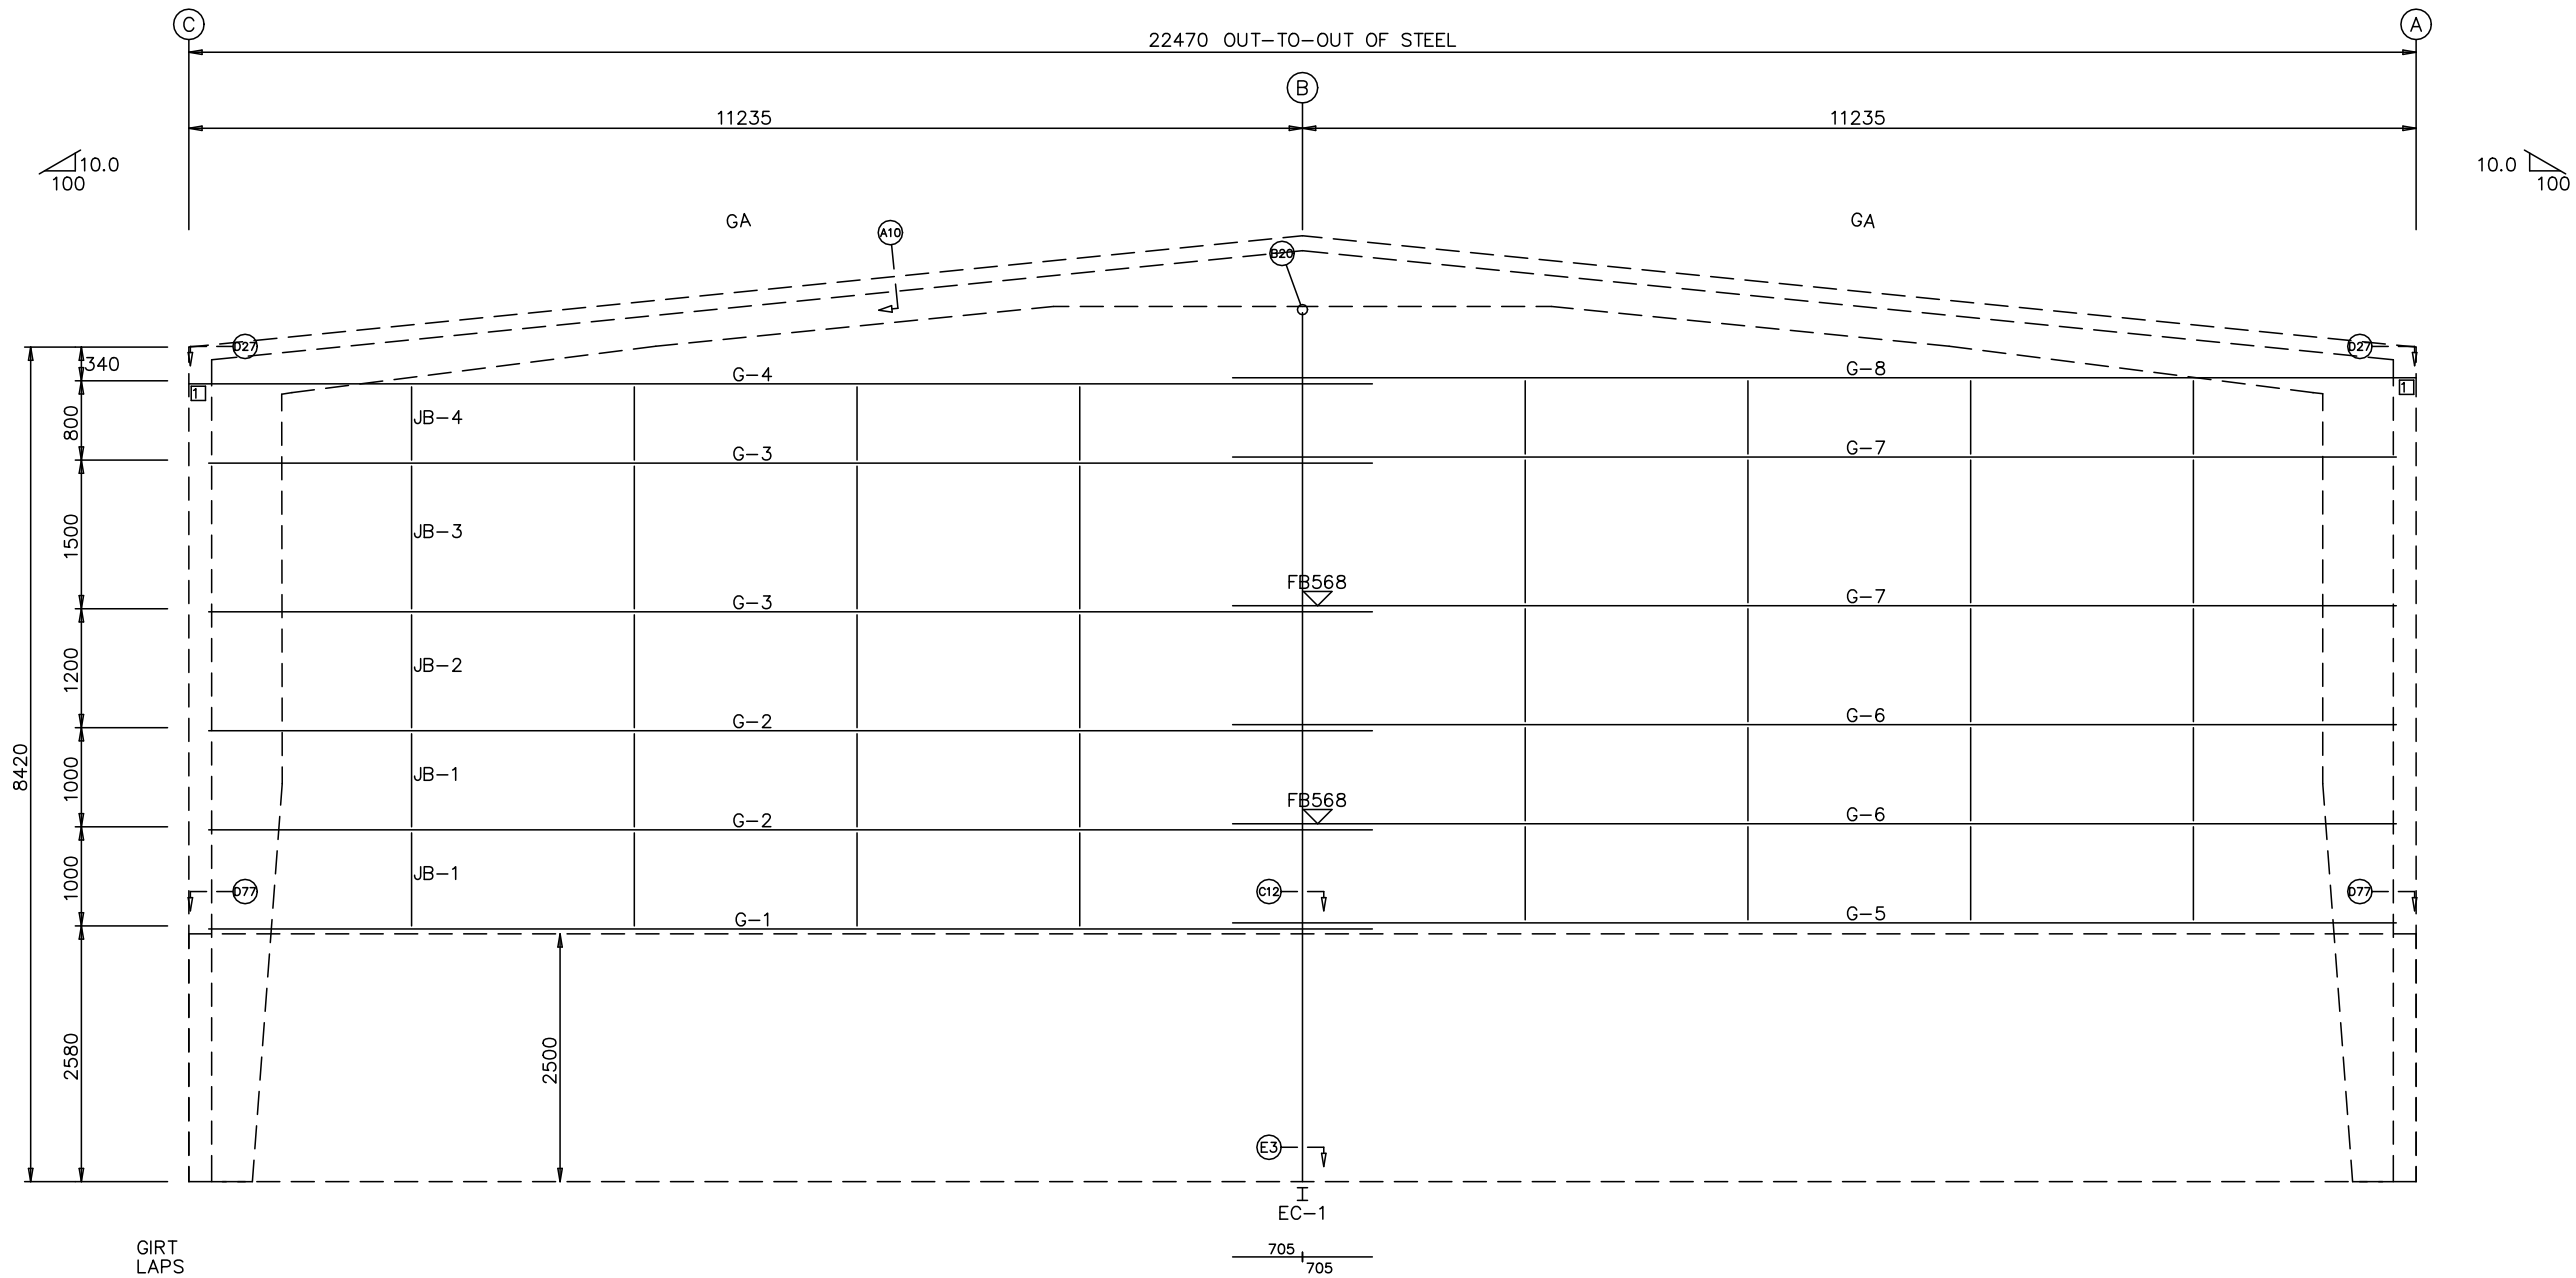

ENDWALL FRAMING: FRAME LINE 1

INFINITI SOLUTION				
PROJECT	Proposed Warehouse	ENDWALL FRAMING		
ID	C323-153-Final	DESIGN:	DRAFT:	CHECK:
PROJECT ADDRESS	Proposed Warehouse	DATE: 11/AUG/2025 SHEET OF		