
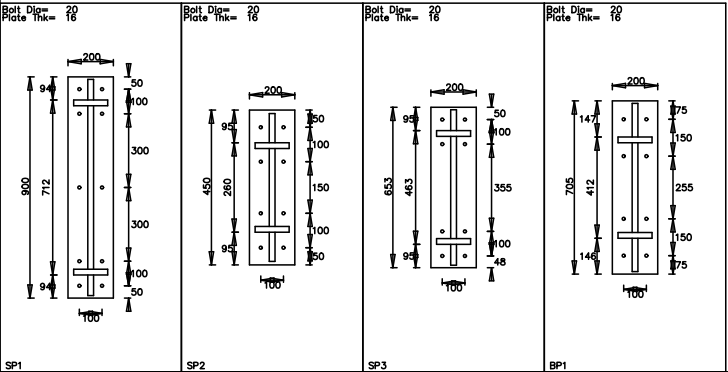


| SPLICE PLATES & BOLTS |         |     |       |     |     |            |       |        |
|-----------------------|---------|-----|-------|-----|-----|------------|-------|--------|
| Splice Mark           | Quan    |     | Bolt  |     |     | Plate Size |       |        |
|                       | Top/Bot | Int | Type  | Dia | Len | Wid        | Thick | Length |
| SP1                   | 4       | 4   | Ør8.8 | 20  | 90  | 200        | 16    | 900    |
| SP2                   | 4       | 4   | Ør8.8 | 20  | 90  | 200        | 16    | 450    |
| SP3                   | 4       | 4   | Ør8.8 | 20  | 90  | 200        | 16    | 653    |

| MEMBER TABLE |           |       |           |  |                                    |
|--------------|-----------|-------|-----------|--|------------------------------------|
| Mark         | Web Depth |       | Web Plate |  | Outside Flange<br>W x Thk x Length |
|              | Start/End | Thick | Length    |  |                                    |
| CL4-1        | 400/ 700  | 5     | 4000      |  | 150 x 6 x 7716                     |
|              | 700/ 700  | 5     | 3716      |  | 150 x 6 x 4011                     |
| RF4-2        | 521/ 601  | 5     | 799       |  | 125 x 6 x 523                      |
|              | 601/ 252  | 4     | 3715      |  | 125 x 6 x 4689                     |
| RF4-3        | 250/ 450  | 4     | 6543      |  | 125 x 5 x 6543                     |
|              |           |       |           |  | 125 x 5 x 6501                     |

▽FLANGE BRACES; FBxx (1 or 2)  
xx=length(mm)  
(1) One Side; (2) Two Sides  
A - L40X40X4

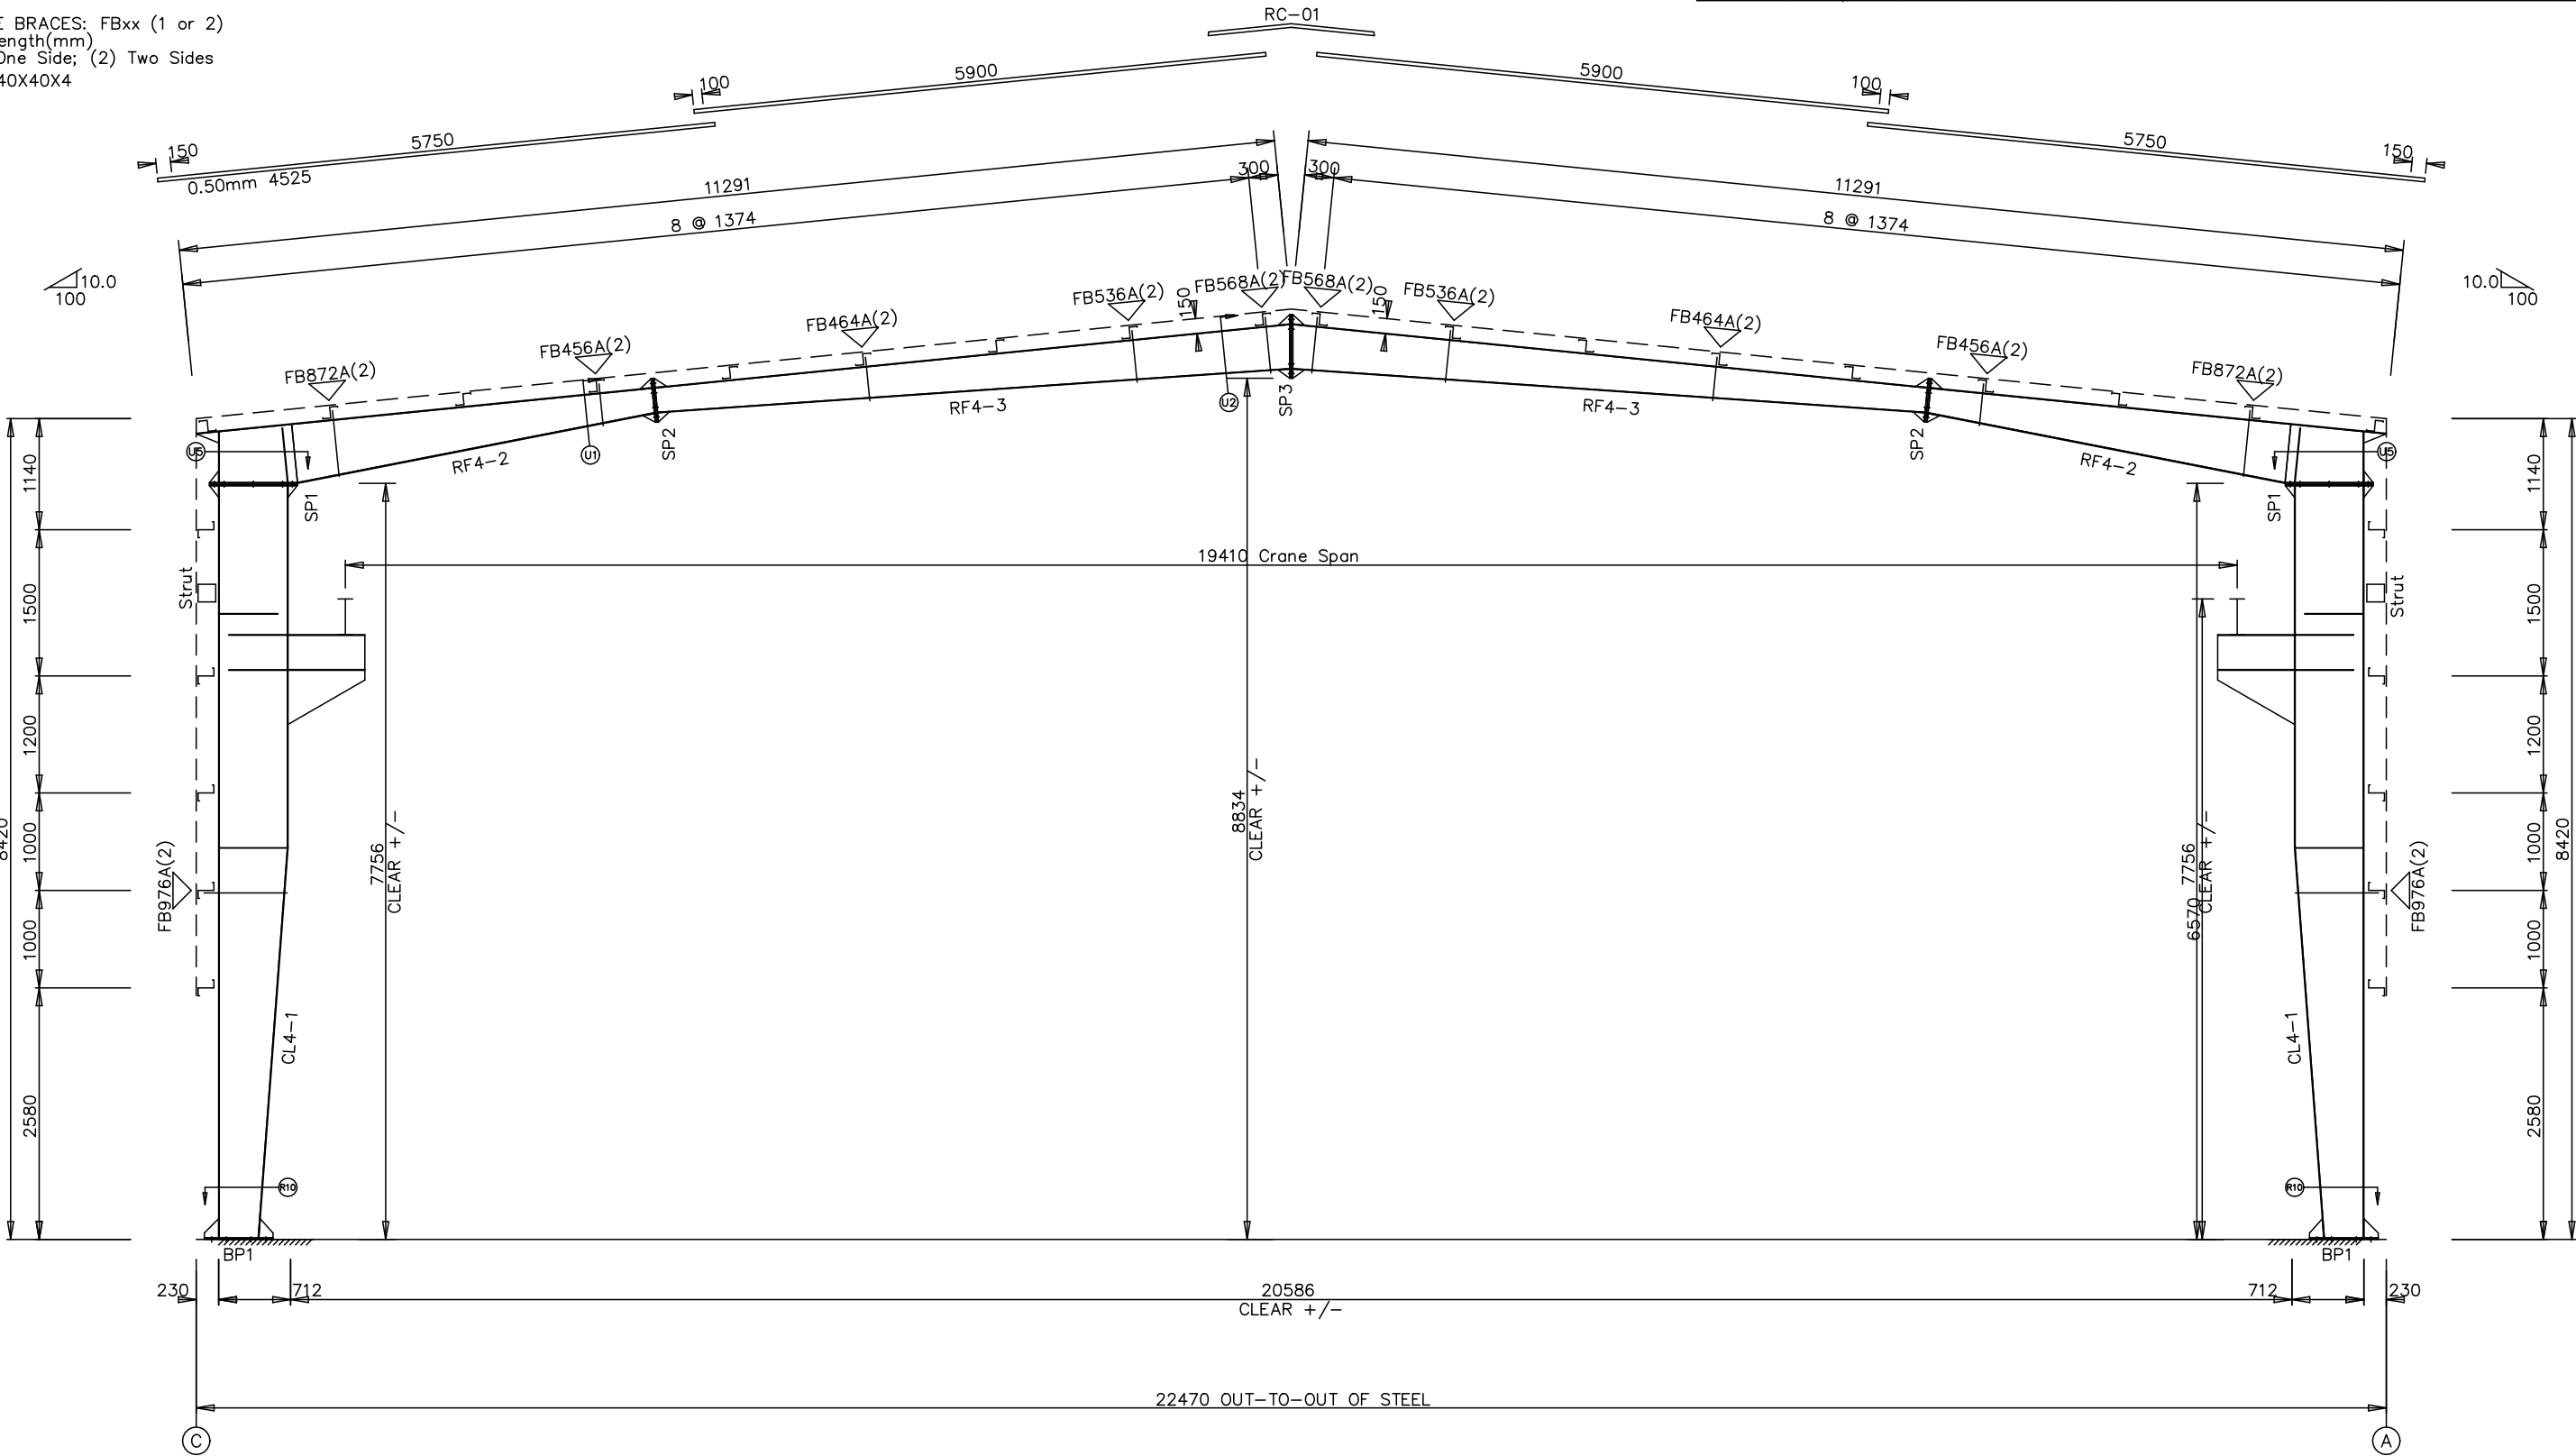

RIGID FRAME ELEVATION: FRAME LINE 6

| INFINITI SOLUTION |                    |                            |        |        |
|-------------------|--------------------|----------------------------|--------|--------|
| PROJECT           | Proposed Warehouse | RIGID FRAME ELEVATION      |        |        |
| ID                | C323-153-Final     | DESIGN:                    | DRAFT: | CHECK: |
| PROJECT ADDRESS   | Proposed Warehouse | DATE: 11/AUG/2025 SHEET OF |        |        |