


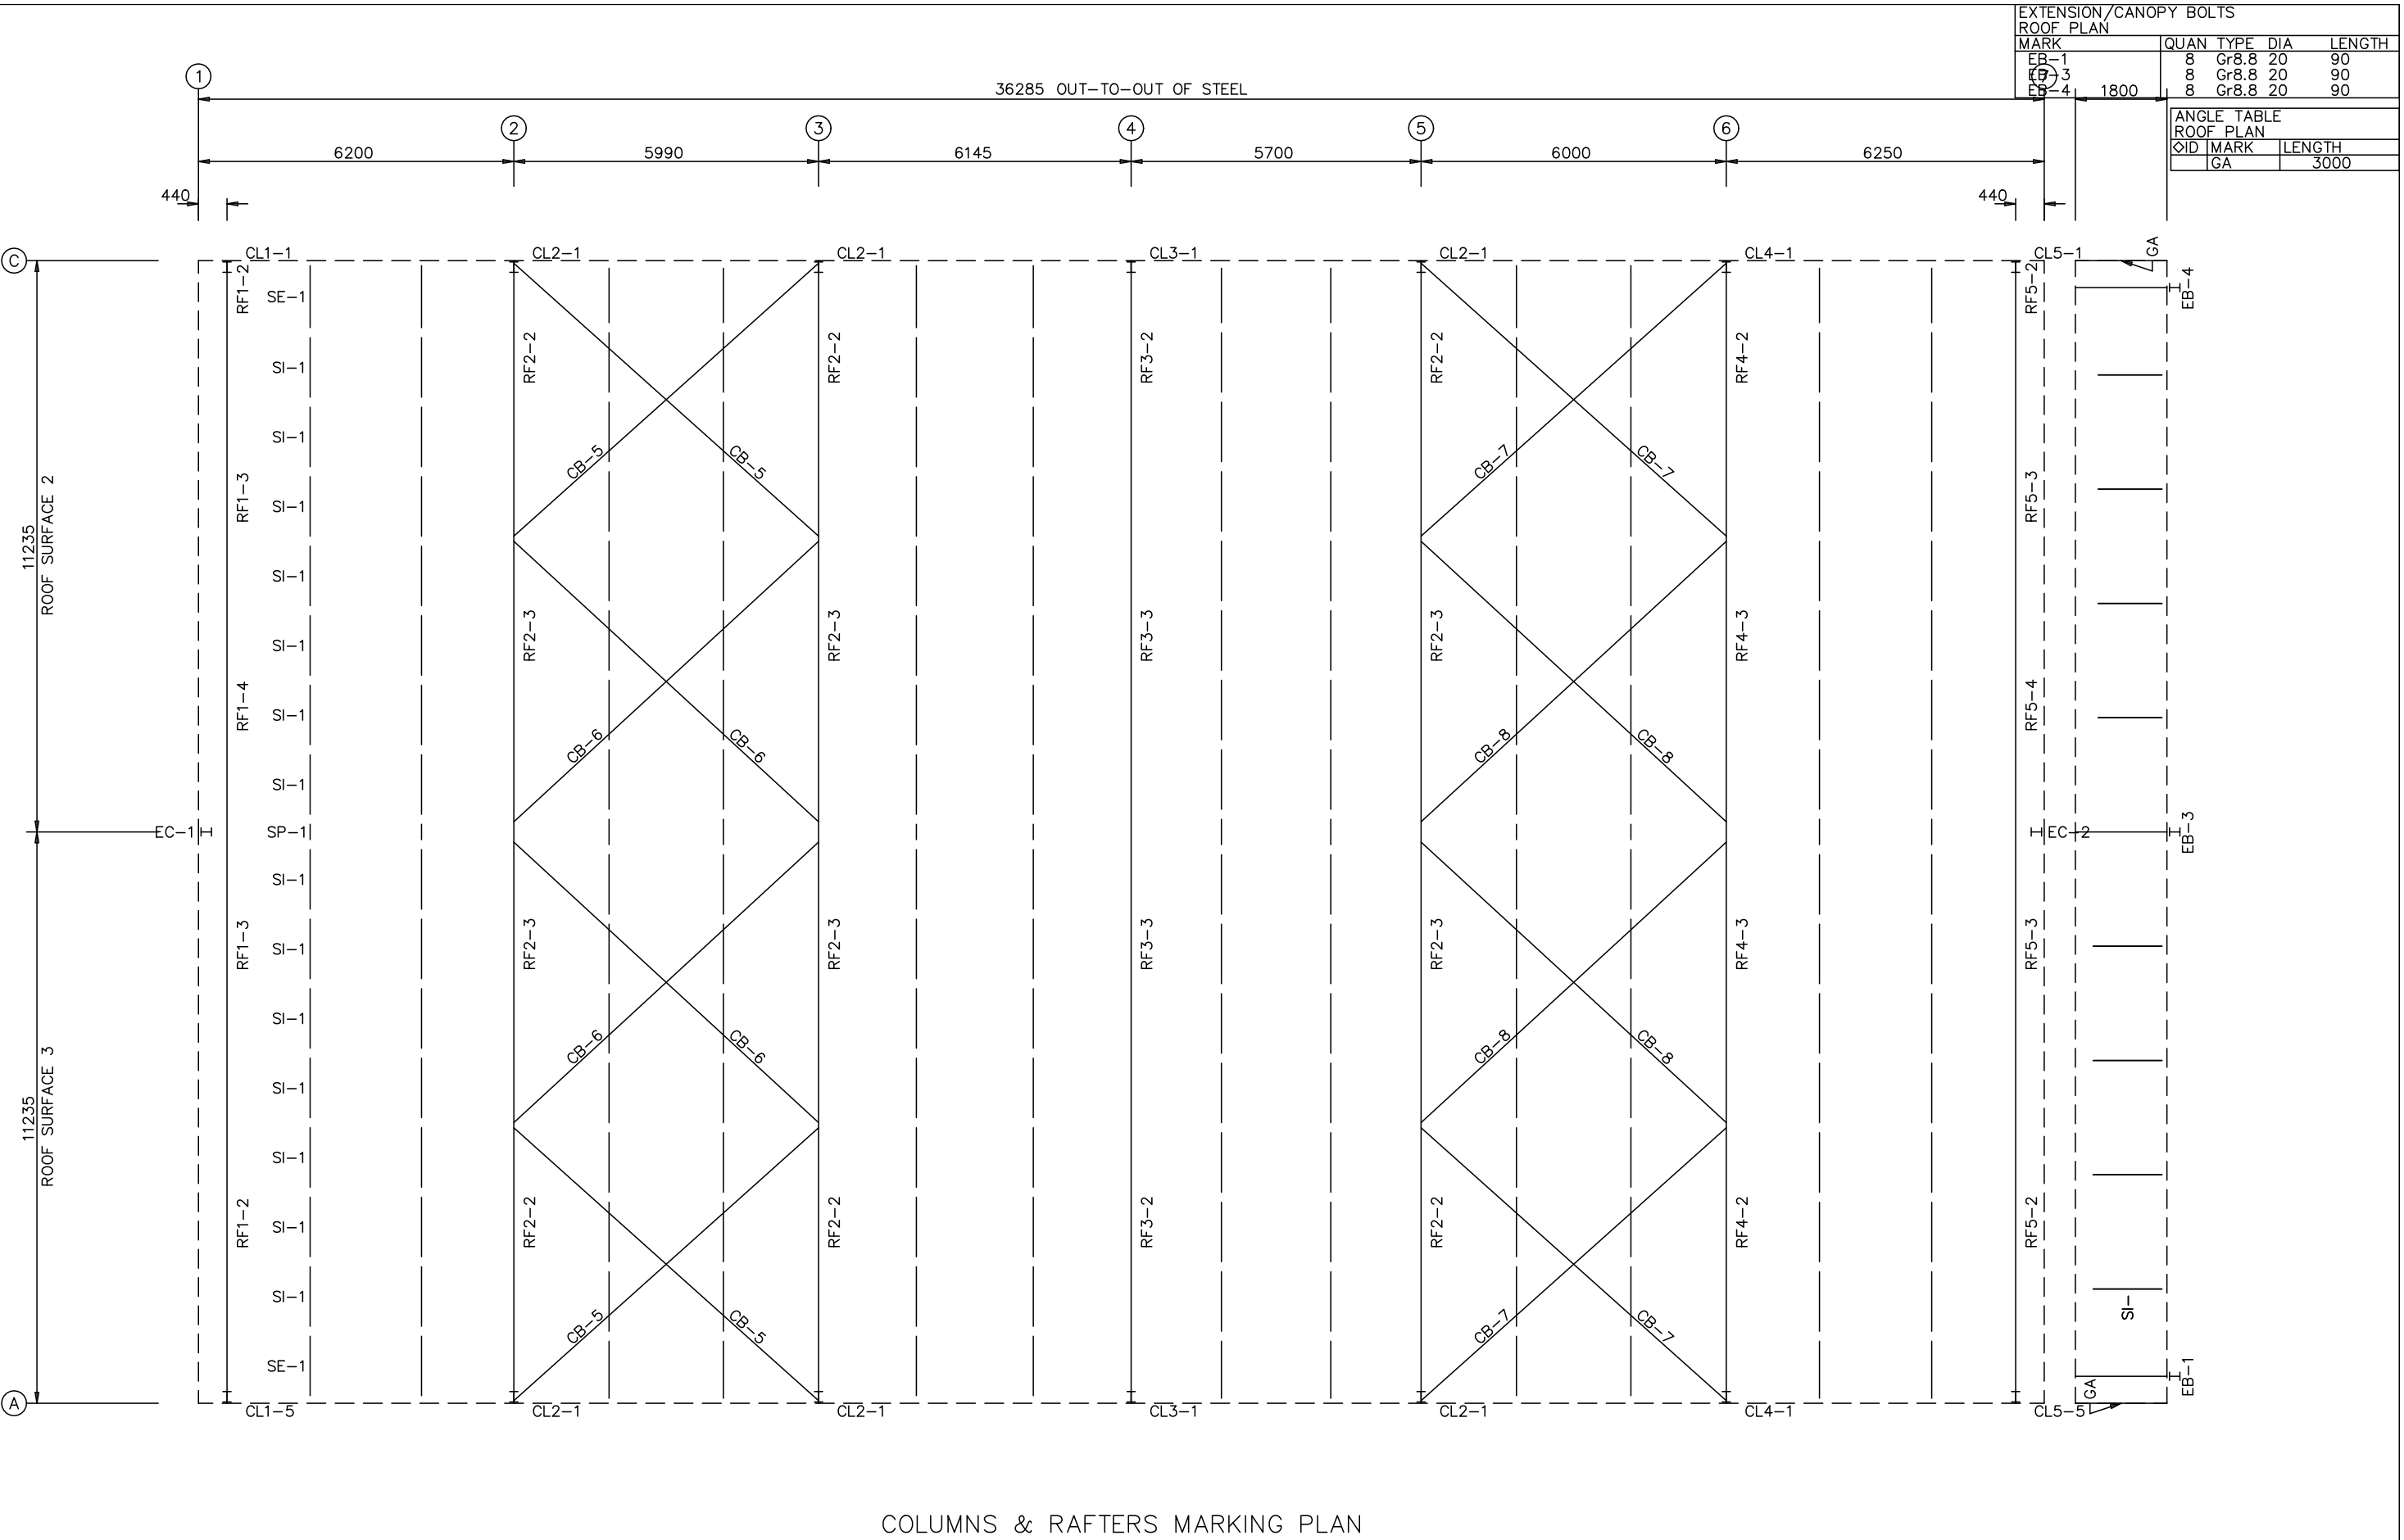

COLUMNS & RAFTERS MARKING PLAN

|                   |                    |  |                            |               |
|-------------------|--------------------|--|----------------------------|---------------|
| INFINITI SOLUTION |                    |  |                            |               |
| PROJECT           | Proposed Warehouse |  | ROOF FRAMING               |               |
| ID                | C323-153-Final     |  | DESIGN:                    | DRAFT: CHECK: |
| PROJECT ADDRESS   | Proposed Warehouse |  | DATE: 11/AUG/2025 SHEET OF |               |