


EXTENSION/CANOPY BOLTS				
ROOF PLAN				
MARK	QUAN	TYPE	DIA	LENGTH
EB-1	8	Gr8.8	20	90
EB-3	8	Gr8.8	20	90
EB-4	8	Gr8.8	20	90

MEMBER TABLE		
ROOF PLAN		
MARK	PART	LENGTH
EB-1	BEAM	2272
EB-3	BEAM	1830
EB-4	BEAM	2272
P-1	150Z15	6570
P-2	150Z15	6740
P-3	150Z15	6895
P-4	150Z15	6450
P-5	150Z15	6750
P-6	150Z15	6620
P-7	150Z15	6570
P-8	150Z15	6620
P-9	250Z18	12235
P-10	250Z18	12235
E-1	150Z15	6570
E-2	150Z15	6740
E-3	150Z15	6895
E-4	150Z15	6450
E-5	150Z15	6750
E-6	150Z15	6620
E-7	150Z15	6570
E-8	150Z15	6620
E-9	250Z18	12240
E-10	250Z18	12240
CB-5	ROD20	7770
CB-6	ROD20	8080
CB-7	ROD20	7780
CB-8	ROD20	8090
SP-1	SROD12	697
SI-1	SROD12	1474
SE-1	SROD12	1394
SI-	SROD12	1519

ANGLE TABLE		
ROOF PLAN		
◊ID	MARK	LENGTH
	GA	3000

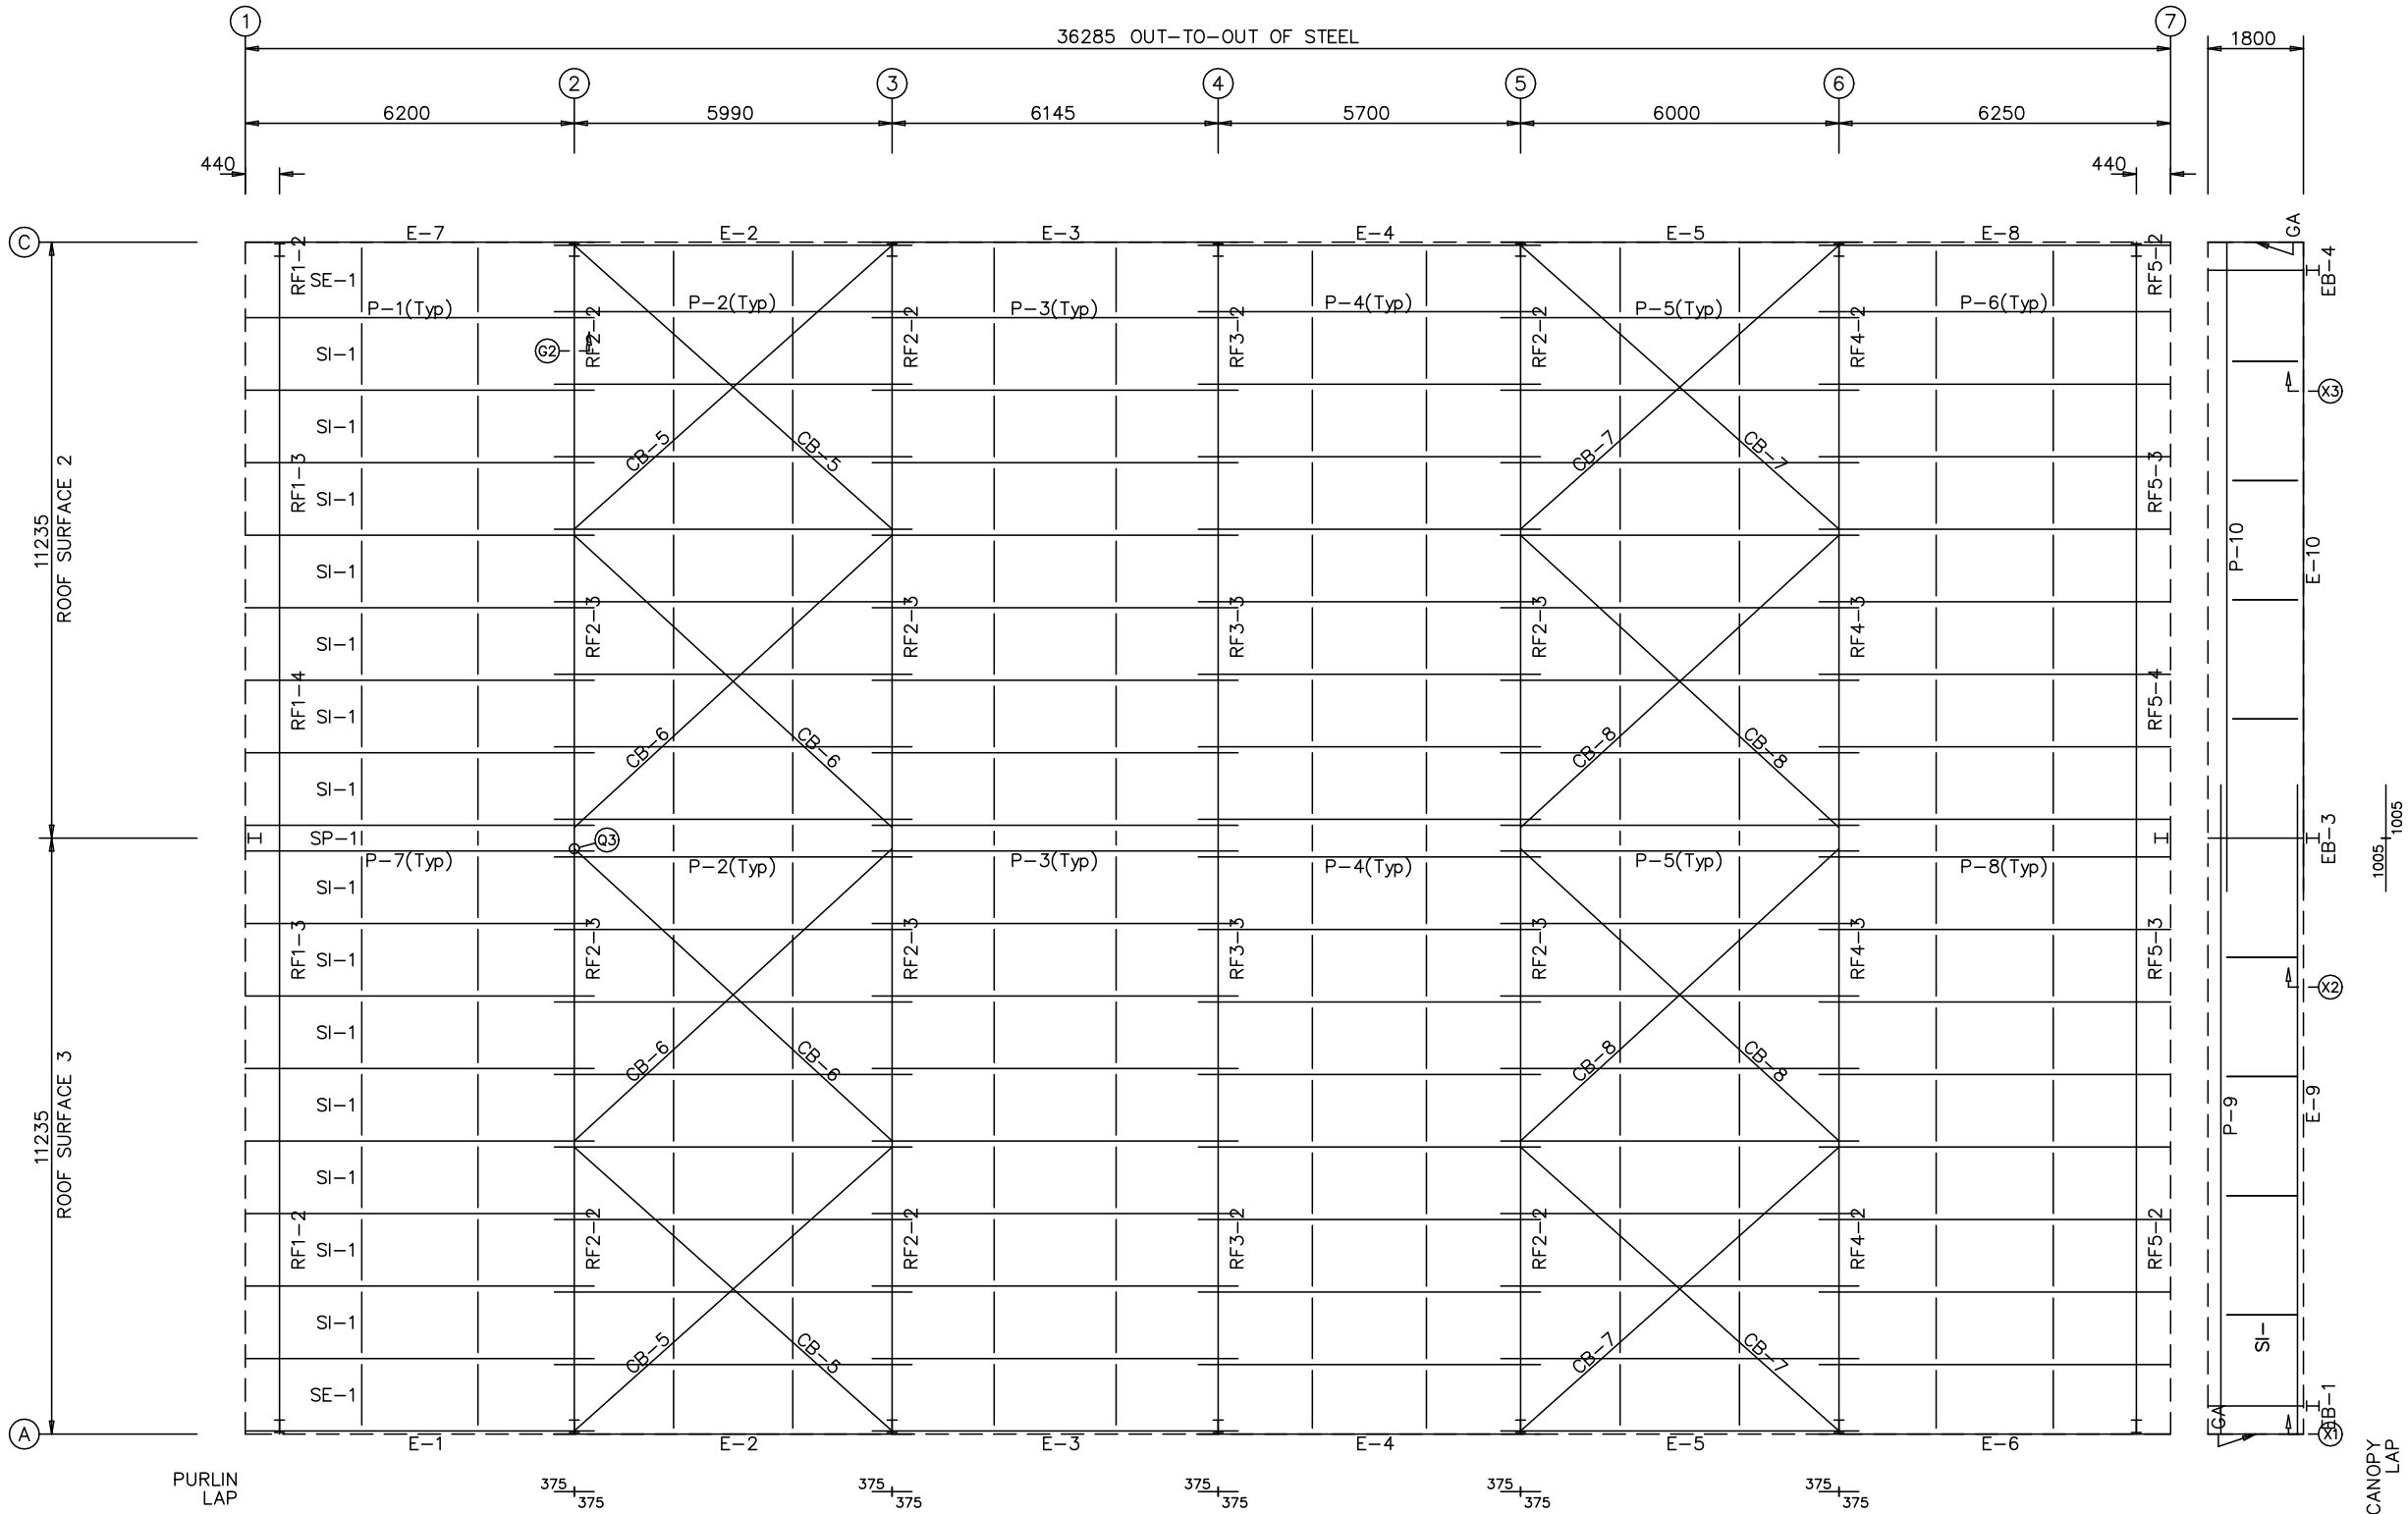

COLUMNS & RAFTERS MARKING PLAN

INFINITI SOLUTION				
PROJECT	Proposed Warehouse	ROOF FRAMING		
ID	C323-153-Final	DESIGN:	DRAFT:	CHECK:
PROJECT ADDRESS	Proposed Warehouse	DATE: 11/AUG/2025 SHEET OF		