


BOLT TABLE				
FRAME LINE A				
LOCATION	QUAN	TYPE	DIA	LENGTH
Strut	2	Gr8.8	16	70
EB-2 (L)	4	Gr8.8	16	
EB-2 (R)	8	Gr8.8	20	90

SPECIAL BOLTS				
Ø ID	QUAN	TYPE	DIA	LENGTH WASH
3	2	Gr8.8	16	70 2

MEMBER TABLE		
FRAME LINE A		
MARK	PART	LENGTH
EB-1	BEAM	2272
EB-2	W30a155	5805
G-14	200Z15	6570
G-15	200Z15	6740
G-16	200Z15	6895
G-17	200Z15	6450
G-18	200Z15	6750
G-19	200Z15	6620
ST-1	T80x32	5945
ST-2	T80x32	5955
CB-1	ROD20	8630
CB-2	ROD20	6120
CB-3	ROD20	8640
CB-4	ROD20	6130
JB-1	SROD12	1100
JB-2	SROD12	1300
JB-3	SROD12	1600
JB-5	SROD12	1090

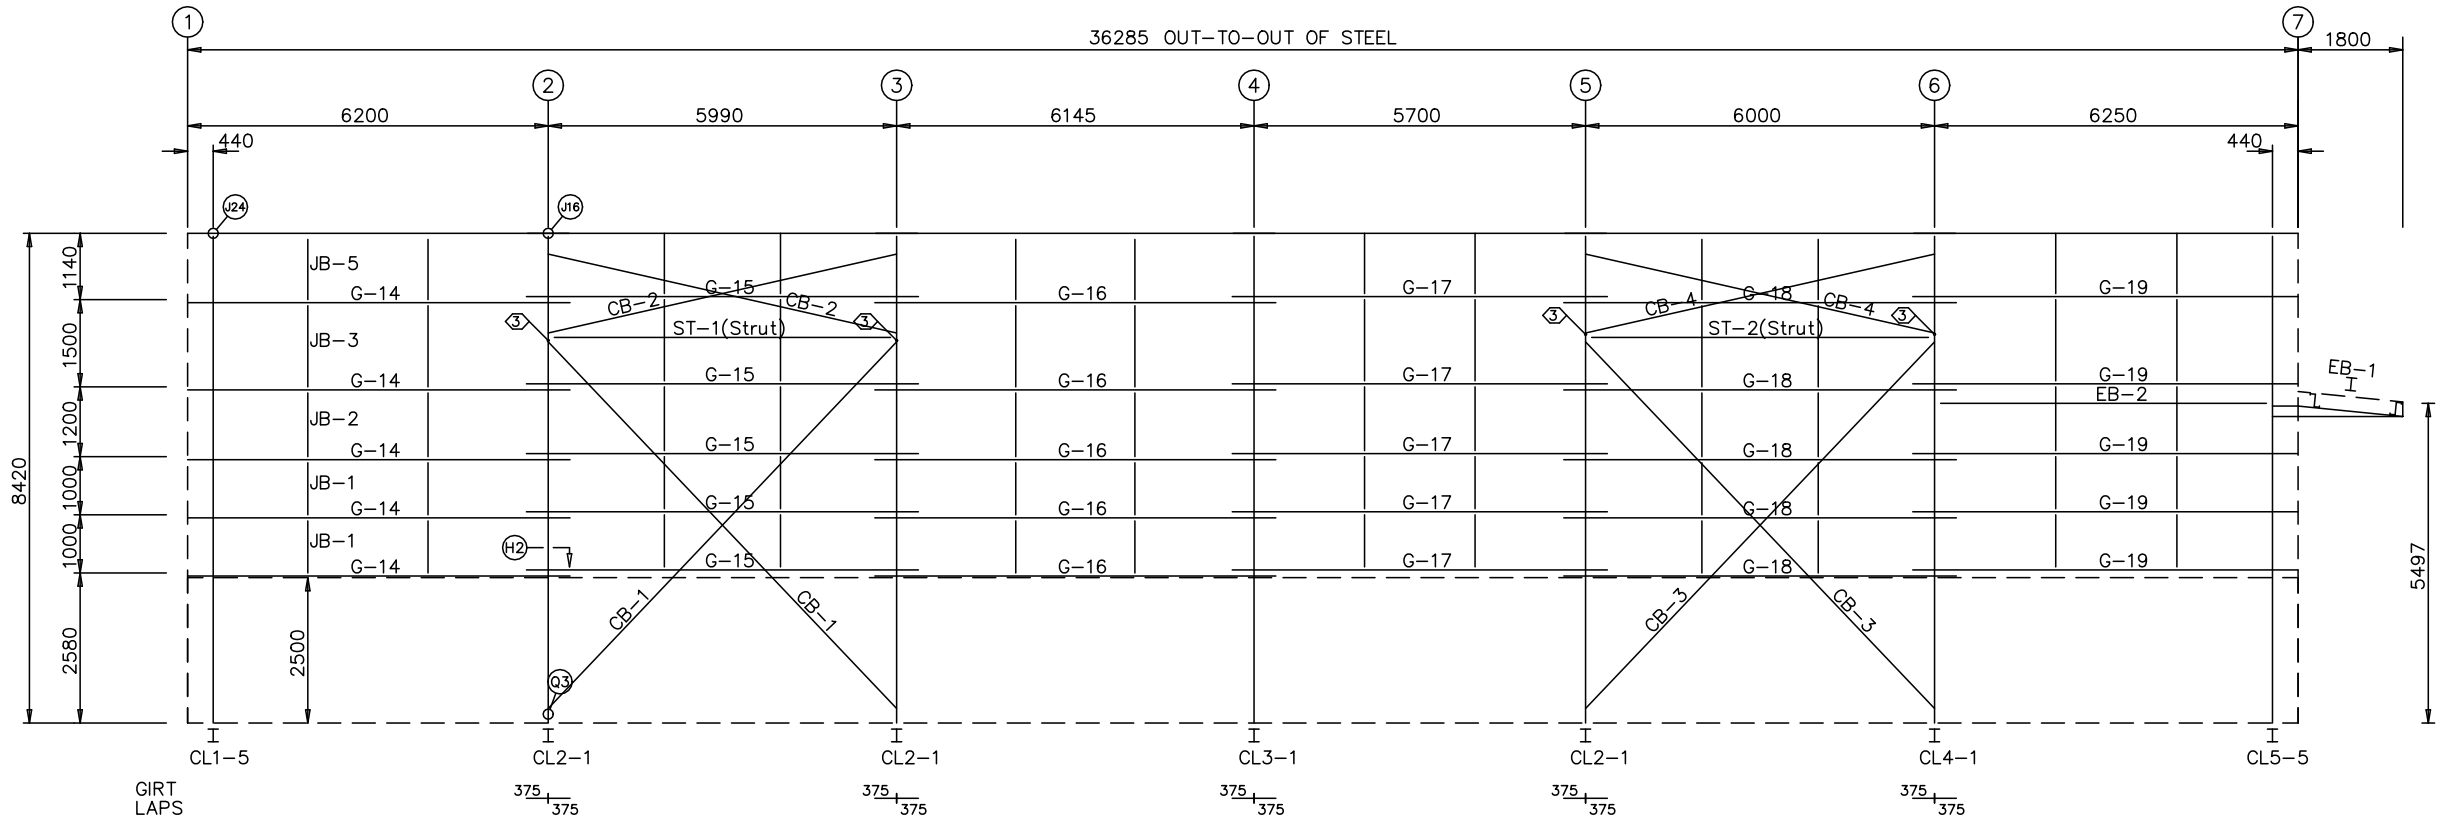

SIDEWALL FRAMING: FRAME LINE A

INFINITI SOLUTION				
PROJECT	Proposed Warehouse	SIDEWALL FRAMING		
ID	C323-153-Final	DESIGN:	DRAFT:	CHECK:
PROJECT ADDRESS	Proposed Warehouse	DATE: 11/AUG/2025 SHEET 1 OF 1		