
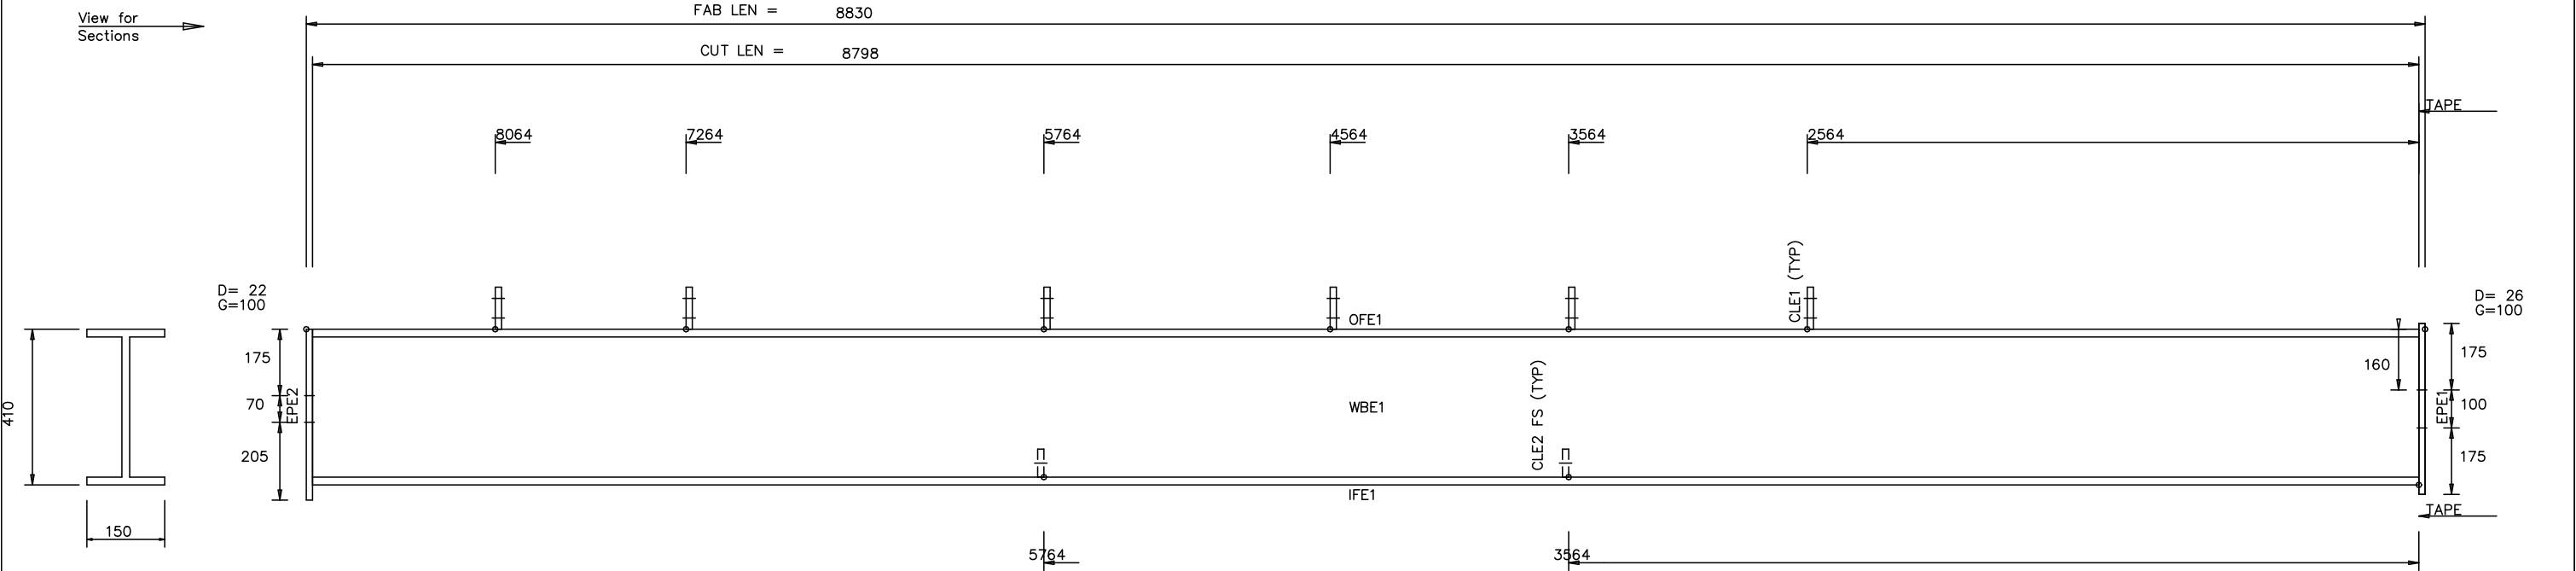
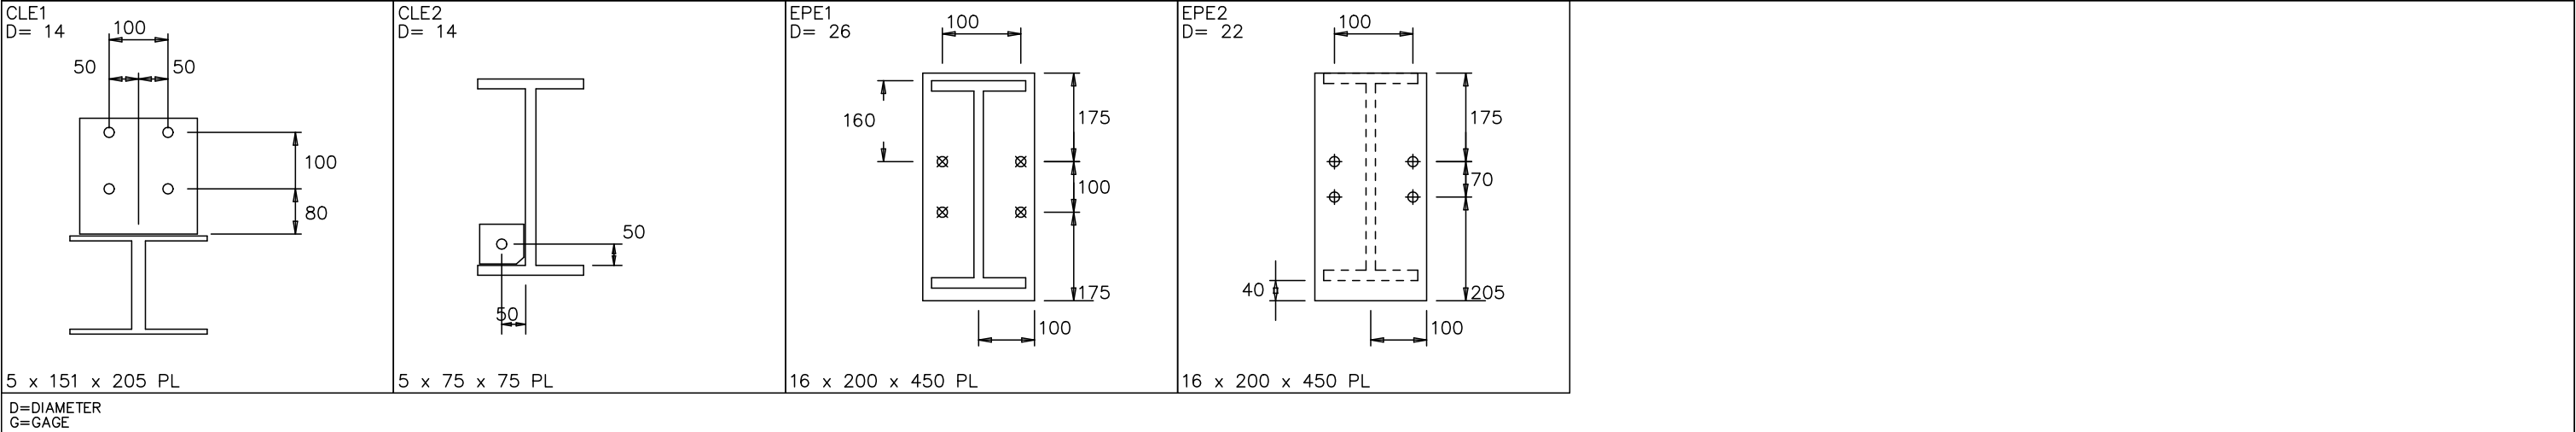


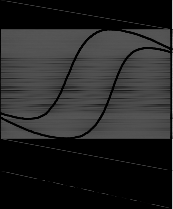

MARK	QNT	DESCRIPTION	Unit Wt
WBE1	1	5 x 400 x 8798 PL	138.2
OFE1	1	5 x 150 x 8798 PL	51.8
IFE1	1	5 x 150 x 8798 PL	51.8
CLE1	6	5 x 151 x 205 PL	7.3
CLE2	2	5 x 75 x 75 PL	0.4
EPE1	1	16 x 200 x 450 PL	11.3
EPE2	1	16 x 200 x 450 PL	11.3
		Weight Sum ..	272.3

						Project :		
						NAME : ENDWALL COLUMN		
						Job : C323-153-Final		Bldg.No.: 03Dec2013
						Qnt: 1	Mark: EC-1	Length: 8830
Rev.	Date	Description	Drw.	Chk.		WEIGHT: 272.3	Part: W40b155	Fin:Red Oxide