


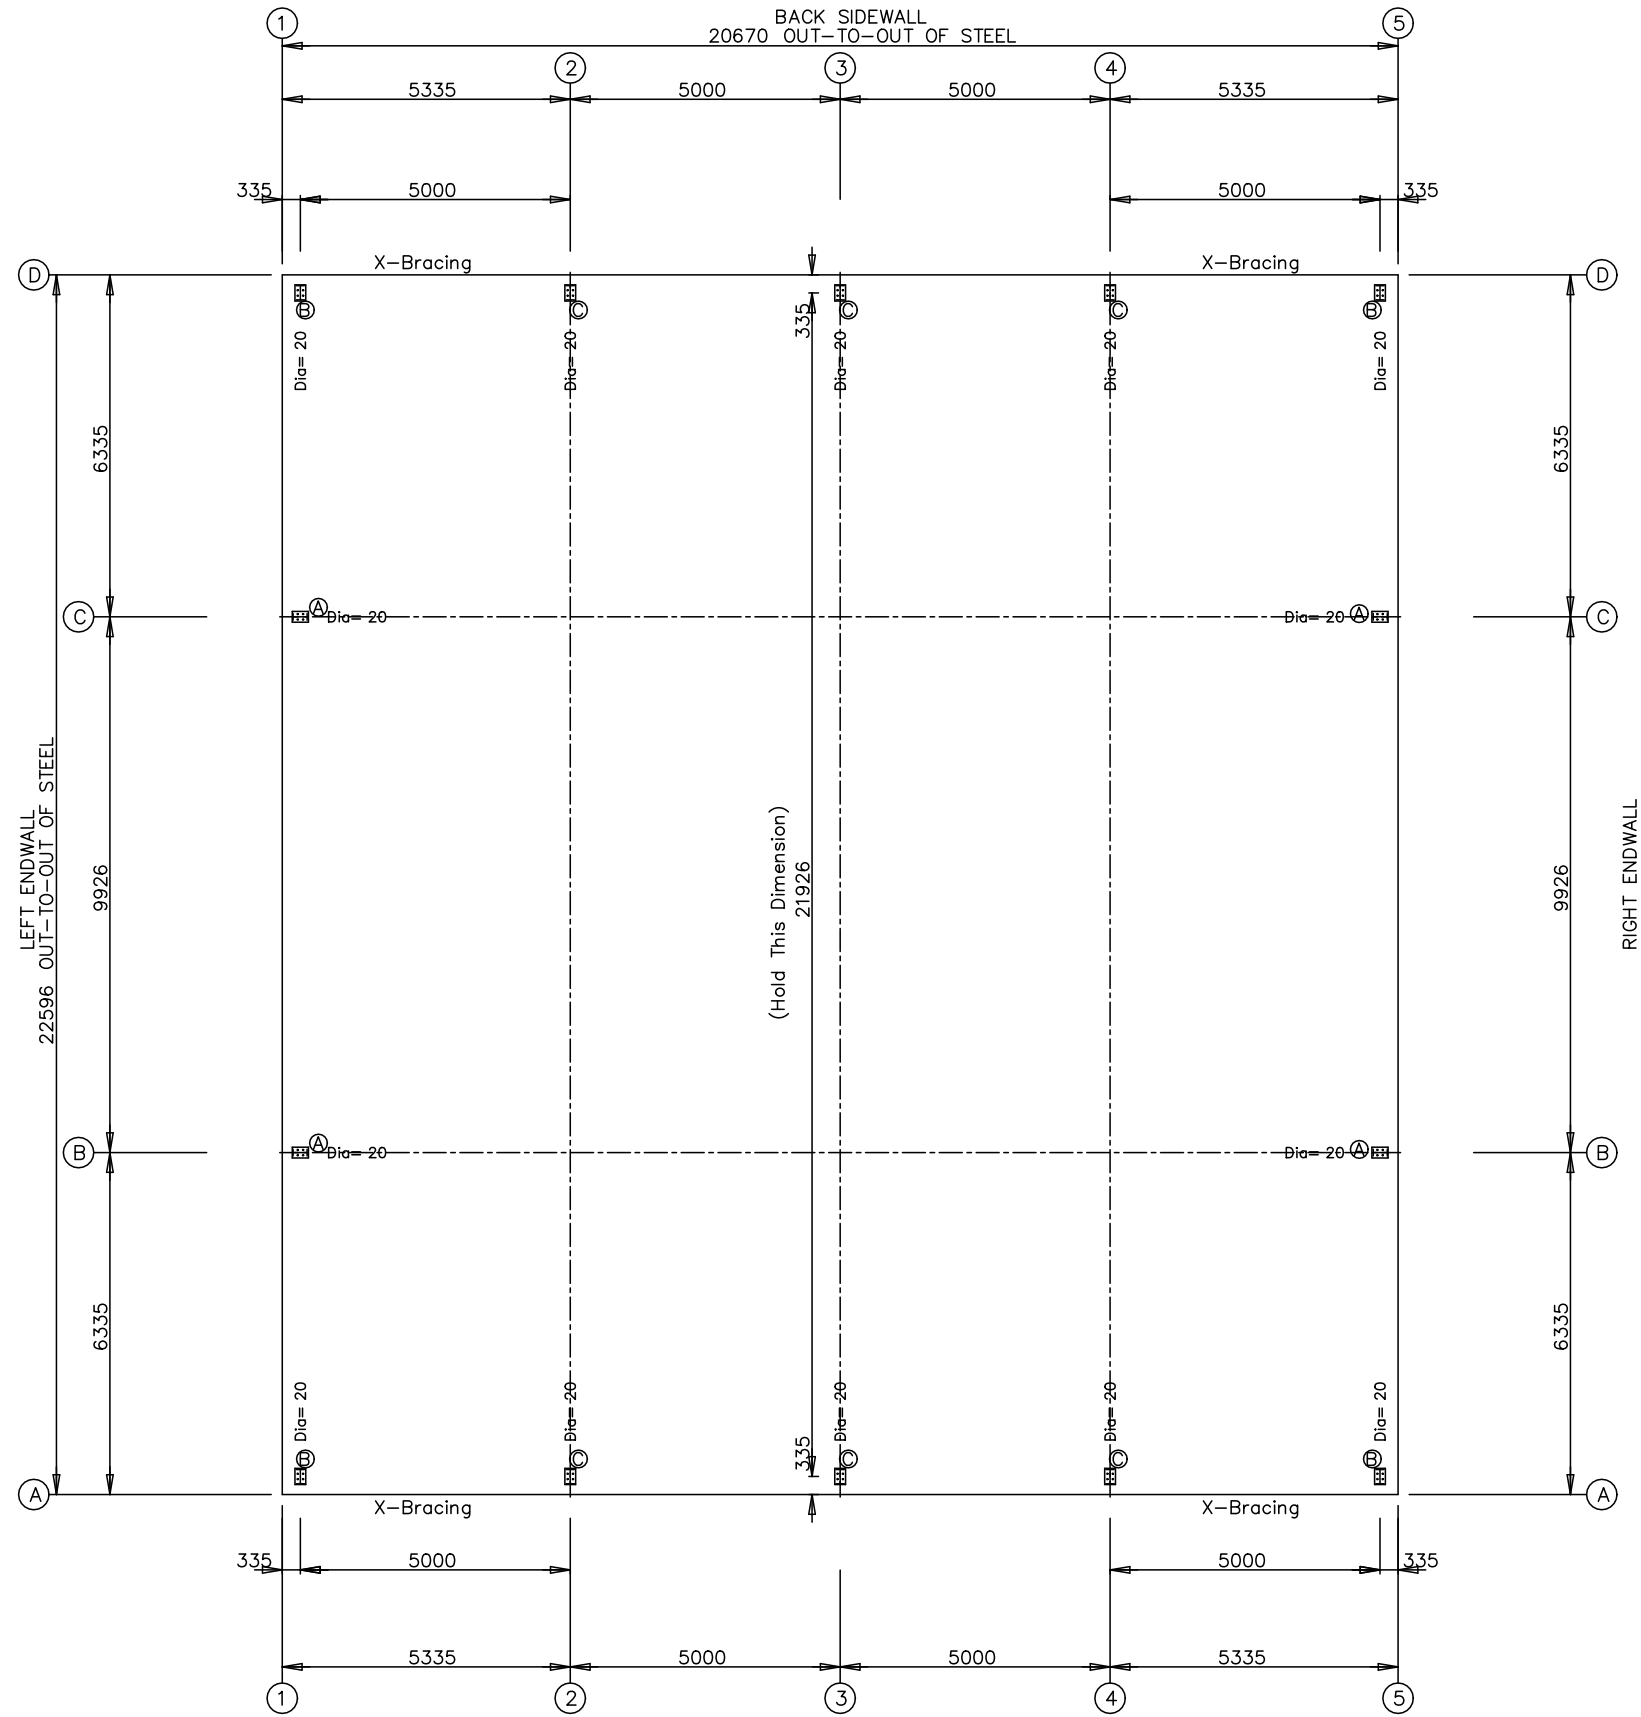

ANCHOR BOLT PLAN
NOTE: All Base Plates © 0 (U.N.)

Sivoko Steel Structures Ltd.				
PROJECT	Proposed Warehouse	ANCHOR BOLT PLAN		
ID	Q-1467	DESIGN:	DRAFT:	CHECK:
PROJECT ADDRESS	Proposed Warehouse	DATE: 15/DEC/2025 SHEET 1 OF 1		