


BOLT TABLE			
FRAME LINE 1			
LOCATION	QUAN	TYPE	DIA LENGTH
Columns/Raf	2	Gr8.8	16 70

MEMBER TABLE		
FRAME LINE 1		
MARK	PART	LENGTH
EC-1	W25a125	7692
EC-2	W25a125	7692
G-1	200Z15	6500
G-2	200Z15	4685
G-3	200Z15	10676
G-4	200Z15	8947
G-5	200Z15	6500
G-6	200Z15	4685
JB-1	SR0D12	1520
JB-2	SR0D12	1300
JB-3	SR0D12	1200

FLANGE BRACE TABLE		
FRAME LINE 1		
VID	MARK	LENGTH
1	FB424	424

CONNECTION PLATES		
FRAME LINE 1		
ID	MARK/PART	
1	d1	
2	r1	

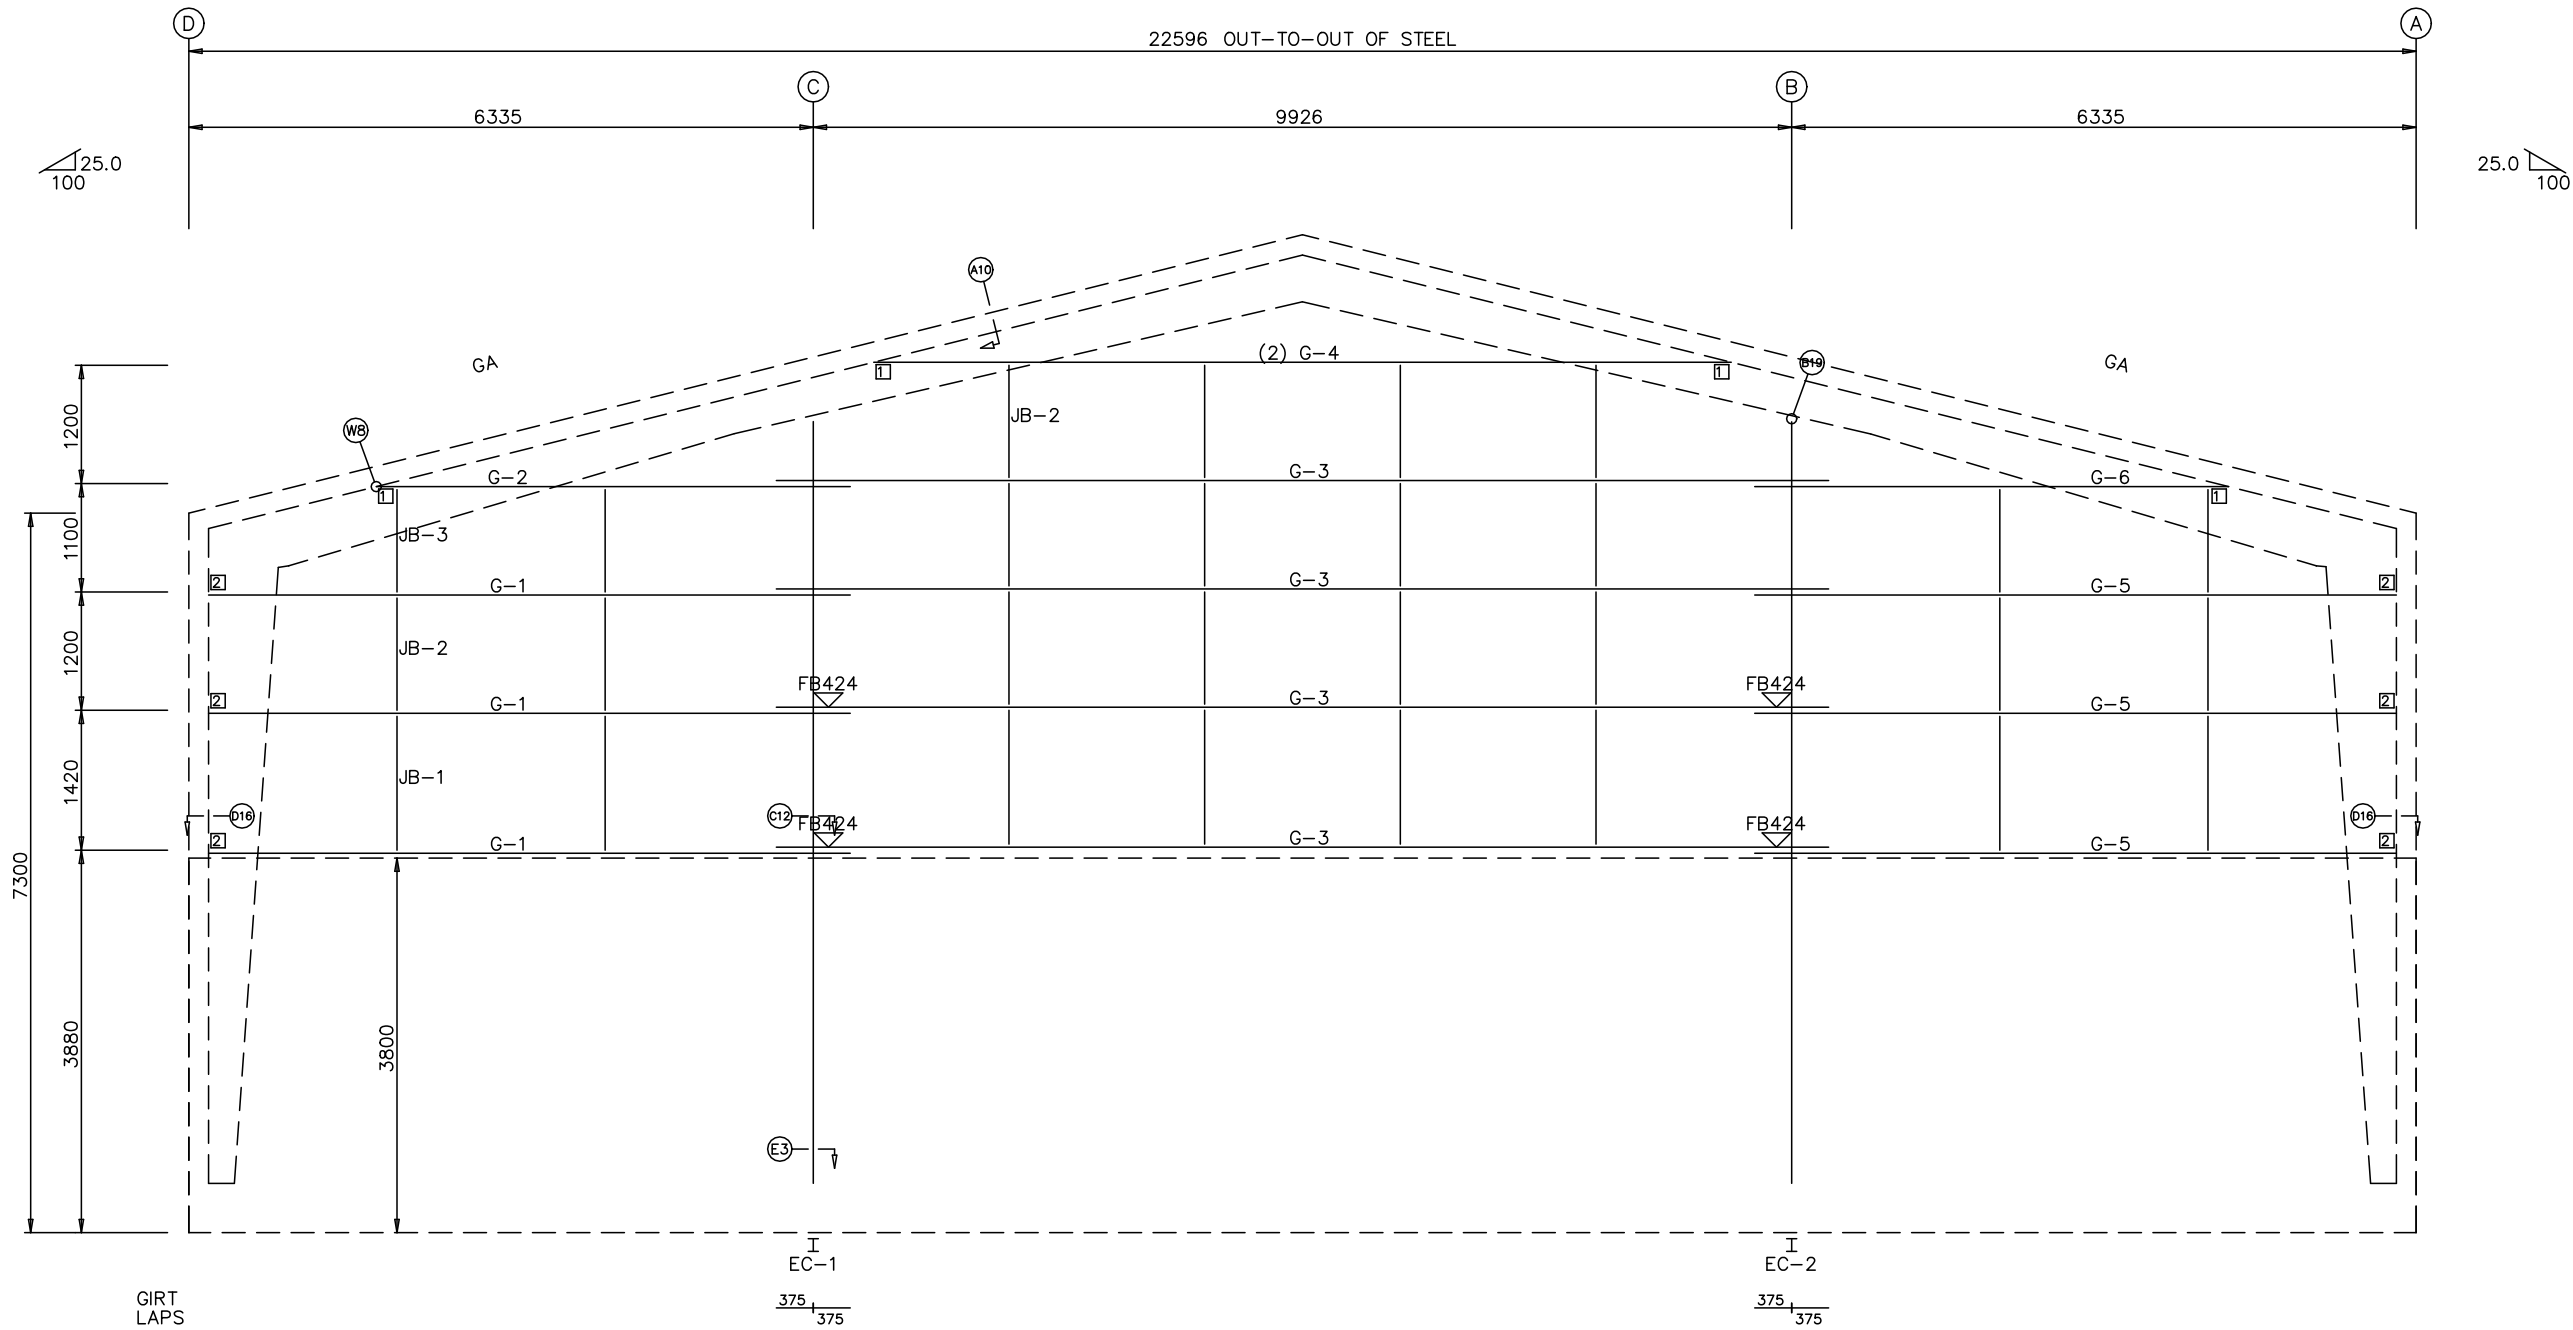

Sivoko Steel Structures Ltd.				
PROJECT	Proposed Warehouse	ENDWALL FRAMING		
ID	Q-1467	DESIGN:	DRAFT:	CHECK:
PROJECT ADDRESS	Proposed Warehouse	DATE: 15/DEC/2025 SHEET OF		