BOLT TABLE FRAME LINE 5				
LOCATION	QUAN	TYPE	DIA	LENGTH
Columns/Raf	2	Gr8.8	16	70

MEMBER TABLE FRAME LINE 5		
MARK	PART	LENGTH
EC–1	W25a125	7692
EC–2	W25a125	7692
G–1	200Z15	6500
G–2	200Z15	4685
G–3	200Z15	10676
G–4	200Z15	8947
G–5	200Z15	6500
G–6	200Z15	4685
JB–1	SROD12	1520
JB–2	SROD12	1300
JB–3	SROD12	1200

FLANGE BRACE TABLE FRAME LINE 5		
▽ID	MARK	LENGTH
1	FB424	424

CONNECTION PLATES FRAME LINE 5	
□ID	MARK/PART
1	d1
2	r1

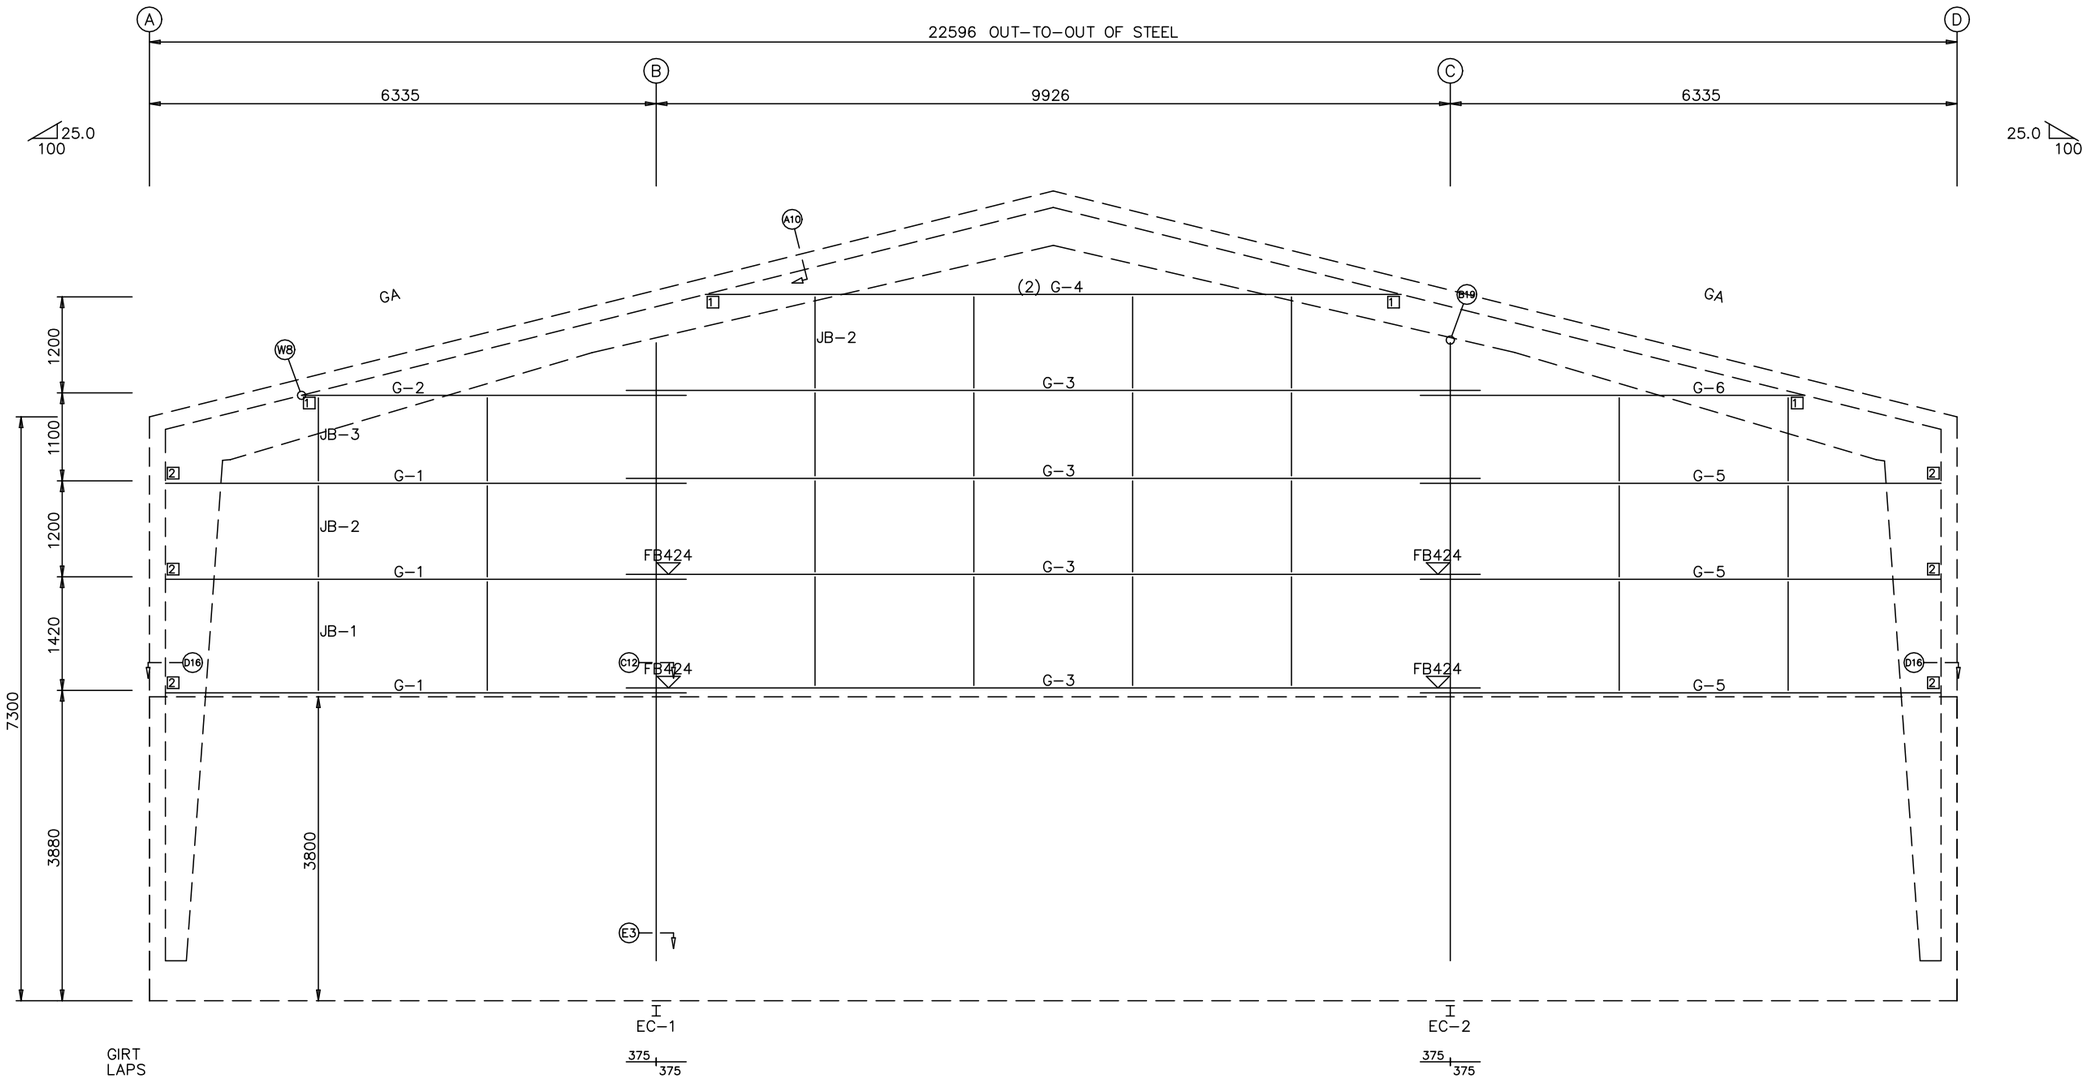

ENDWALL FRAMING: FRAME LINE 5

Sivoko Steel Structures Ltd.				
PROJECT	Proposed Warehouse	ENDWALL FRAMING		
ID	Q–1467	DESIGN:	DRAFT:	CHECK:
PROJECT ADDRESS	Proposed Warehouse	DATE: 15/DEC/2025	SHEET	OF