


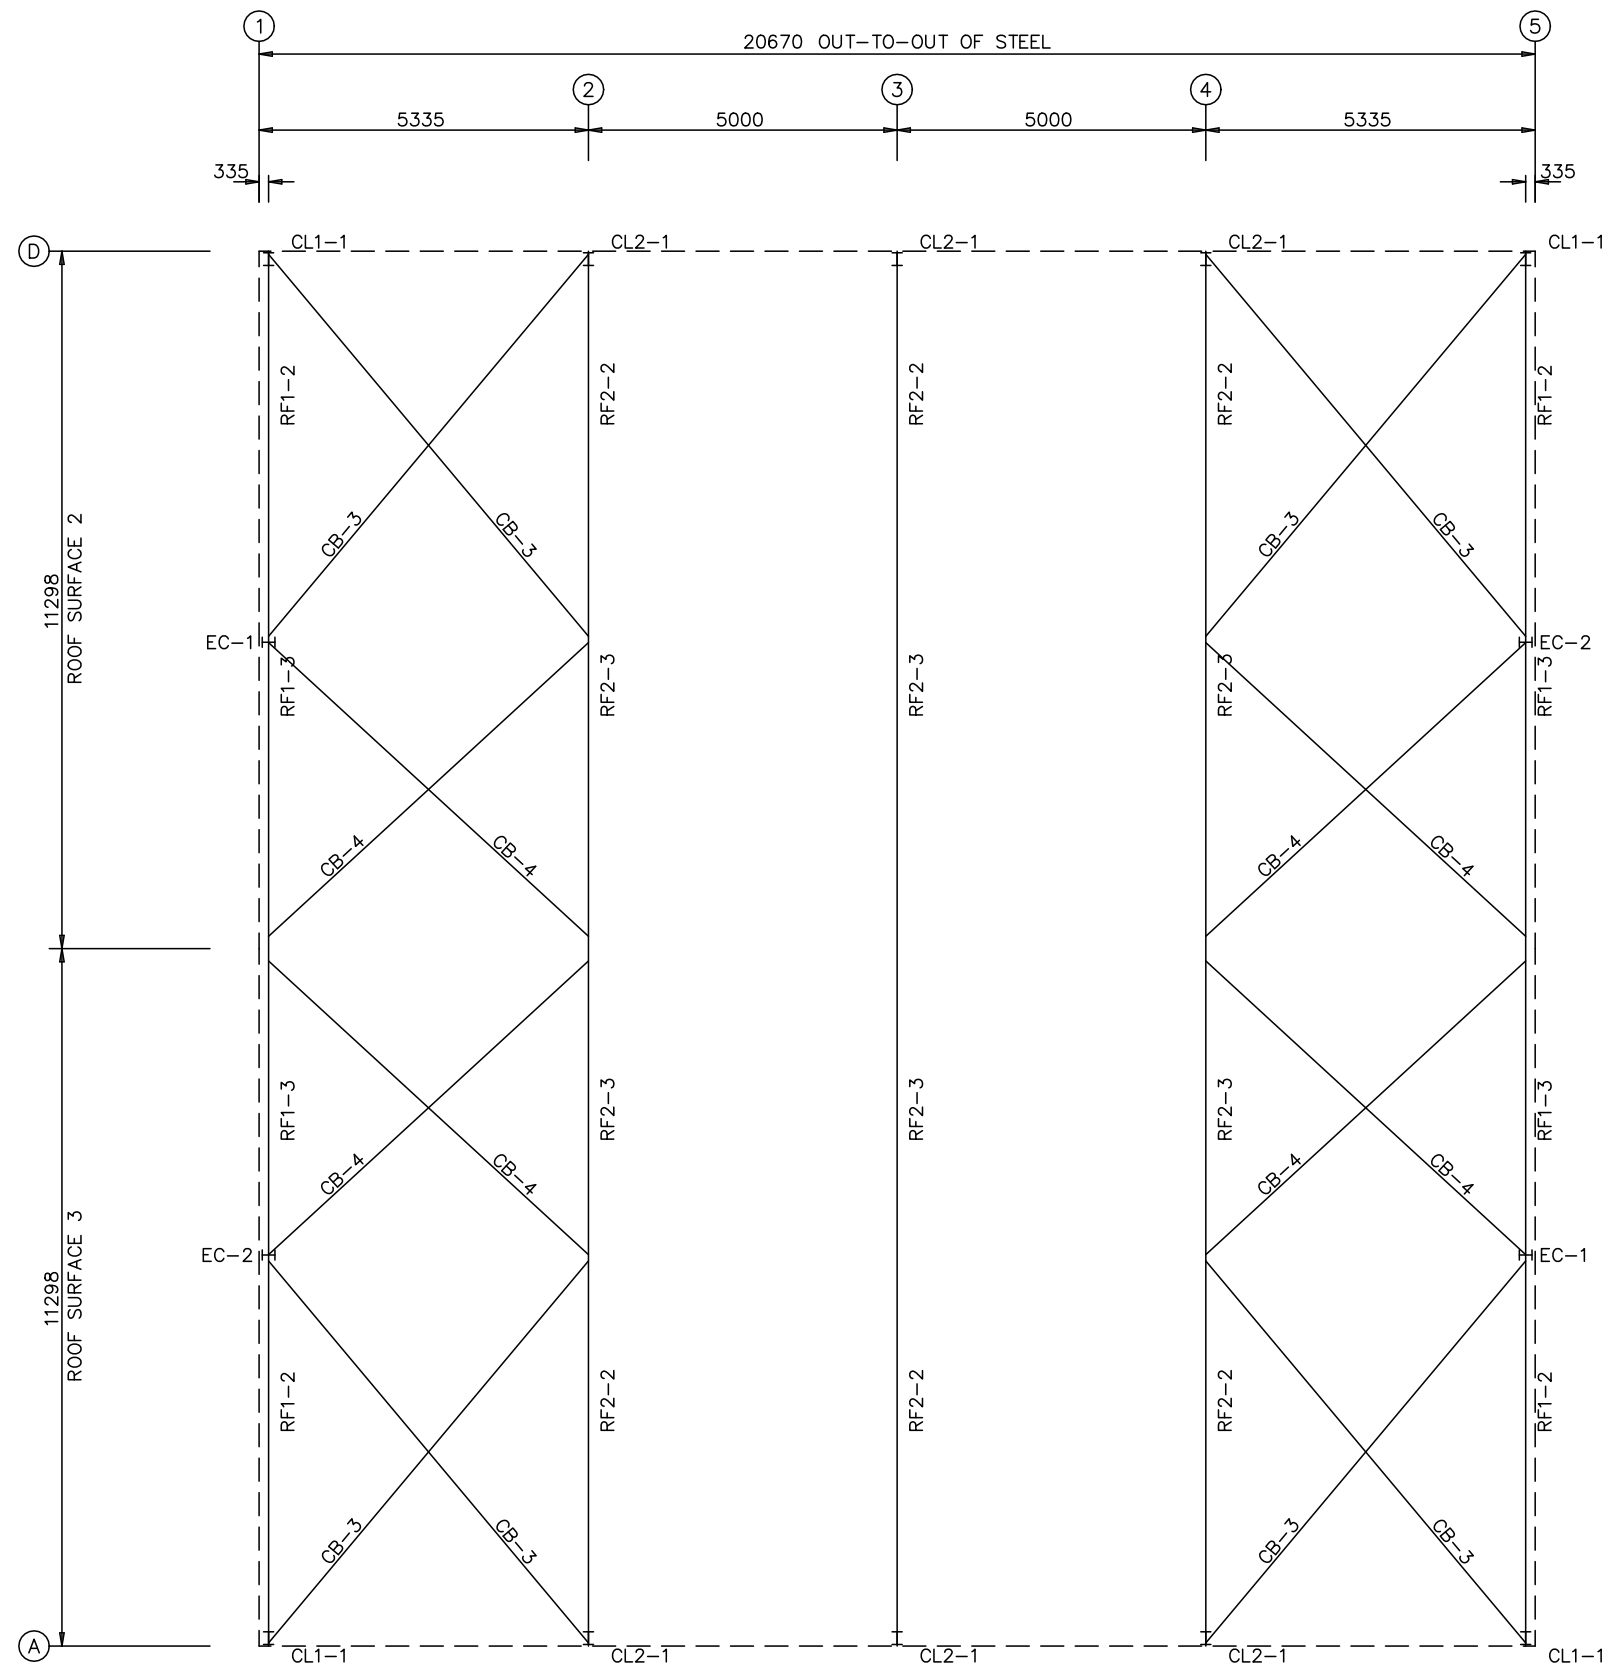

COLUMNS & RAFTERS MARKING PLAN

Sivoko Steel Structures Ltd.				
PROJECT	Proposed Warehouse	ROOF FRAMING		
ID	Q-1467	DESIGN:	DRAFT:	CHECK:
PROJECT ADDRESS	Proposed Warehouse	DATE: 15/DEC/2025	SHEET	OF