


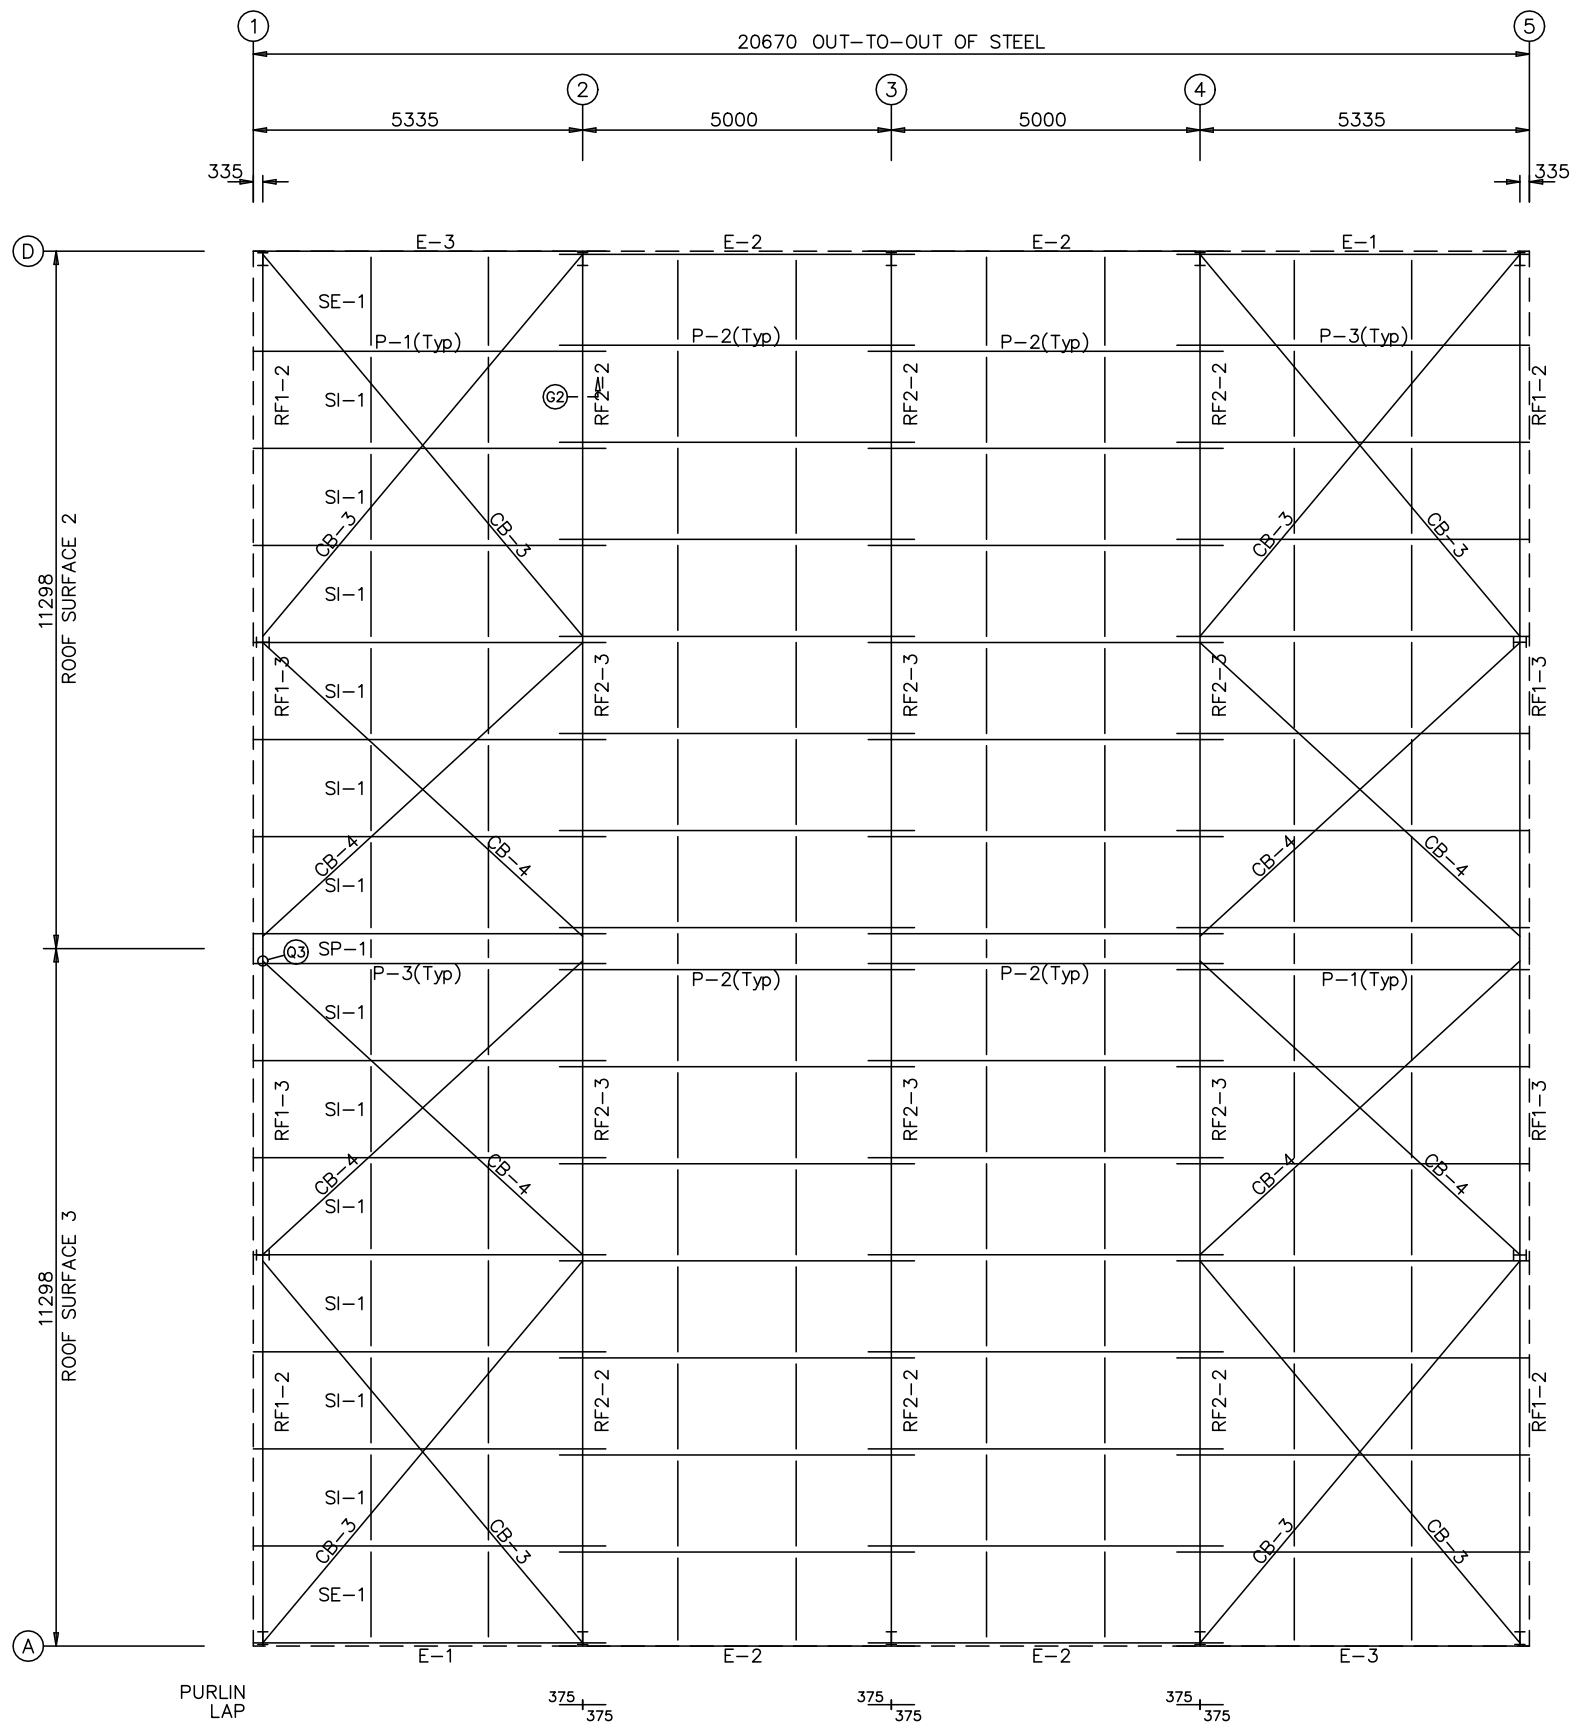

ROOF FRAMING PLAN

MEMBER TABLE		
ROOF PLAN		
MARK	PART	LENGTH
P-1	200Z15	5705
P-2	200Z15	5750
P-3	200Z15	5705
E-1	200Z15	5705
E-2	200Z15	5750
E-3	200Z15	5705
CB-3	ROD20	7810
CB-4	ROD20	6900
SP-1	SROD12	682
SI-1	SROD12	1721
SE-1	SROD12	1641

Sivoko Steel Structures Ltd.				
PROJECT	Proposed Warehouse	ROOF FRAMING		
ID	Q-1467	DESIGN:	DRAFT:	CHECK:
PROJECT ADDRESS	Proposed Warehouse	DATE: 15/DEC/2025 SHEET OF		