


BOLT TABLE				
FRAME LINE D				
LOCATION	QUAN	TYPE	DIA	LENGTH
Strut	2	Gr8.8	16	70

SPECIAL BOLTS					
Ø ID	QUAN	TYPE	DIA	LENGTH	WASH
3	2	Gr8.8	16	70	2

MEMBER TABLE		
FRAME LINE D		
MARK	PART	LENGTH
G-7	200Z15	5705
G-8	200Z15	5750
G-9	200Z15	5705
ST-1	T72x32	4958
CB-1	ROD20	6680
CB-2	ROD20	5190
JB-1	SROD12	1520
JB-2	SROD12	1300
JB-4	SROD12	700

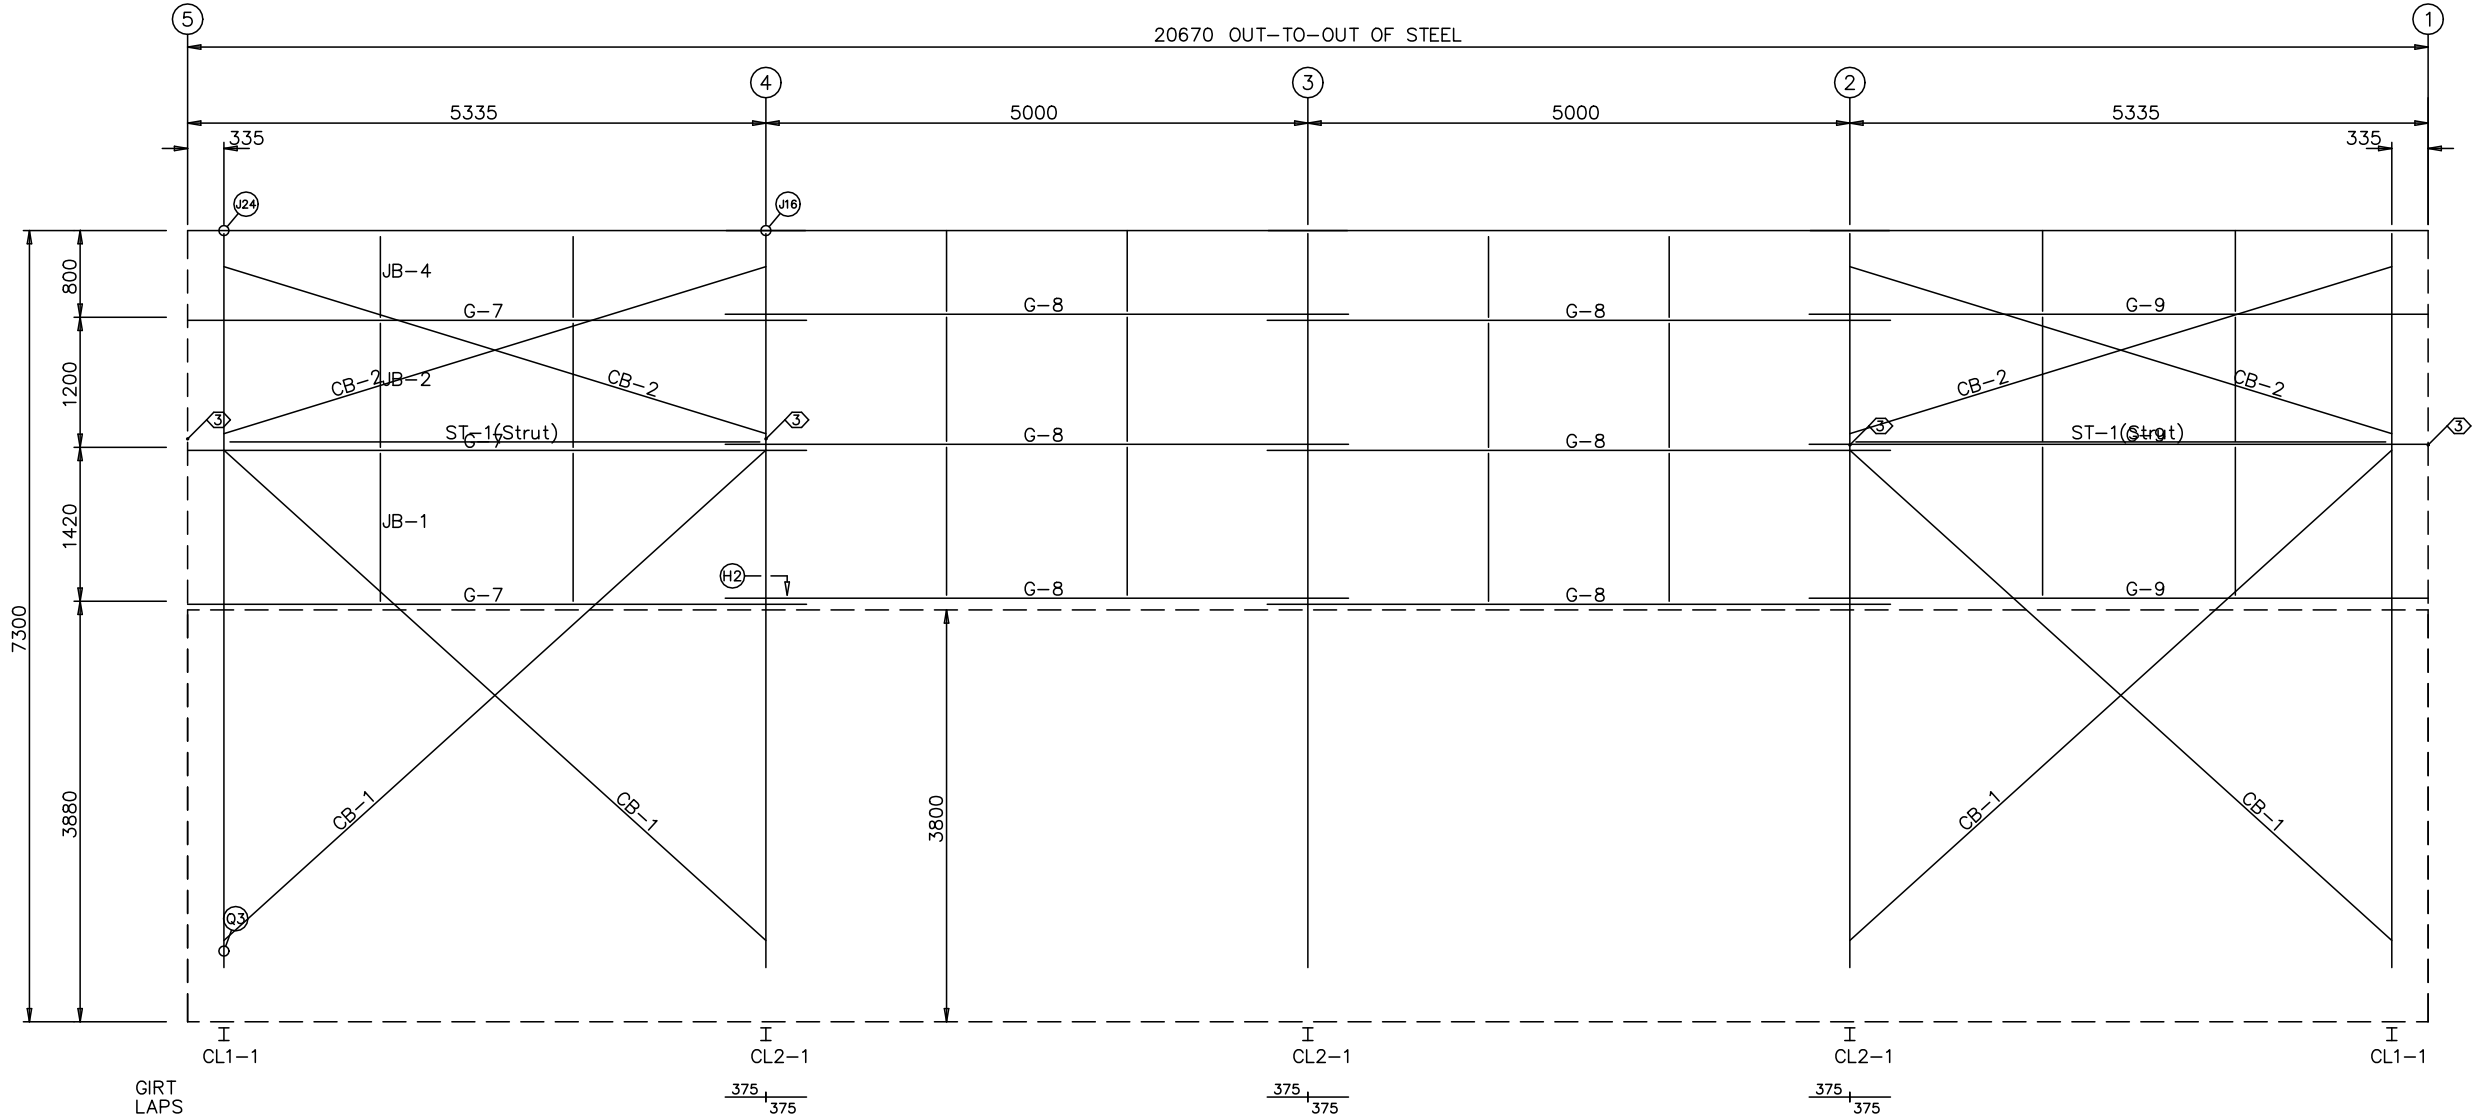

SIDEWALL FRAMING: FRAME LINE D

Sivoko Steel Structures Ltd.				
PROJECT	Proposed Warehouse	SIDEWALL FRAMING		
ID	Q-1467	DESIGN:	DRAFT:	CHECK:
PROJECT ADDRESS	Proposed Warehouse	DATE: 15/DEC/2025 SHEET OF		