


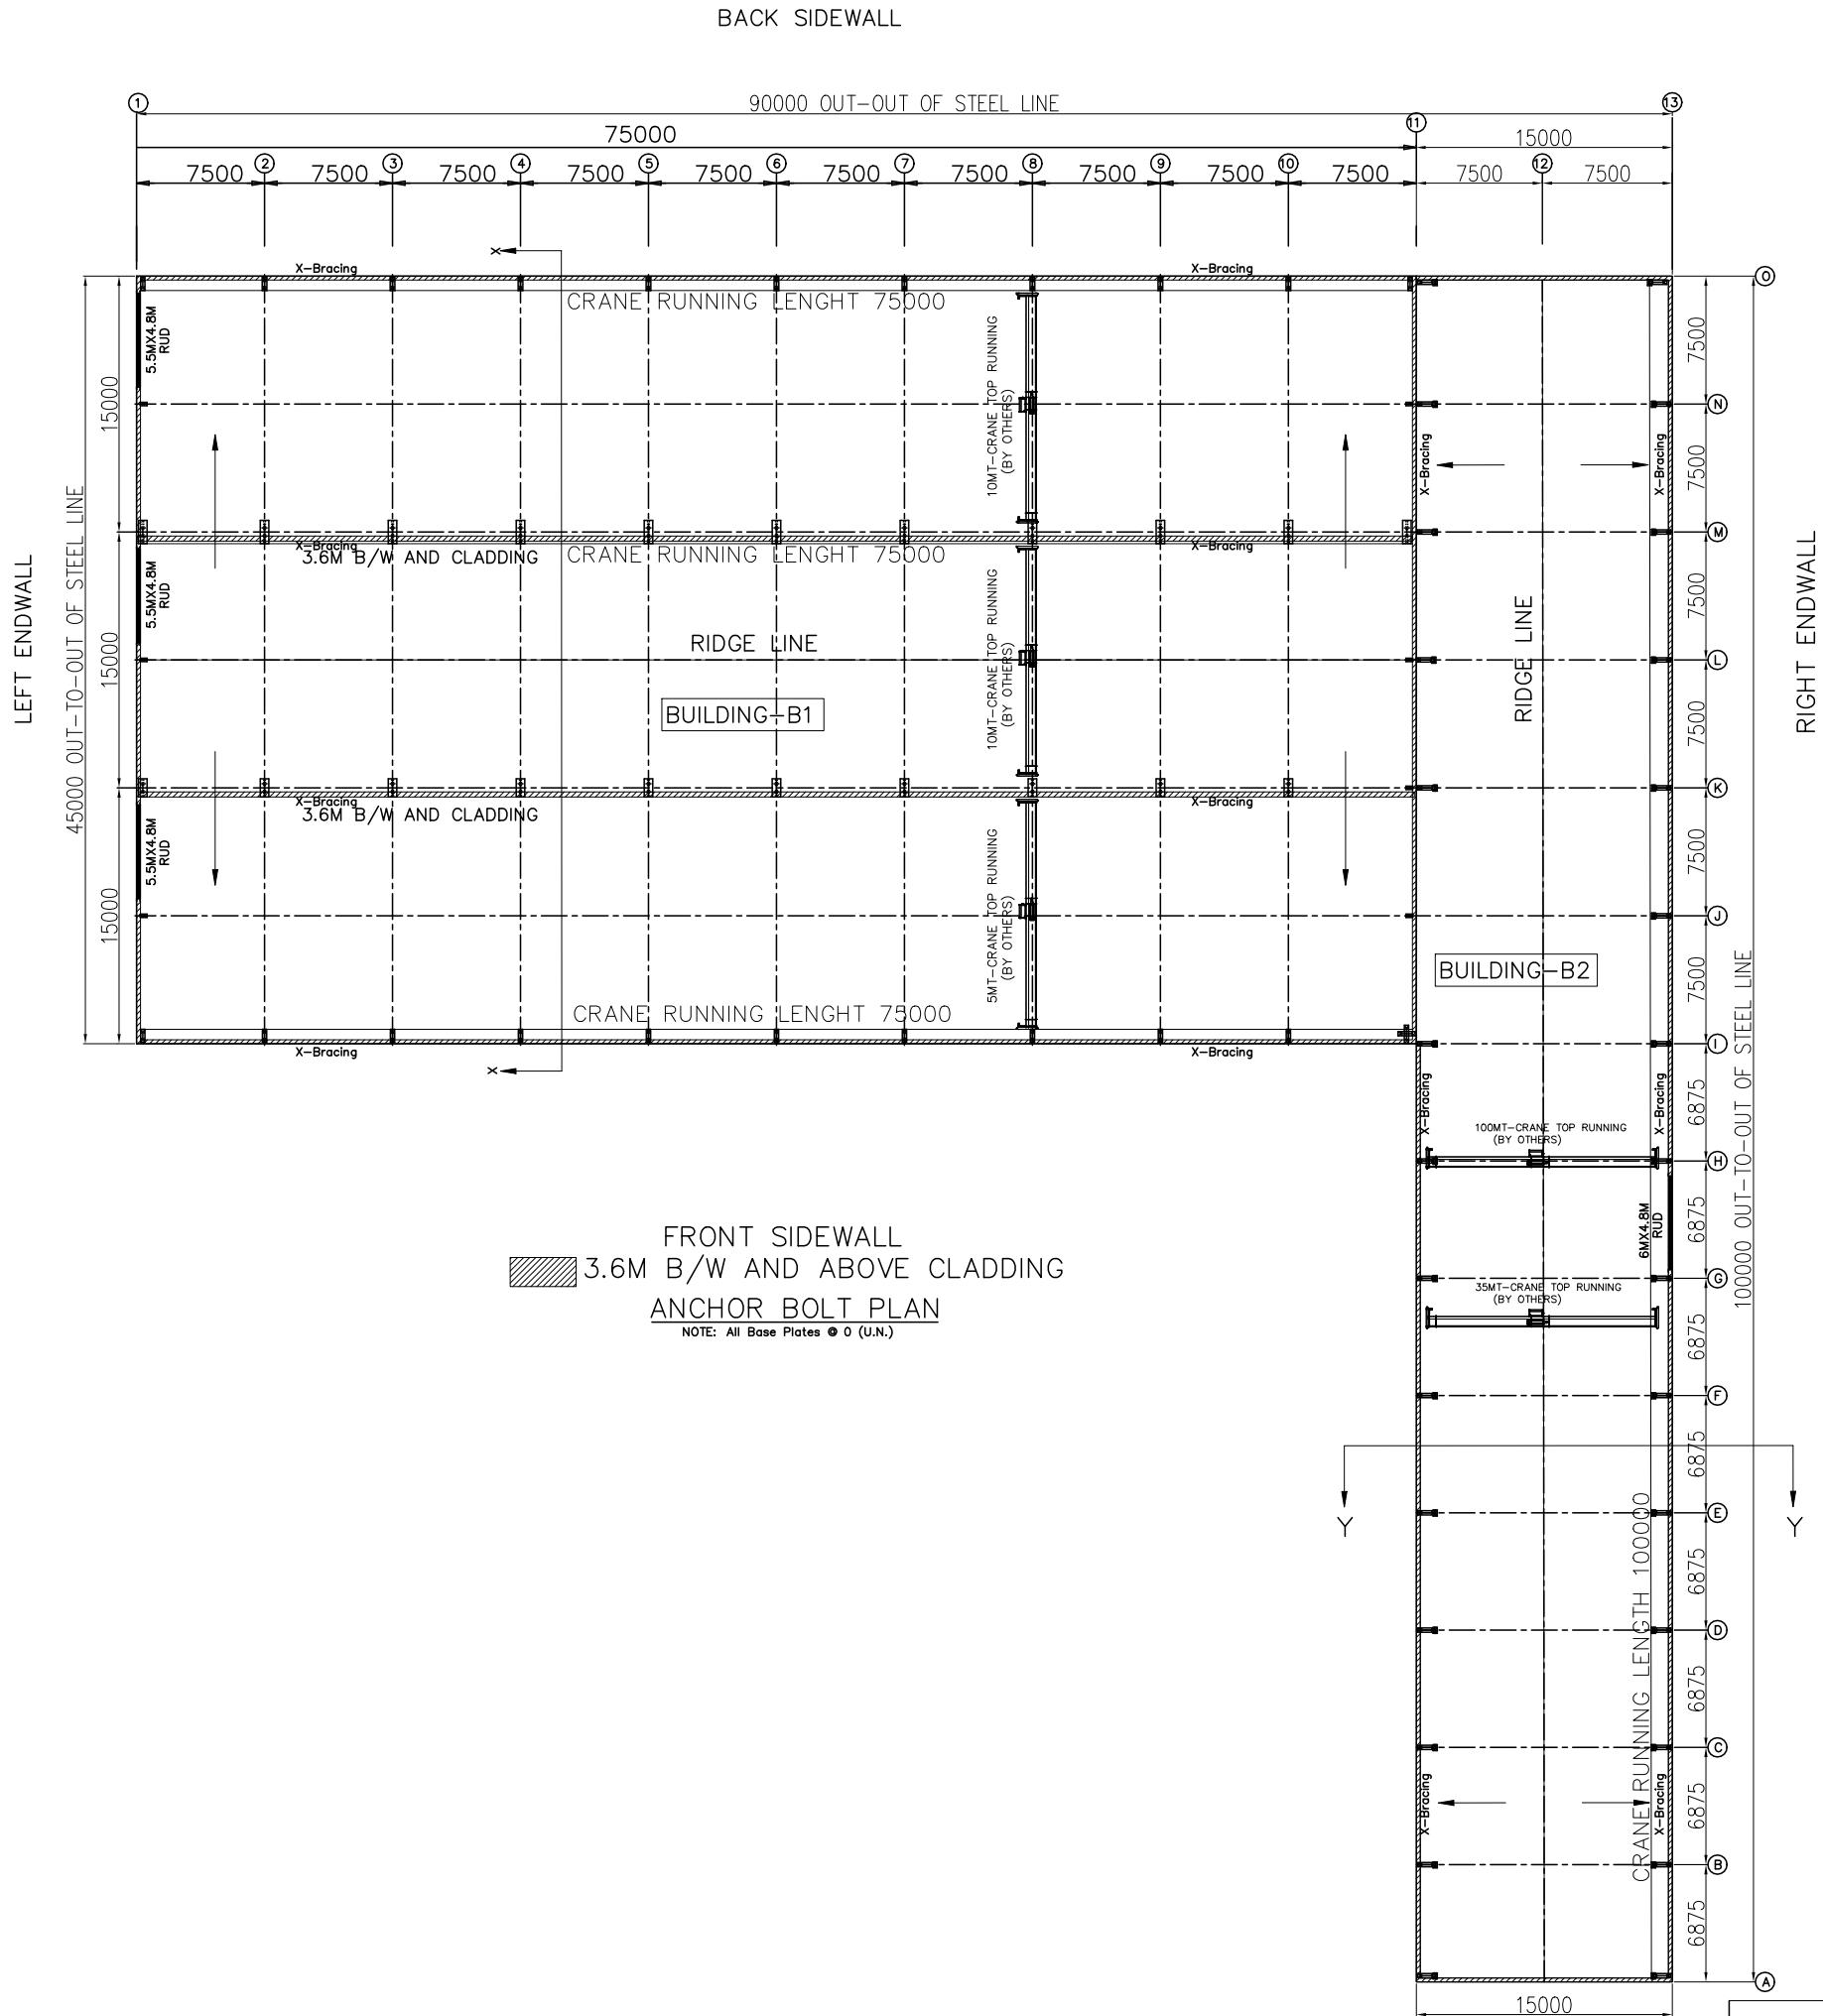

FRONT SIDEWALL
3.6M B/W AND ABOVE CLADDING
ANCHOR BOLT PLAN
NOTE: All Base Plates 0 (U.N.)

INFINITI SOLUTION				
PROJECT	INDUSTRIAL		ANCHOR BOLT PLAN	
ID	C493-012-Raipur		DESIGN: ASB	DRAFT: ASB
PROJECT ADDRESS	Raipur		CHECK: DATE: 13/FEB/2026	