


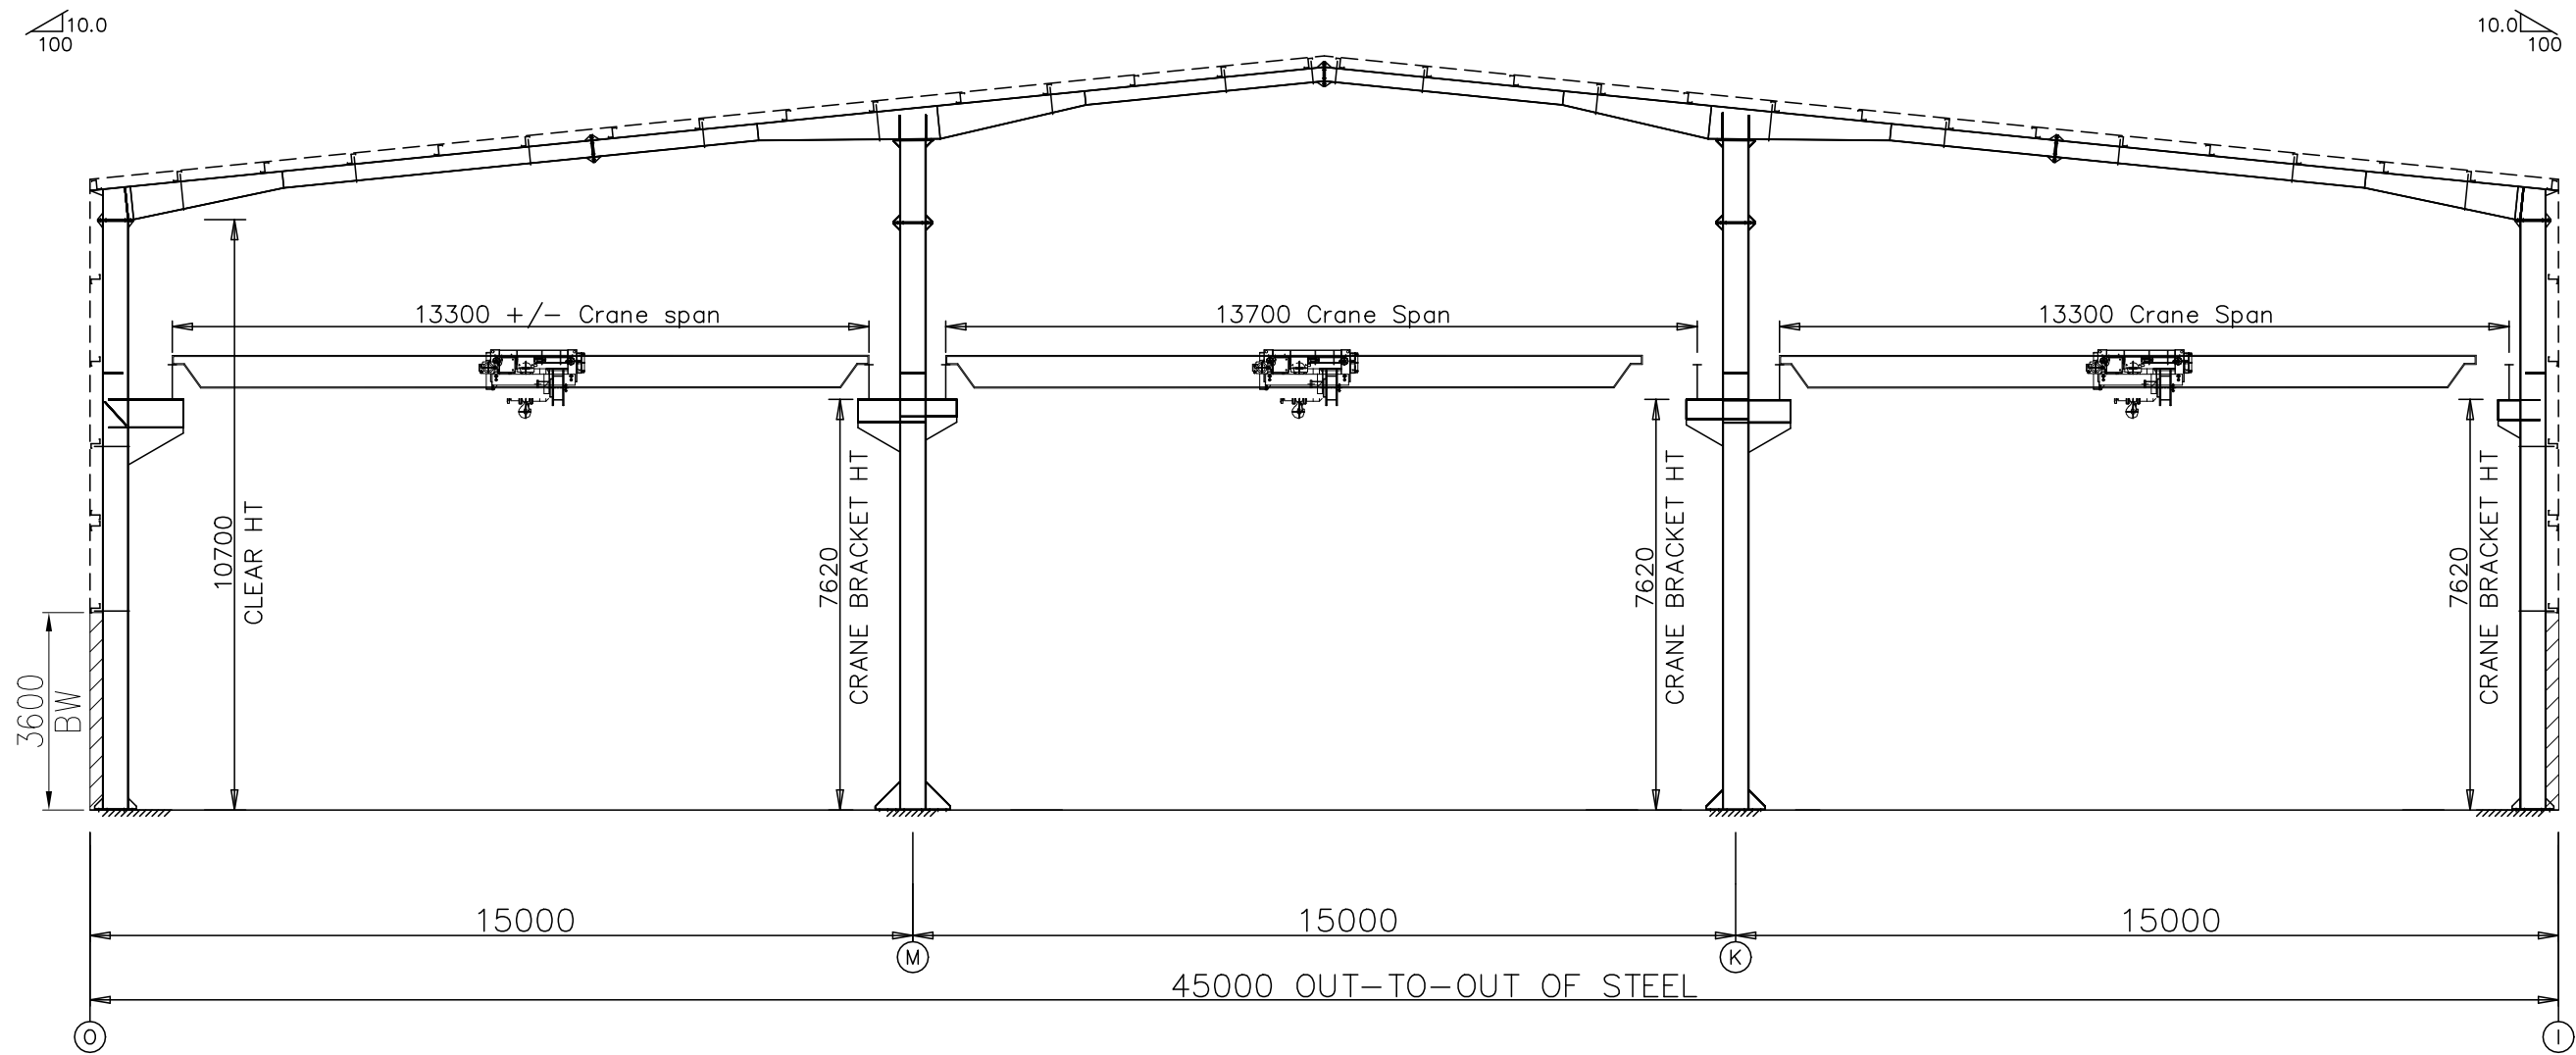

RIGID FRAME ELEVATION: FRAME LINE X-X

INFINITI SOLUTION				
PROJECT	INDUSTRIAL		RIGID FRAME ELEVATION	
ID	C493-012		DESIGN: ASB	DRAFT: ASB CHECK:
PROJECT ADDRESS	Raipur		DATE: 12/FEB/2026	