


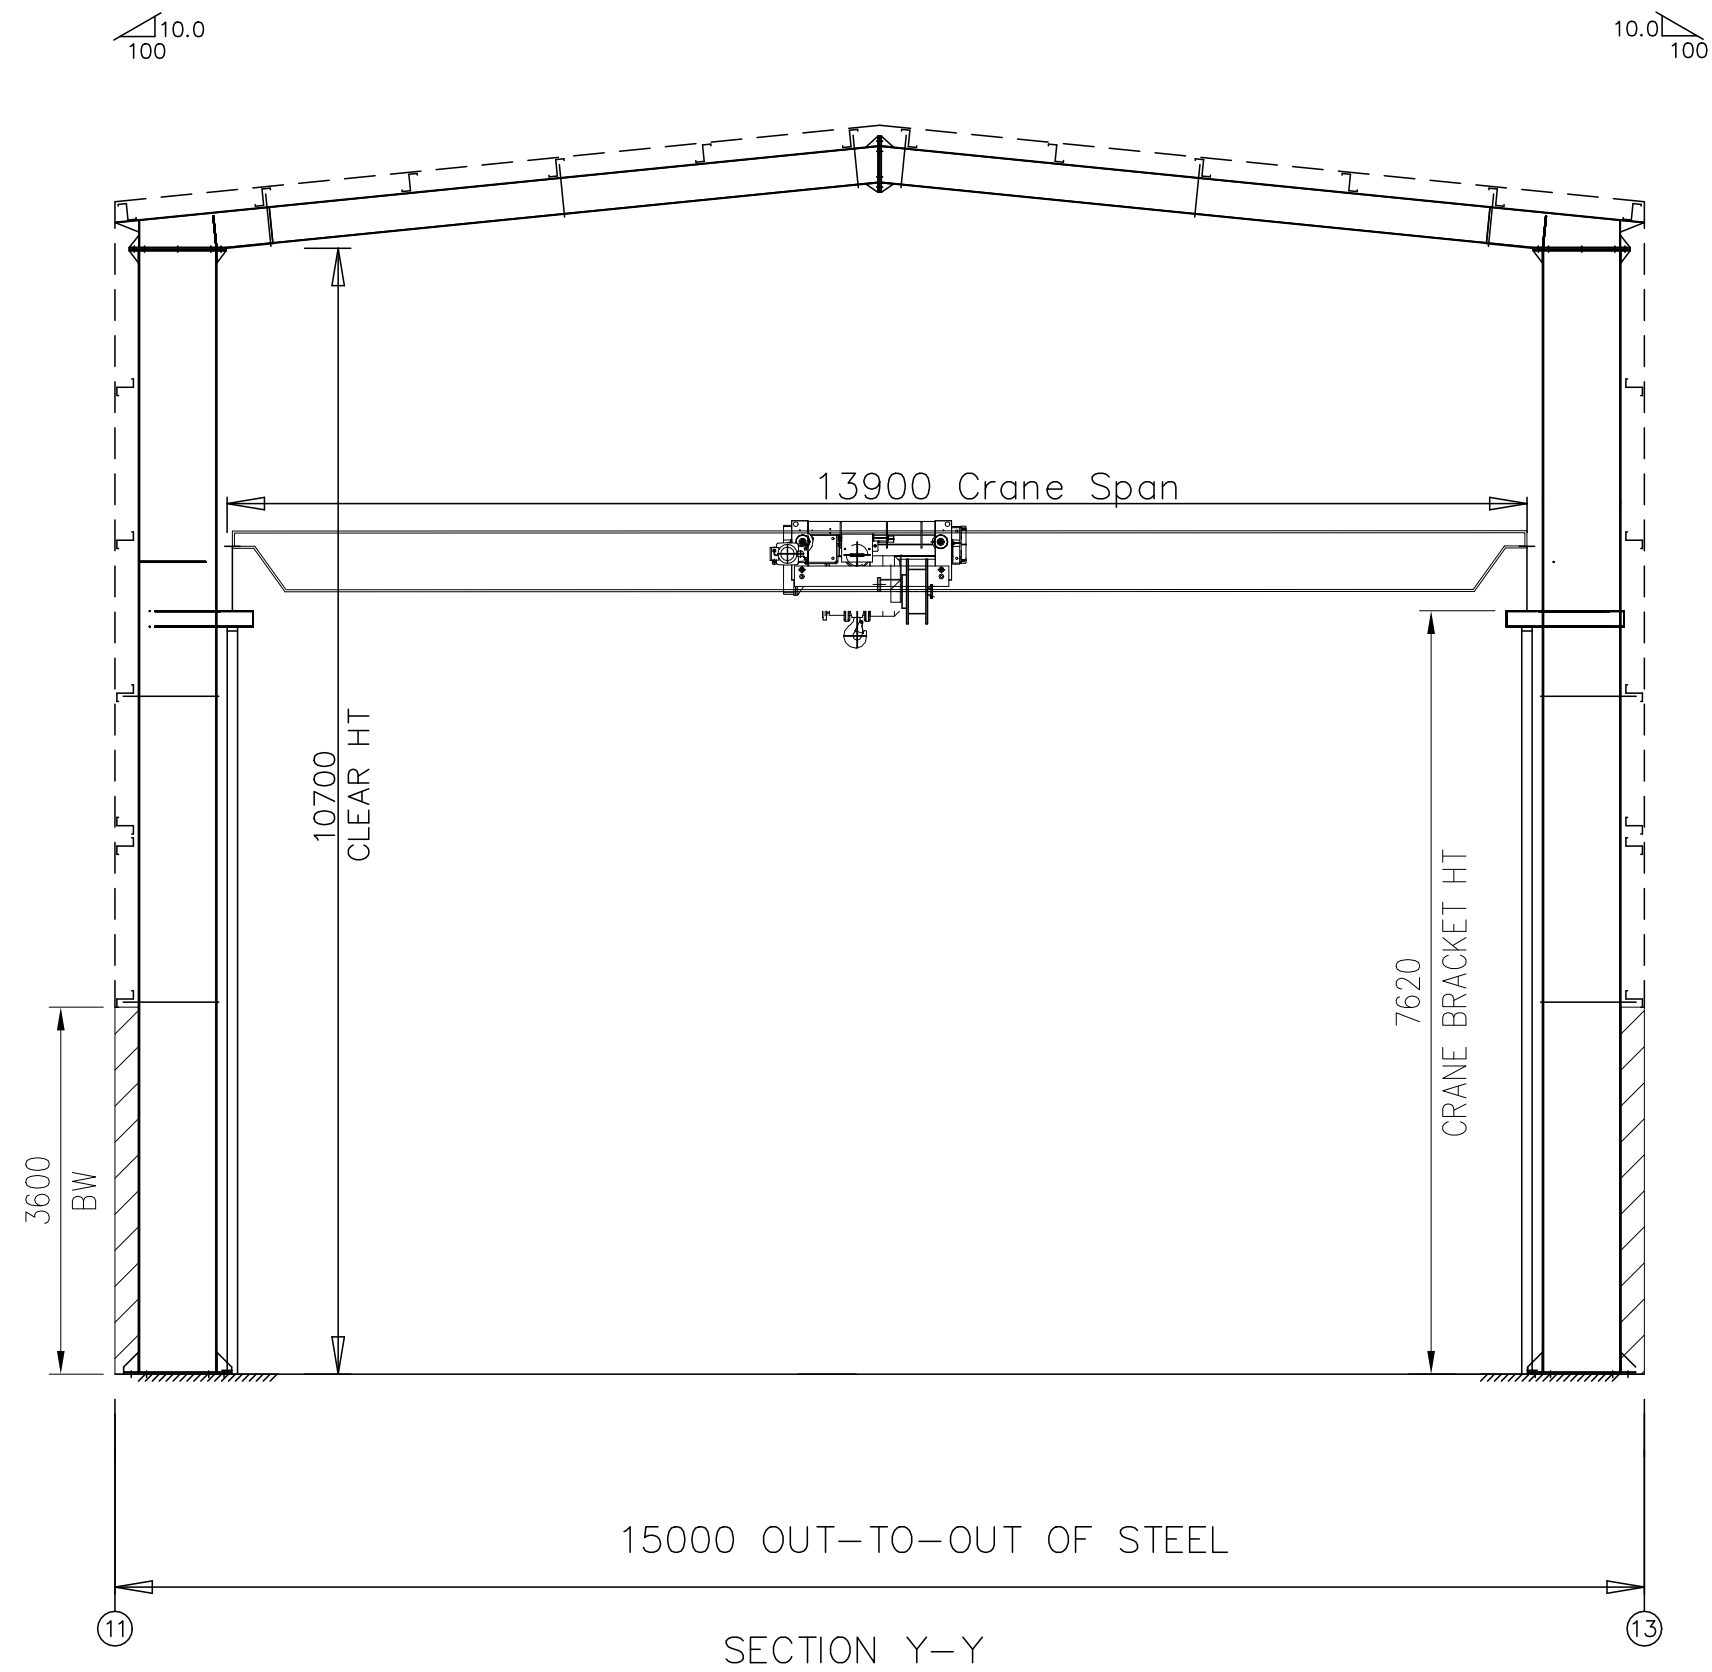

INFINITI SOLUTIONS				
PROJECT	INDUSTRIAL		RIGID FRAME ELEVATION	
ID	111		DESIGN:	DRAFT: CHECK:
PROJECT ADDRESS	Proposed Warehouse		DATE: 12/FEB/2026	