


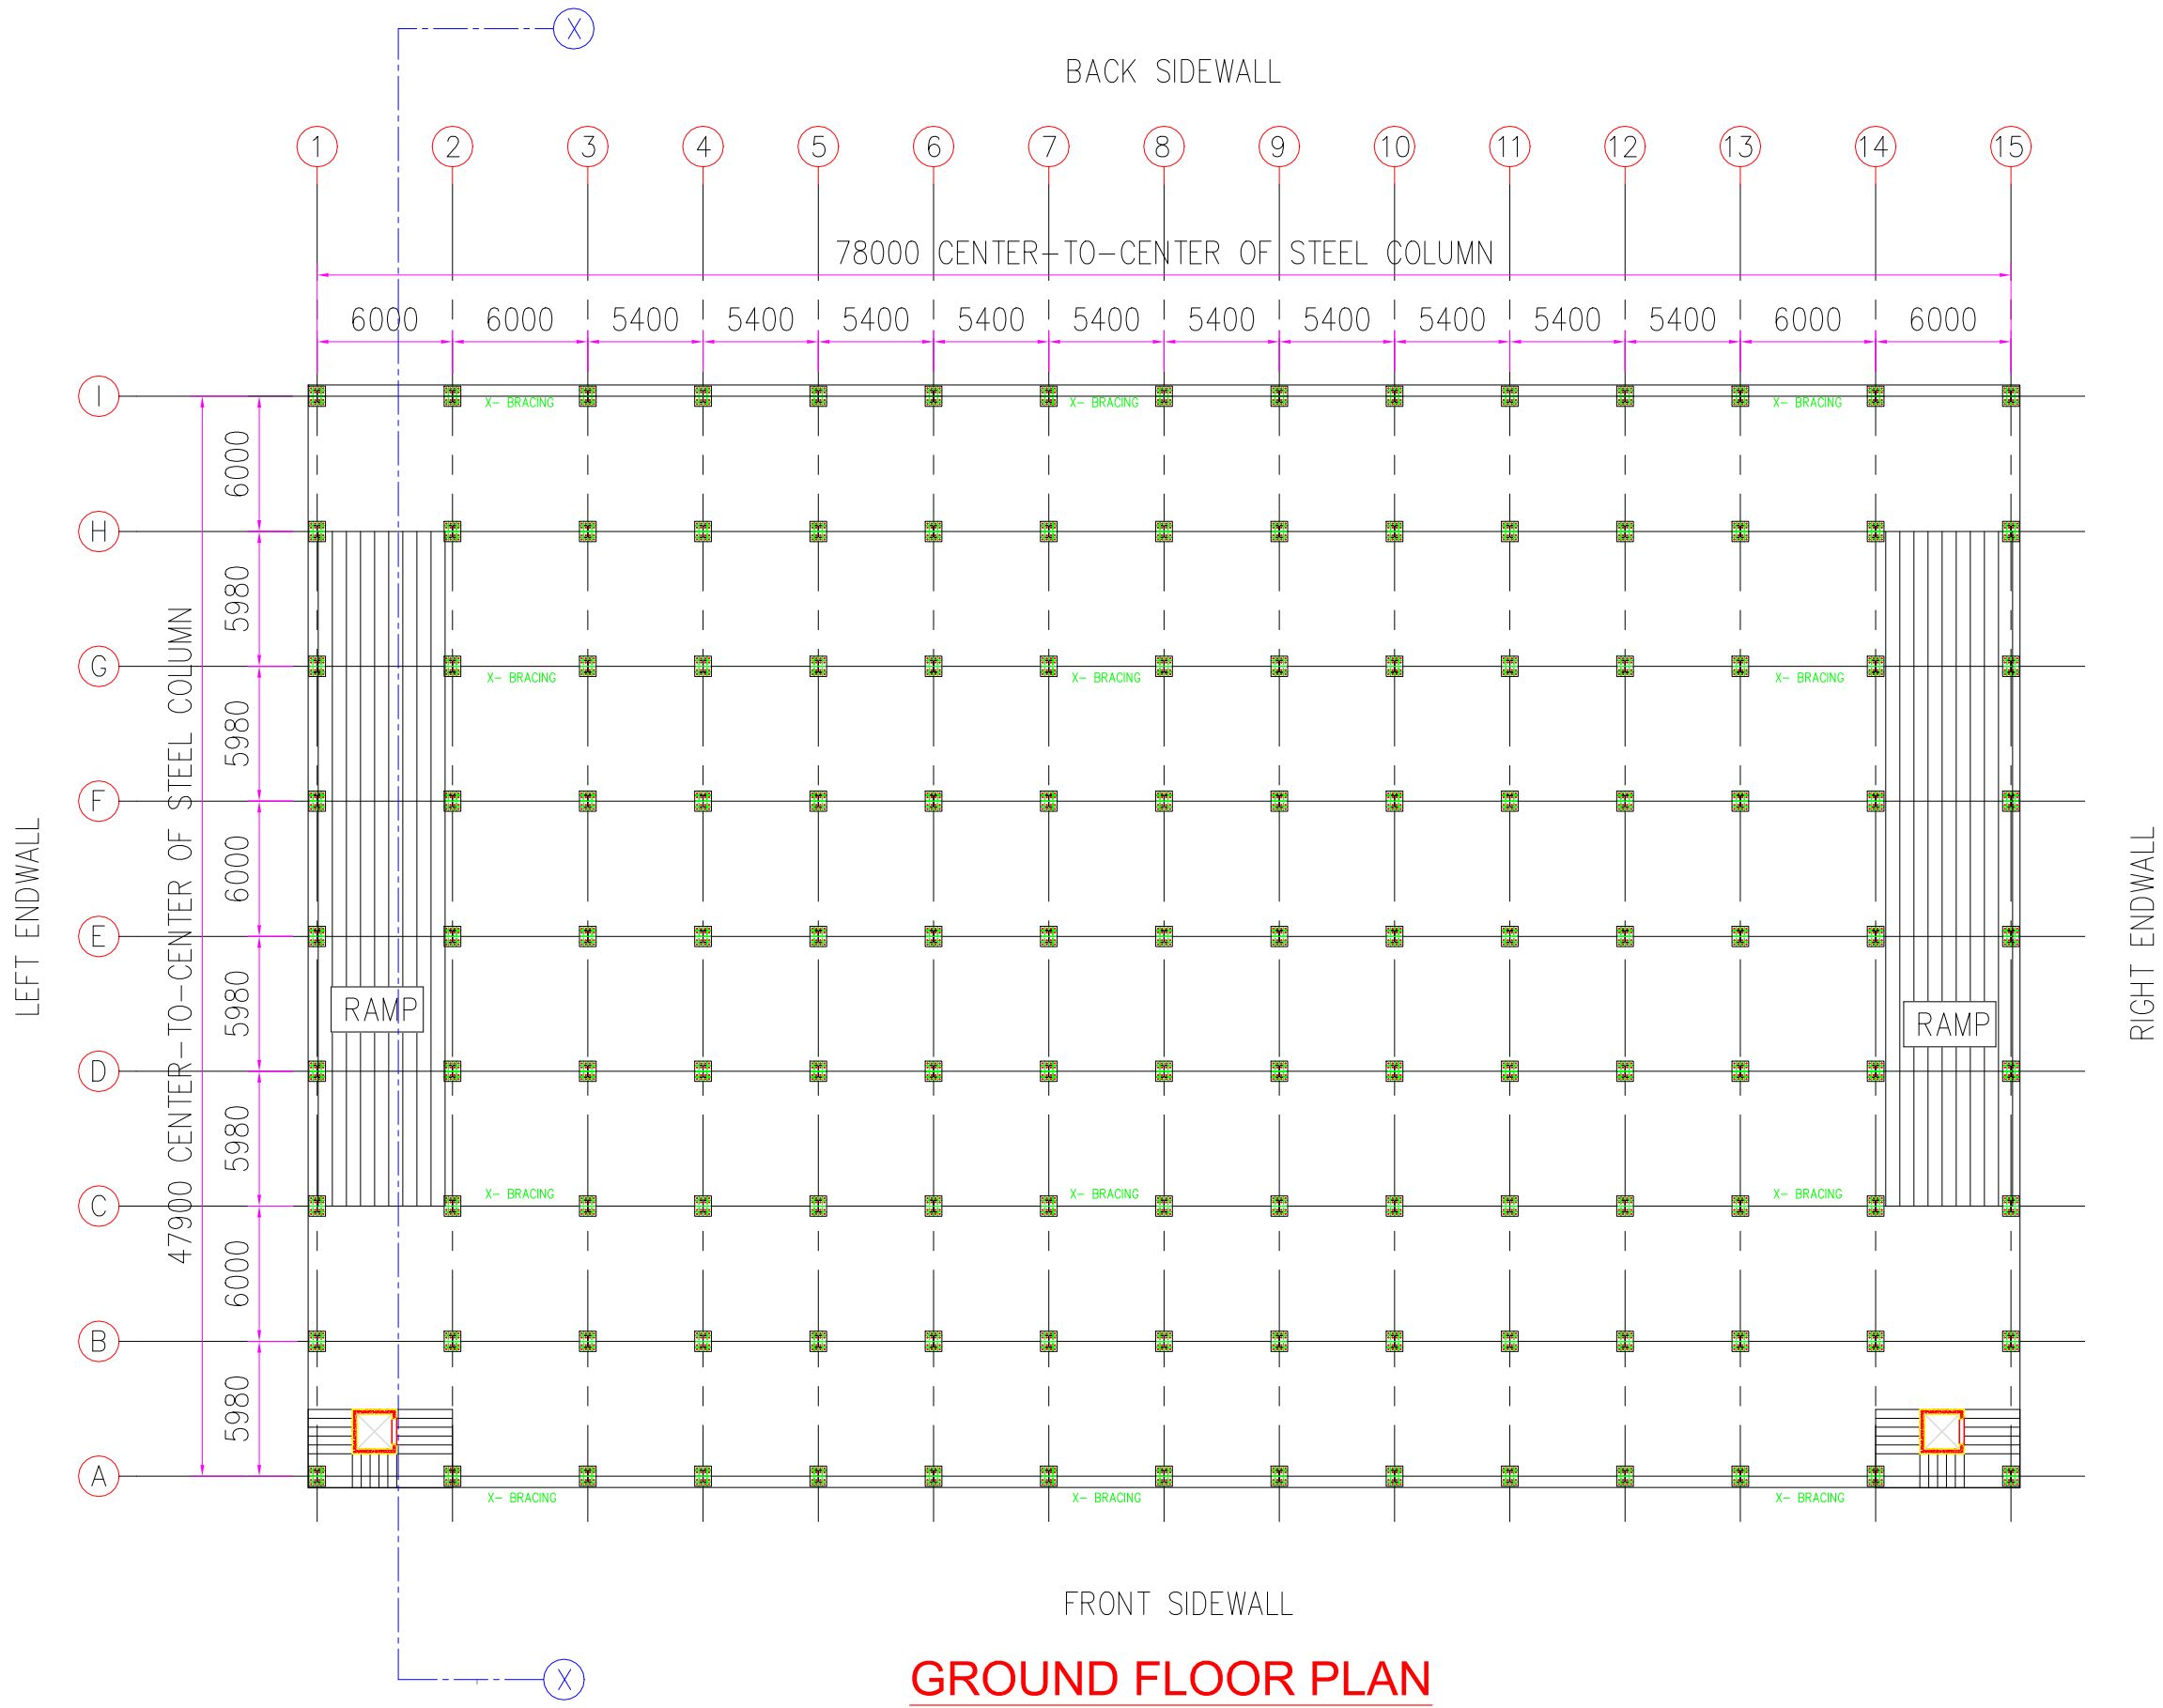

GROUND FLOOR PLAN

NOTE:
1. ALL DIMENSION ARE IN MILLIMETER U.N.O
2. ROOF&WALL SHEETING:0.5mm THK. RAL-9016
FINISH: ALUZINC
ALL DIMENSION LEVEL SHOW IN THE PROPOSAL
DRAWING IS INDICATED ONLY, FINAL DESIGN
DIMENSION LEVEL WILL BE SHOWN IN OUR
APPROVAL DRAWING IN THE DESIGN STAGE

THIS DOCUMENT IS PROPOSAL
DRAWING DATA OF SIVOKO
NOT FOR CONSTRUCTION

00	24.NOV.25	ISSUED FOR PROPOSAL	RSG	RSG	VVJ
NO.	DATE	DESCRIPTION	DSN	DRN	CHK

PROJECT: PARKING STRUCTURE

CLIENT: -

STEEL CONTRACTOR:



P.O. Box CS 8807,
Comm. 7, Tema - Ghana (West Africa)
Tel: +233-0303-910099 / +233-0302-765777
Fax: +233-0303-951408 / +233-0302-765778
Website: www.sivoko.net

MANUFACTURER OF P.E.B, LEAF SPRING, BOLTS
H-BEAM & AXLE

QUOTATION NO.	BUILDING NO.	REVISION NO.	DATE
Q-1392	01	03	24.NOV.2025
DRAWING TITLE:	COLUMN LAYOUT PLAN		DRAWING NO.
			04