


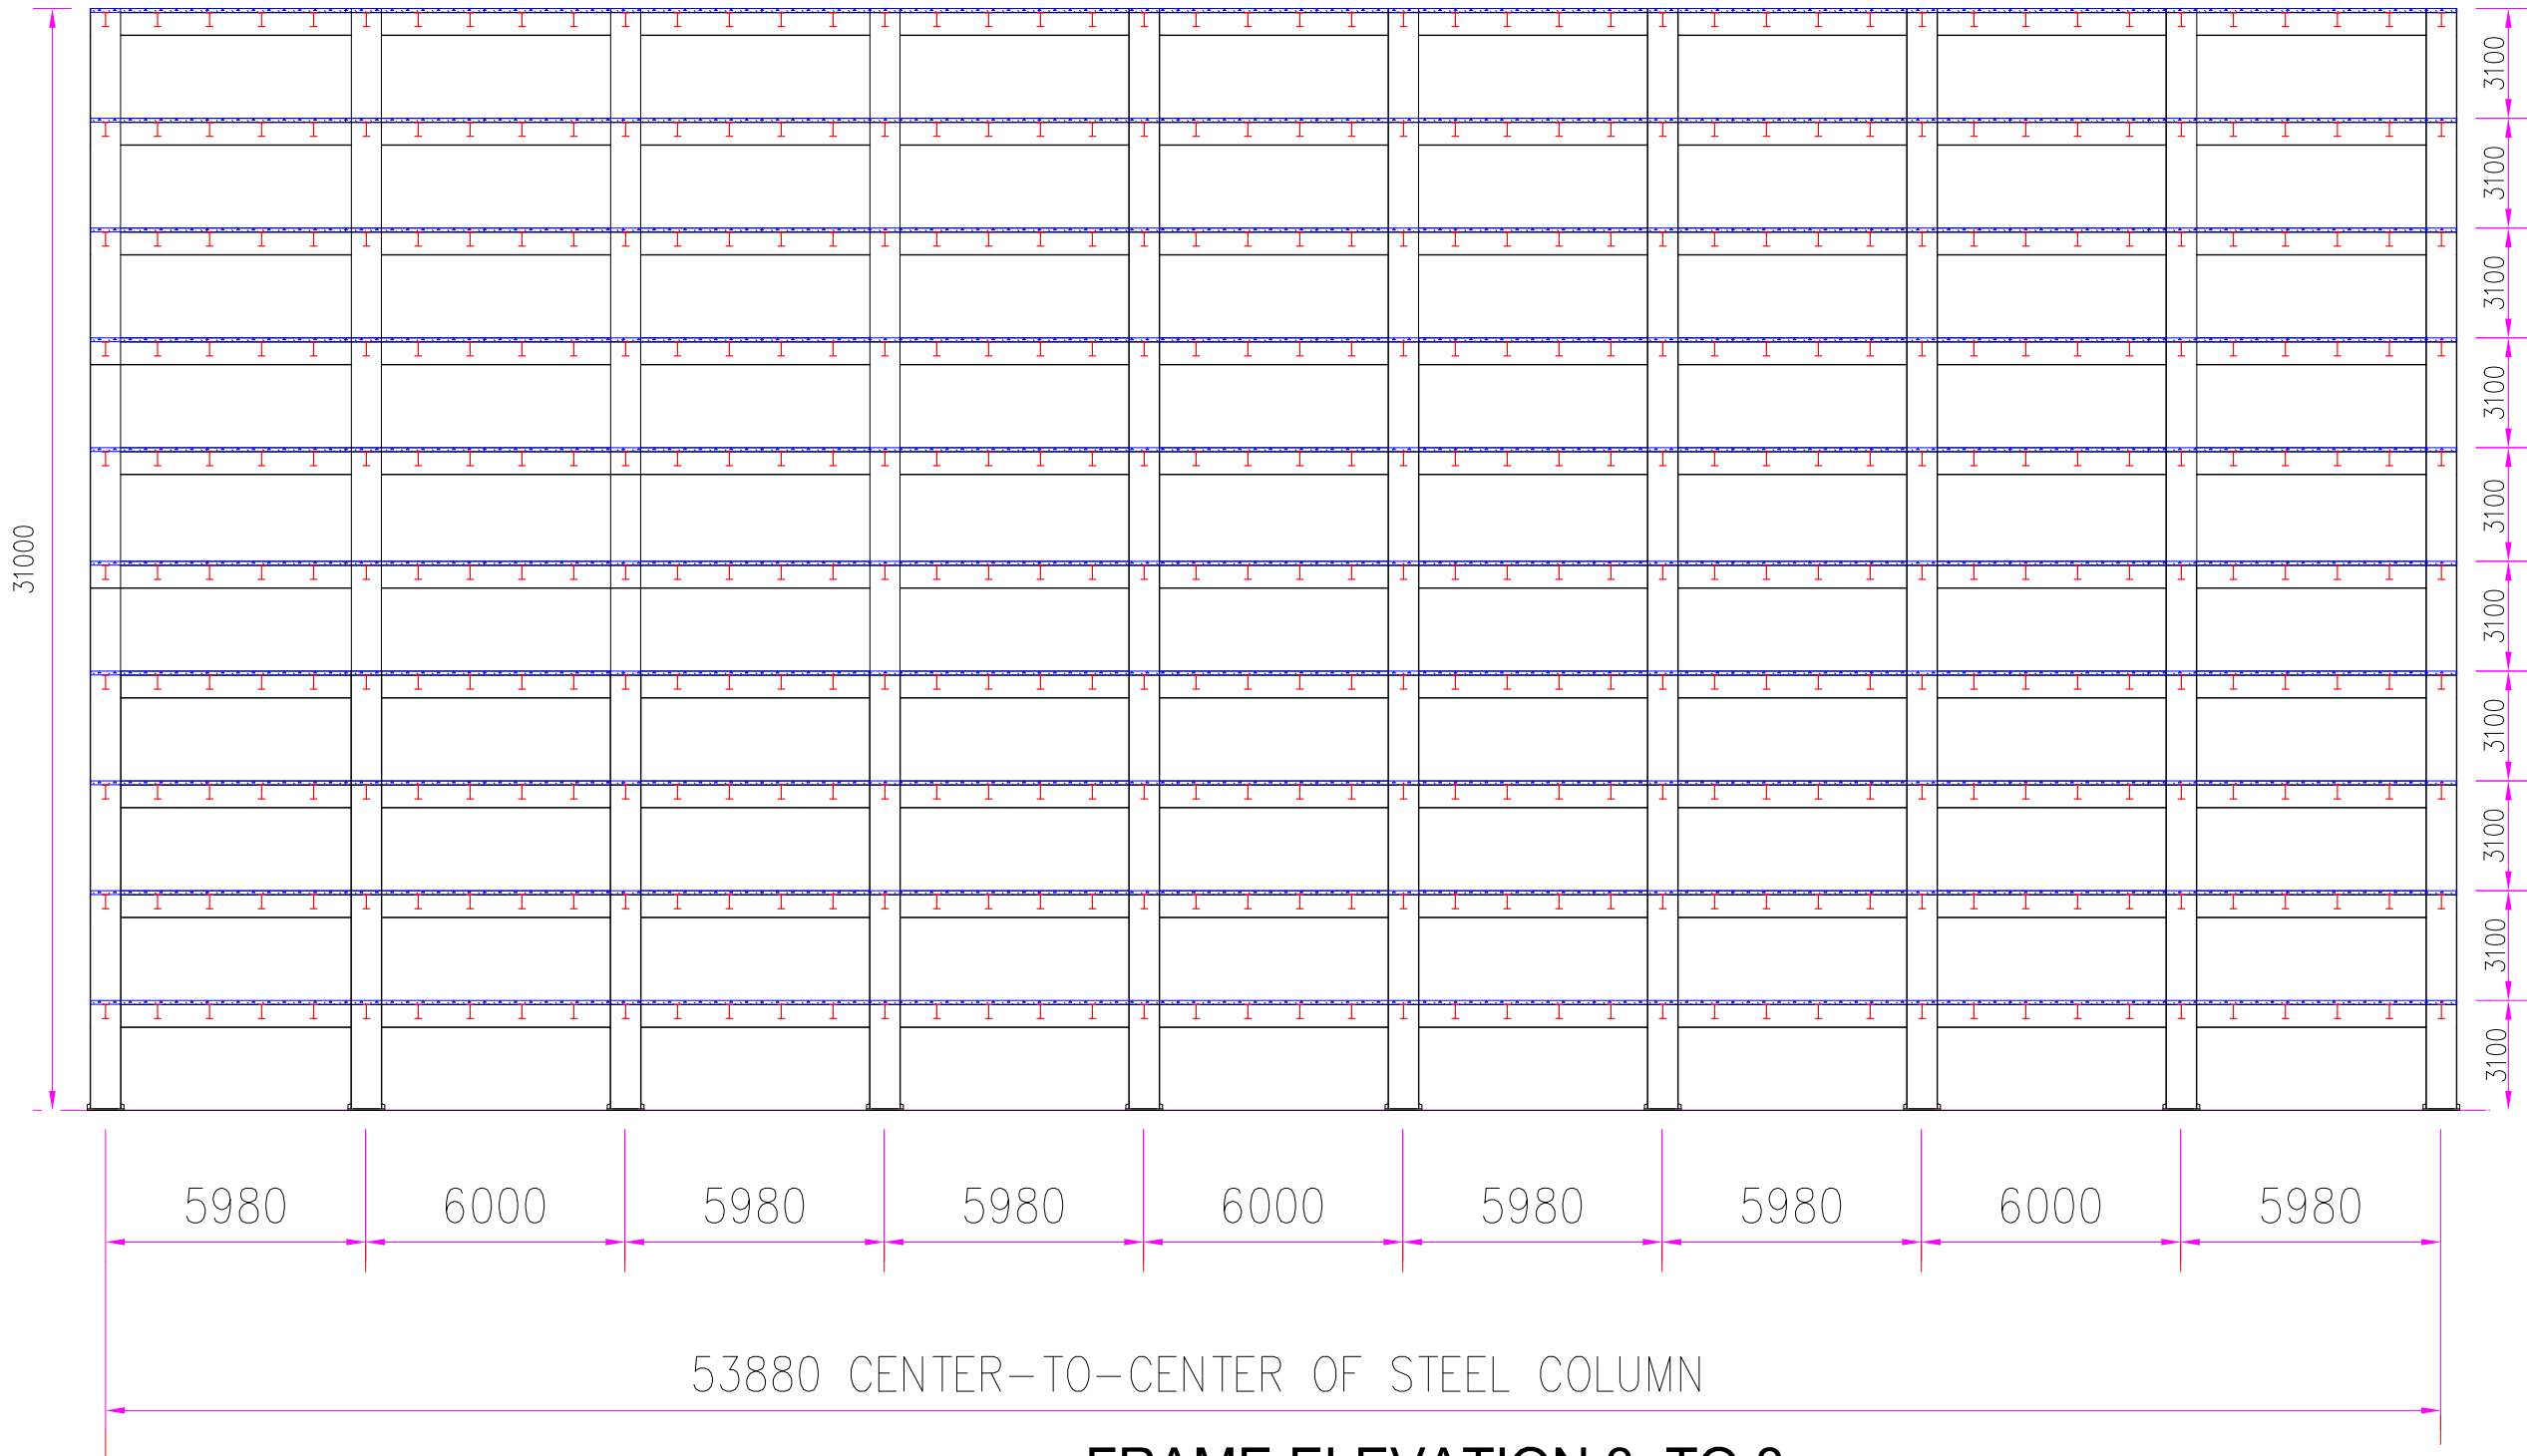

NOTE:

1. ALL DIMENSION ARE IN MILLIMETER U.N.O

2. ROOF&WALL SHEETING:0.5mm THK. RAL-9016

FINISH: ALUZINC

ALL DIMENSION LEVEL SHOW IN THE PROPOSAL

DRAWING IS INDICATED ONLY, FINAL DESIGN

DIMENSION LEVEL WILL BE SHOWN IN OUR

APPROVAL DRAWING IN THE DESIGN STAGE

THIS DOCUMENT IS PROPOSAL

DRAWING DATA OF SIVOKO

NOT FOR CONSTRUCTION

00	24.NVO.25	ISSUED FOR PROPOSAL	RSG	RSG	VVJ
NO.	DATE	DESCRIPTION	DSN	DRN	CHK

PROJECT:

PARKING STRUCTURE

CLIENT:

-

STEEL CONTRACTOR:



P.O. Box CS 8807,
Comm. 7, Tema - Ghana (West Africa)
Tel: +233-0303-910099 / +233-0302-765777
Fax: +233-0303-951408 / +233-0302-765778
Website: www.sivoko.net

MANUFACTURER OF P.E.B, LEAF SPRING, BOLTS
H-BEAM & AXLE

QUOTATION NO.	BUILDING NO.	REVISION NO.	DATE
Q-NNN	01	00	24.NVO.2025
DRAWING TITLE:			DRAWING NO.
FRAME ELEVATION			05