


## OUTLINE SPECIFICATIONS

| |
|---|
| Date          | 13 MAY 2025   | Client   |                   |              |              |                                       |     |     |     |           |      |                                   | Project Location                                 | Ghana                                         | |
| Proposal Id   | Q-1392   | Project   | Parking Structure |              |              |                                       |     |     |     |           |      |                                   | Building No.                                     | 1                                             | Option | 1                 | Revision            | 1               | |
| Sr.No.        | Description   | PEB SPECIFICATIONS   | |
| 1.            | Building type   | Mezzanine Building   |                   |              |              |                                       |     |     |     |           |      | Area in m²                        |                                                  | 4047                                          | |
| 2.            | Length in m (c/c of steel)   | 75.1   |                   |              |              |                                       |     |     |     |           |      | Length wise bay spacing           |                                                  | 2@6.0+10@5.11+2@6.0                           | |
| 3.            | Width in m (c/c of steel)   | 53.88   |                   |              |              |                                       |     |     |     |           |      | End wall column spacing           |                                                  | 1@5.89+1@6.0+2@5.89+1@6.0+2@5.89+1@6.0+1@5.89 | |
| 4.            | Width modules in m   | Ref.Dwg   |                   |              |              |                                       |     |     |     |           |      | No. of interior columns per frame |                                                  | 0                                             | |
| 5.            | Clear height in m   | Ref.Dwg   |                   |              |              |                                       |     |     |     |           |      | Frames symmetrical                |                                                  | Yes                                           | |
| 6.            | Roof   | Slope: 10:100   |                   |              | Cladding: NA |                                       |     |     |     |           |      |                                   | Rainwater drainage: Eave Gutters and Down spouts | |
| 7.            | Future Expansion   | NA   | |
| 8.            | Block Wall   | NA   | |
| 9.            | Column base elevations   | NA (At FFL)   | |
| 10.           | Wall Cladding   | NA   | |
| 11.           | Insulation   | Roof: NA   |                   |              |              |                                       |     |     |     |           |      | Outer Walls: NA                   |                                                  |                                               |        |                   | Partition walls: NA | |
| 12.           | Openings   | <table><tr><td>Outer side only</td><td colspan="10">Numbers</td><td colspan="3">Type</td><td colspan="3">Size in m (w x h)</td></tr><tr><td>Doors</td><td colspan="10">NA</td><td colspan="3">NA</td><td colspan="3">NA</td></tr><tr><td>Windows</td><td colspan="10">NA</td><td colspan="3">NA</td><td colspan="3">NA</td></tr></table> |                   |              |              |                                       |     |     |     |           |      |                                   |                                                  |                                               |        |                   |                     | Outer side only | Numbers |               |  |  |  |  |  |  |  |  | Type |  |  | Size in m (w x h) |  |  | Doors | NA |  |  |  |  |  |  |  |  |  | NA |  |  | NA |  |  | Windows | NA |  |  |  |  |  |  |  |  |  | NA |  |  | NA |  |  |
|               |   | Outer side only   | Numbers           |              |              |                                       |     |     |     |           |      |                                   | Type                                             |                                               |        | Size in m (w x h) | |
|               |   | Doors   | NA                |              |              |                                       |     |     |     |           |      |                                   | NA                                               |                                               |        | NA                | |
|               |   | Windows   | NA                |              |              |                                       |     |     |     |           |      |                                   | NA                                               |                                               |        | NA                | |
|               |   | Location of doors & bracing   | |
|               |   | Side Wall Gridlines   | 1-2               | 2-3          | 3-4          | 4-5                                   | 5-6 | 6-7 | 7-8 | 8-9       | 9-10 | 10-11                             | 11-12                                            | 12-13                                         | 13-14  | 14-15             | 15-16               | Right End Wall  | |
|               |   | Front Side Wall   |                   | XP           |              |                                       |     | XP  |     |           |      | XP                                |                                                  |                                               |        | XP                | |
|               |   | Back Side Wall   |                   | XP           |              |                                       |     | XP  |     |           |      | XP                                |                                                  |                                               |        | XP                | |
|               |   | End Wall Axes   |                   | A-B          | B-C          | C-D                                   | D-E | E-F | F-G | G-H       | H-I  | I-J                               | Back Side Wall                                   | |
|               |   | Right End Wall   | |
| Left End Wall | |
| 13.           | Extensions   | Eave: NA   | Gable: NA         | Canopies: NA |              |                                       |     |     |     |           |      |                                   |                                                  |                                               |        |                   | Parapet: NA         | |
| 14.           | Accessories   | Wall Lights:   |                   | NA           |              |                                       |     |     |     |           |      |                                   |                                                  |                                               |        |                   | Roof Monitor        |                 | NA      | Any other: NA | |
|               |   | Skylights:   |                   | NA           |              |                                       |     |     |     |           |      |                                   |                                                  |                                               |        |                   | Cage ladder         |                 | NA      | |
|               |   | Turbo Ventilators:   |                   | NA           |              |                                       |     |     |     |           |      |                                   |                                                  |                                               |        |                   | Ridge Ventilators:  |                 | NA      | |
| 15.           | For Frames<br>(Standard codes and manuals used in design - 2010 Metal Building Systems Manual, NAUS07, AISC05, UBC 1997)<br>Design Software: MBS | DESIGN LOADS   |                   |              |              | LOCATION - CLIMATIC DATA              |     |     |     |           |      | SERVICEBILITY CRITERIA            | |
|               |   | Dead Load in kN/m²   |                   | 0.10         |              | Max wind speed in m/s                 |     |     |     | 36.11     |      | Frames                            |                                                  | H/100, L/150                                  | |
|               |   | Live Load in kN/m²   |                   | 0.575        |              | Exposure category                     |     |     |     | B         |      | Purlins                           |                                                  | Span/150                                      | |
|               |   | Collateral load in kN/m²   |                   | 0.05         |              | Max rainfall intensity in mm/hr.      |     |     |     | 150       |      | Girts                             |                                                  | Span/120                                      | |
|               |   | Any other   |                   | NA           |              | Seismic Design category (Coefficient) |     |     |     | II (0.33) |      | Crane Beams                       |                                                  | Span/600                                      | |
|               |   |   |                   |              |              | Max Temperature variation in °C       |     |     |     | 20        |      | Mezzanine Beams                   |                                                  | Span/240                                      | |



|     |                       |   |   |   |
|-----|-----------------------|---|---|---|
| 16. | Mezzanine             | <b>Location:</b> Ref.Dwg.<br><b>Loading:</b><br>Live load in kN/m <sup>2</sup> : 7.5<br>Dead load in kN/m <sup>2</sup> : 3.75<br>Collateral load in kN/m <sup>2</sup> : 0   | <b>Dimensions:</b><br>Length in m: Ref.Dwg.<br>Width in m: Ref.Dwg.<br>Top of the Mezzanine Floor in m: Ref.Dwg.<br>Depth of mezzanine slab in mm: 150<br>Deck sheeting thickness: 0.7mm | <b>Accessories:</b> <i>Staircase</i><br>Nos.: 2<br>Location: Ref.Dwg.<br>Type: <i>Double staircase with intermediate landing</i><br>Handrail: <i>All round</i> |
| 17. | Partition Walls       | NA   |   |   |
| 18. | Jack Beam             | NA   |   |   |
| 19. | Assumptions & Remarks | <p><i>Built-up sections are made from hot rolled plates conforming to ASTM A-572 Gr50 (345MPa) steel.</i></p> <p><i>The plates are joined together with double side welding. Sections consist of minimum 5mm for flange &amp; minimum 4mm for web thickness.</i></p> <p><i>Cold formed sections thickness 1.5 mm or more are made of hot rolled sheet of Gr50 (345 MPa) steel.</i></p> <p><i>Primary structural connections are high strength machine bolts conforming to ASTM A325 or equivalent.</i></p> <p><i>Sheeting profile considered is of 1 m standard width, formed from a coil of 1.220 m. Single colour sheeting of up to maximum 9 m lengths is considered.</i></p> <p><b>Not considered in scope:</b> <i>Foundation, Block wall (Civil work). Crane Bridge, Trolley, Rail and its installation.</i></p> |   |   |

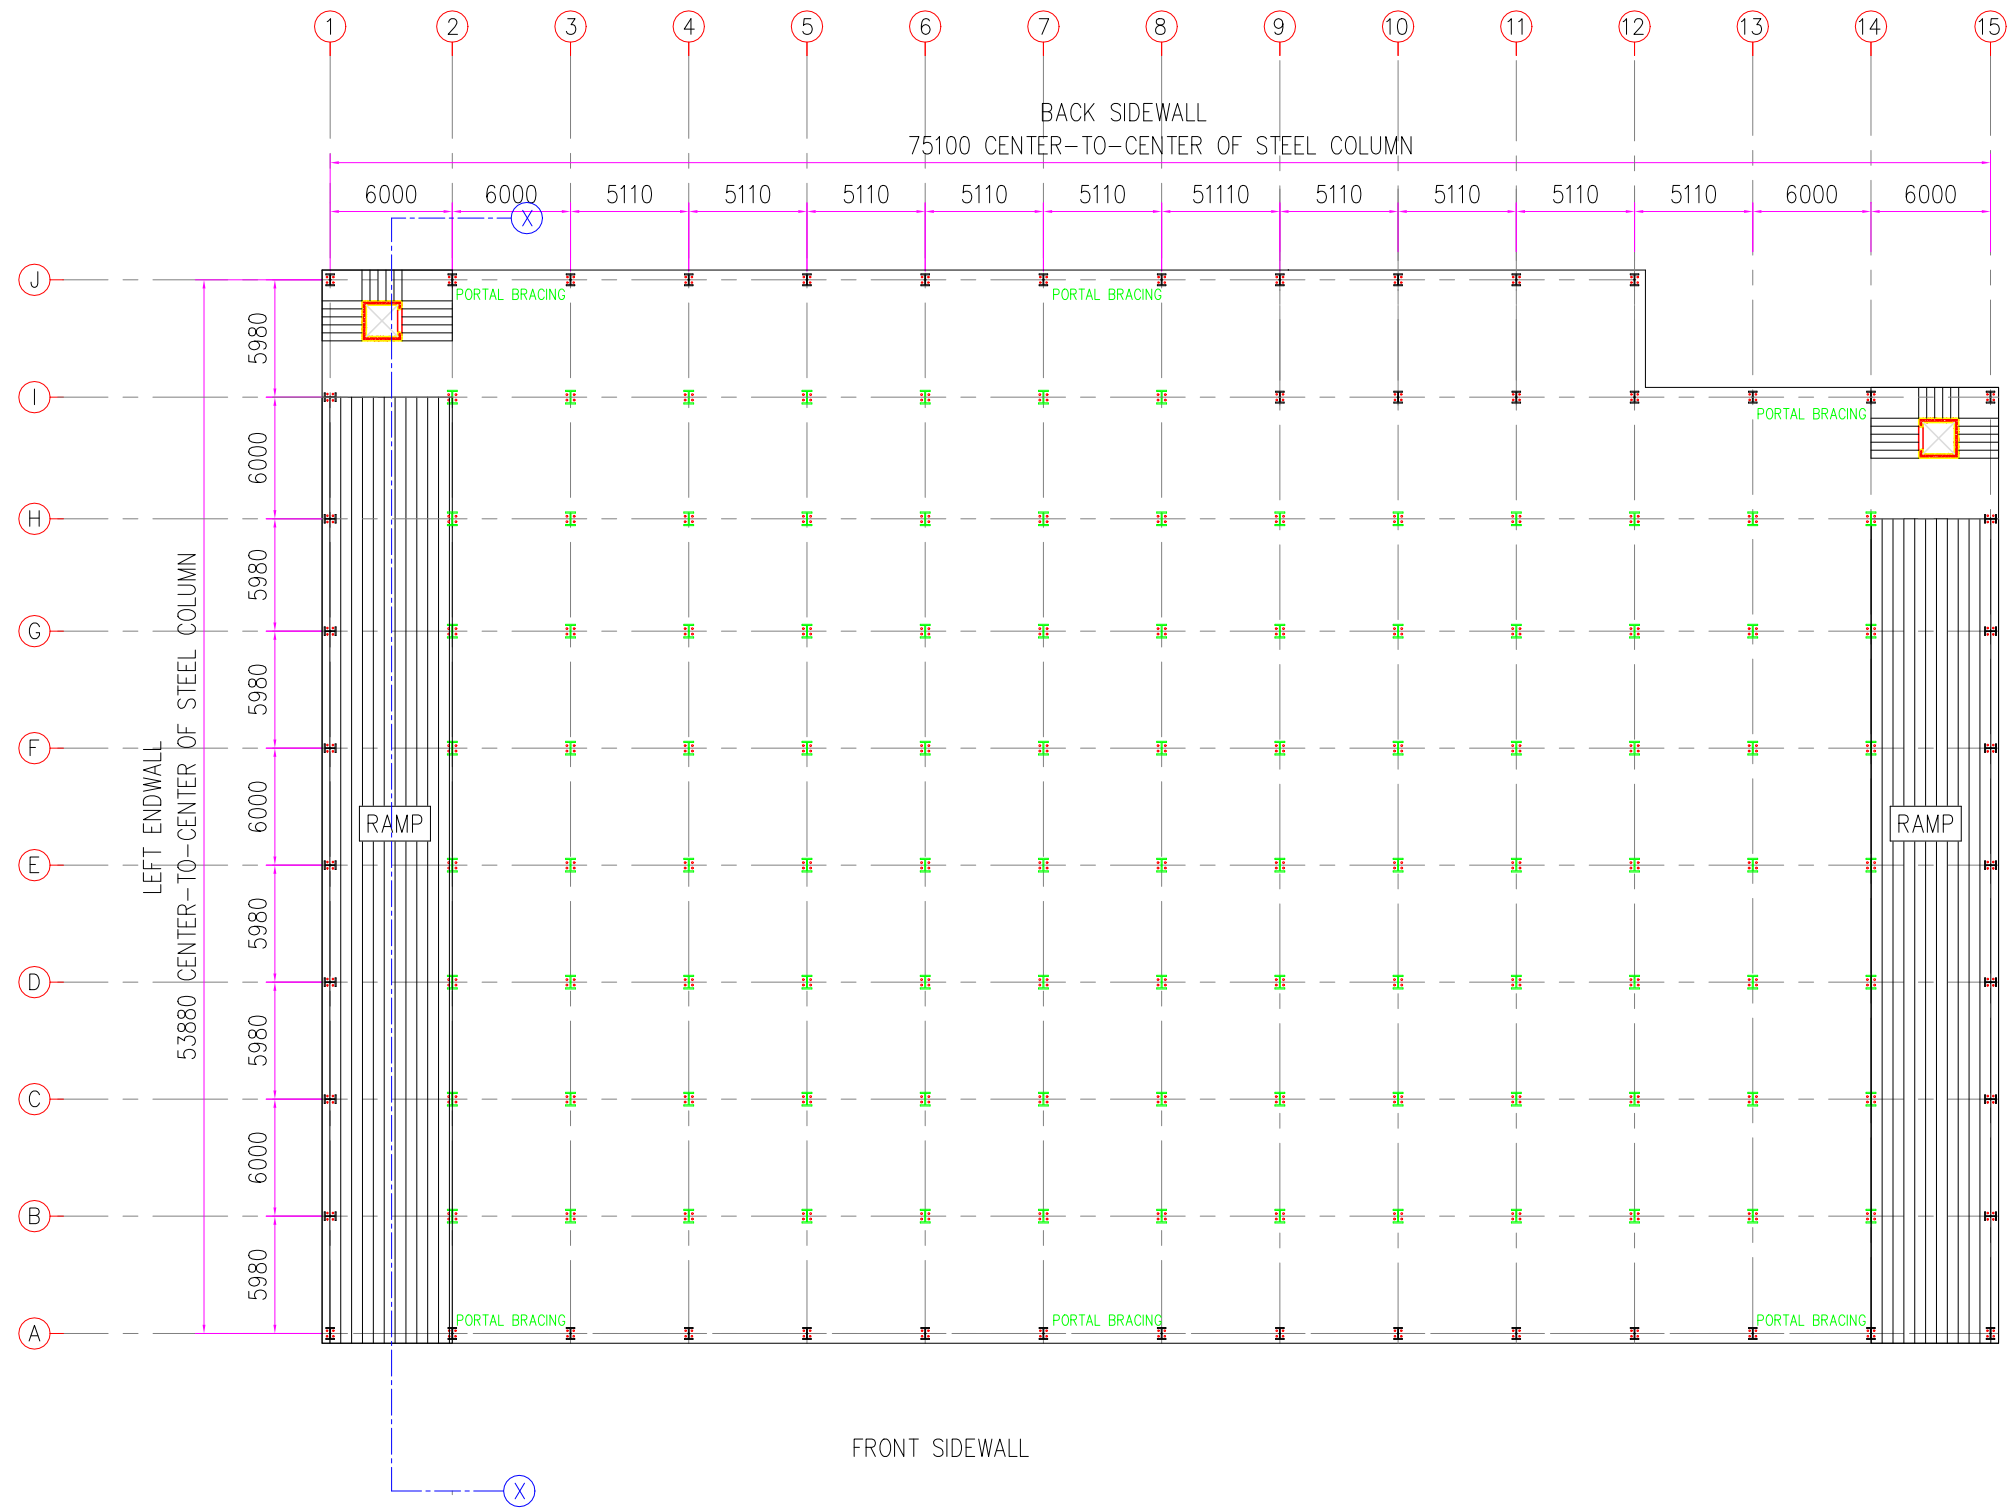

GROUND FLOOR PLAN

**NOTE:**

1. ALL DIMENSION ARE IN MILLIMETER U.N.O

2. ROOF&WALL SHEETING:0.5mm THK. RAL-9016

FINISH: ALUZINC

ALL DIMENSION LEVEL SHOW IN THE PROPOSAL  
DRAWING IS INDICATED ONLY, FINAL DESIGN  
DIMENSION LEVEL WILL BE SHOWN IN OUR  
APPROVAL DRAWING IN THE DESIGN STAGE

THIS DOCUMENT IS PROPOSAL  
DRAWING DATA OF SIVOKO  
NOT FOR CONSTRUCTION

|     |             |                     |     |     |     |
|-----|-------------|---------------------|-----|-----|-----|
| 00  | 06.AUG.2021 | ISSUED FOR PROPOSAL | RSG | RSG | VVJ |
| NO. | DATE        | DESCRIPTION         | DSN | DRN | CHK |

PROJECT: PARKING STRUCTURE

CLIENT: -


STEEL CONTRACTOR:



P.O. Box CS 8807,  
Comm. 7, Tema - Ghana (West Africa)  
Tel: +233-0303-910099 / +233-0302-765777  
Fax: +233-0303-951408 / +233-0302-765778  
Website: www.sivoko.net

MANUFACTURER OF P.E.B, LEAF SPRING, BOLTS  
H-BEAM & AXLE

|                                      |                    |                    |                     |
|--------------------------------------|--------------------|--------------------|---------------------|
| QUOTATION NO.<br>Q-1392              | BUILDING NO.<br>01 | REVISION NO.<br>00 | DATE<br>07.MAY.2025 |
| DRAWING TITLE:<br>COLUMN LAYOUT PLAN |                    |                    | DRAWING NO.<br>04   |

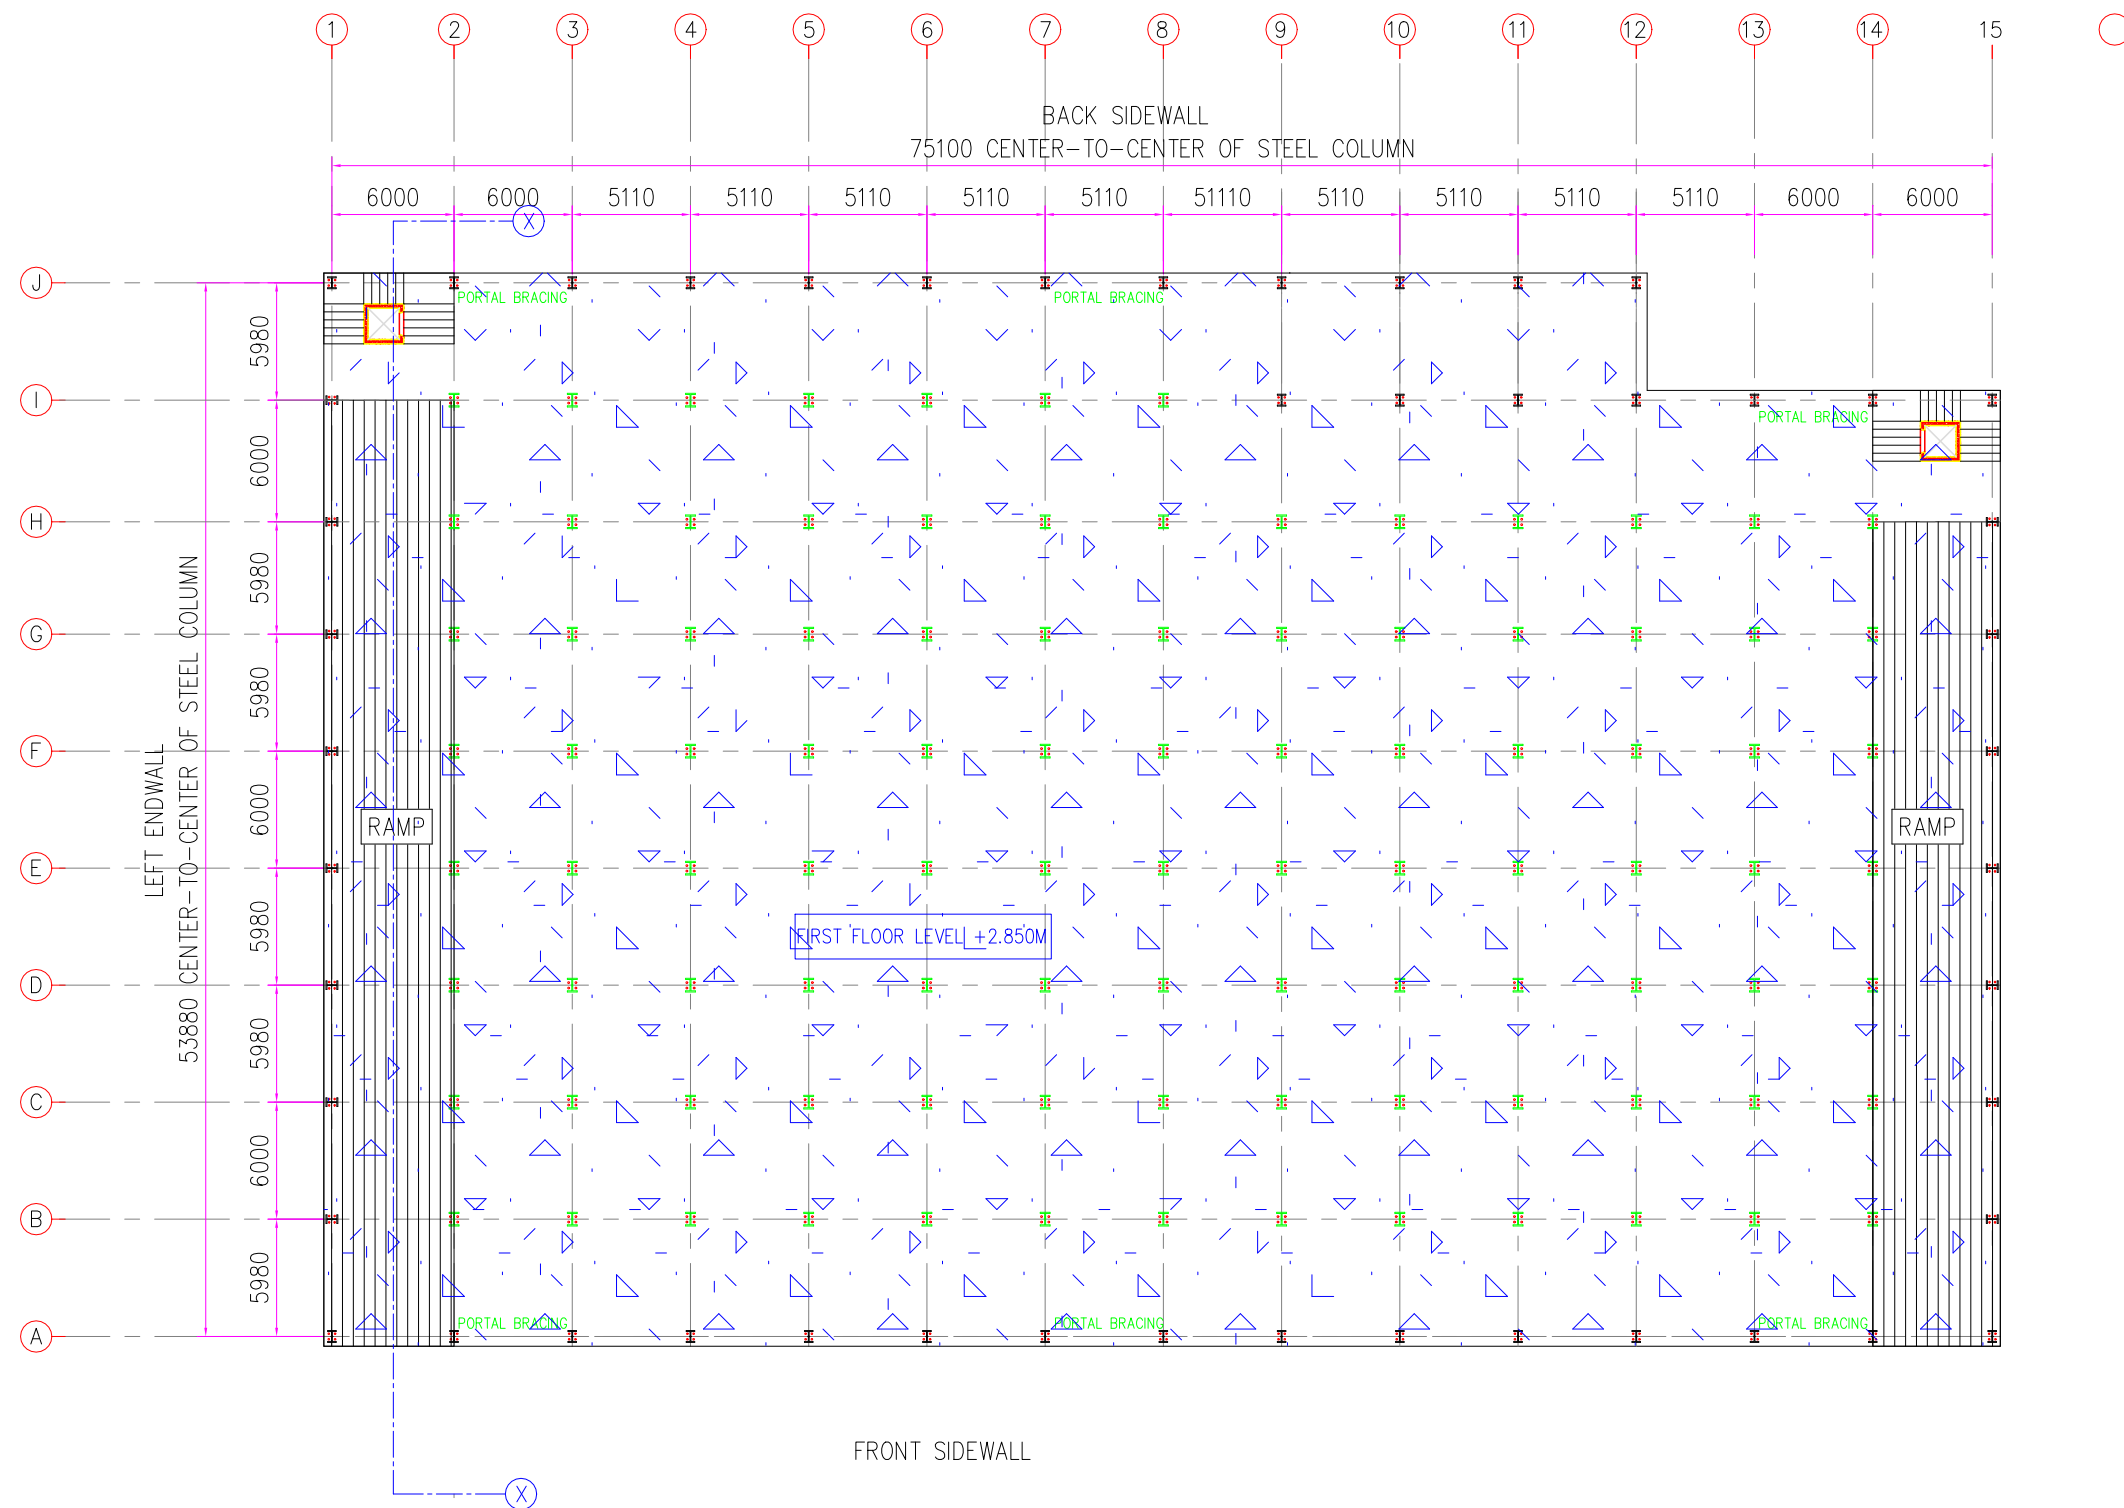

FLOOR PLAN @ LVL.+2.85m, 5.7m, 8.55m, 11.4m, 14.25m, 17.1m, 19.95m, 22.8m

NOTE:

1. ALL DIMENSION ARE IN MILLIMETER U.N.O
  2. ROOF&WALL SHEETING:0.5mm THK. RAL-9016  
FINISH: ALUZINC
- ALL DIMENSION LEVEL SHOW IN THE PROPOSAL  
DRAWING IS INDICATED ONLY, FINAL DESIGN  
DIMENSION LEVEL WILL BE SHOWN IN OUR  
APPROVAL DRAWING IN THE DESIGN STAGE

RIGHT ENDWALL

THIS DOCUMENT IS PROPOSAL  
DRAWING DATA OF SIVOKO  
NOT FOR CONSTRUCTION

|     |             |                     |     |     |     |
|-----|-------------|---------------------|-----|-----|-----|
| 00  | 06.AUG.2021 | ISSUED FOR PROPOSAL | RSG | RSG | VVJ |
| NO. | DATE        | DESCRIPTION         | DSN | DRN | CHK |

PROJECT:

PARKING STRUCTURE

CLIENT:


STEEL CONTRACTOR:



P.O. Box CS 8807,  
Comm. 7, Tema - Ghana (West Africa)  
Tel: +233-0303-910099 / +233-0302-765777  
Fax: +233-0303-951408 / +233-0302-765778  
Website: www.sivoko.net

MANUFACTURER OF P.E.B, LEAF SPRING, BOLTS  
H-BEAM & AXLE

|                    |              |              |             |
|--------------------|--------------|--------------|-------------|
| QUOTATION NO.      | BUILDING NO. | REVISION NO. | DATE        |
| Q-1392             | 01           | 00           | 07.MAY.2025 |
| DRAWING TITLE:     | DRAWING NO.  |              |             |
| COLUMN LAYOUT PLAN | 04           |              |             |

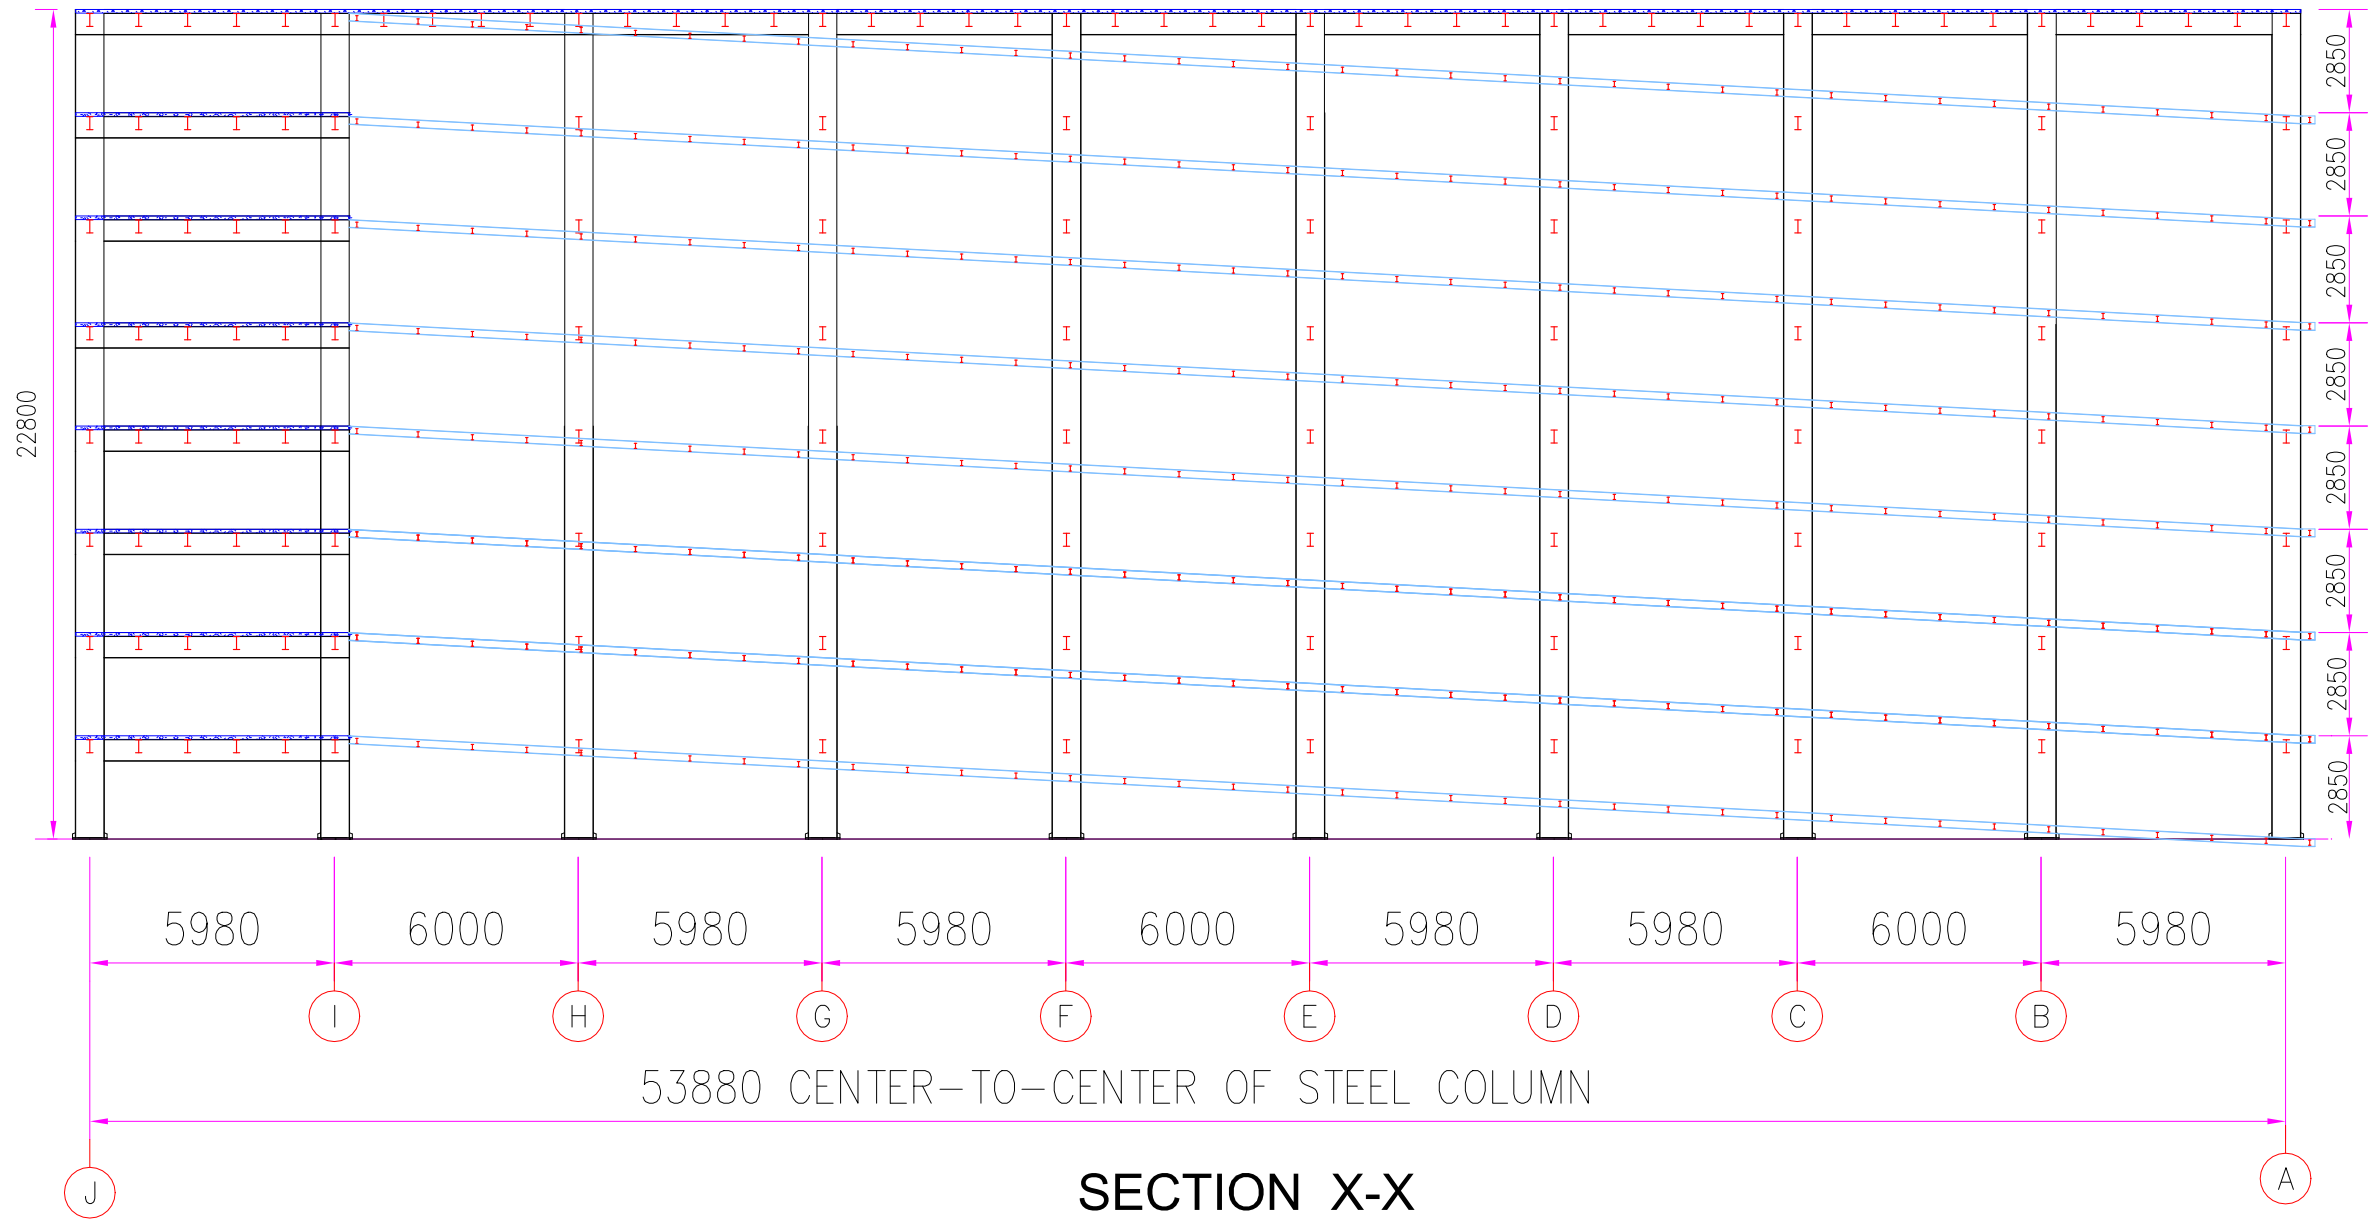

NOTE:

1. ALL DIMENSION ARE IN MILLIMETER U.N.O
  2. ROOF&WALL SHEETING:0.5mm THK. RAL-9016  
FINISH: ALUZINC
- ALL DIMENSION LEVEL SHOW IN THE PROPOSAL  
DRAWING IS INDICATED ONLY, FINAL DESIGN  
DIMENSION LEVEL WILL BE SHOWN IN OUR  
APPROVAL DRAWING IN THE DESIGN STAGE

THIS DOCUMENT IS PROPOSAL  
DRAWING DATA OF SIVOKO  
NOT FOR CONSTRUCTION

|     |             |                     |     |     |     |
|-----|-------------|---------------------|-----|-----|-----|
| 00  | 06.AUG.2021 | ISSUED FOR PROPOSAL | RSG | RSG | VVJ |
| NO. | DATE        | DESCRIPTION         | DSN | DRN | CHK |

PROJECT:  
PARKING STRUCTURE

CLIENT:  
-


STEEL CONTRACTOR:



P.O. Box CS 8807,  
Corm. 7, Tema - Ghana (West Africa)  
Tel: +233-0303-910098 / +233-0302-765777  
Fax: +233-0303-951408 / +233-0302-765778  
Website: www.sivoko.net

MANUFACTURER OF P.E.B, LEAF SPRING, BOLTS  
H-BEAM & AXLE

|                                   |                    |                    |                     |
|-----------------------------------|--------------------|--------------------|---------------------|
| QUOTATION NO.<br>Q-NNN            | BUILDING NO.<br>01 | REVISION NO.<br>00 | DATE<br>07.MAY.2025 |
| DRAWING TITLE:<br>FRAME ELEVATION |                    |                    | DRAWING NO.<br>05   |

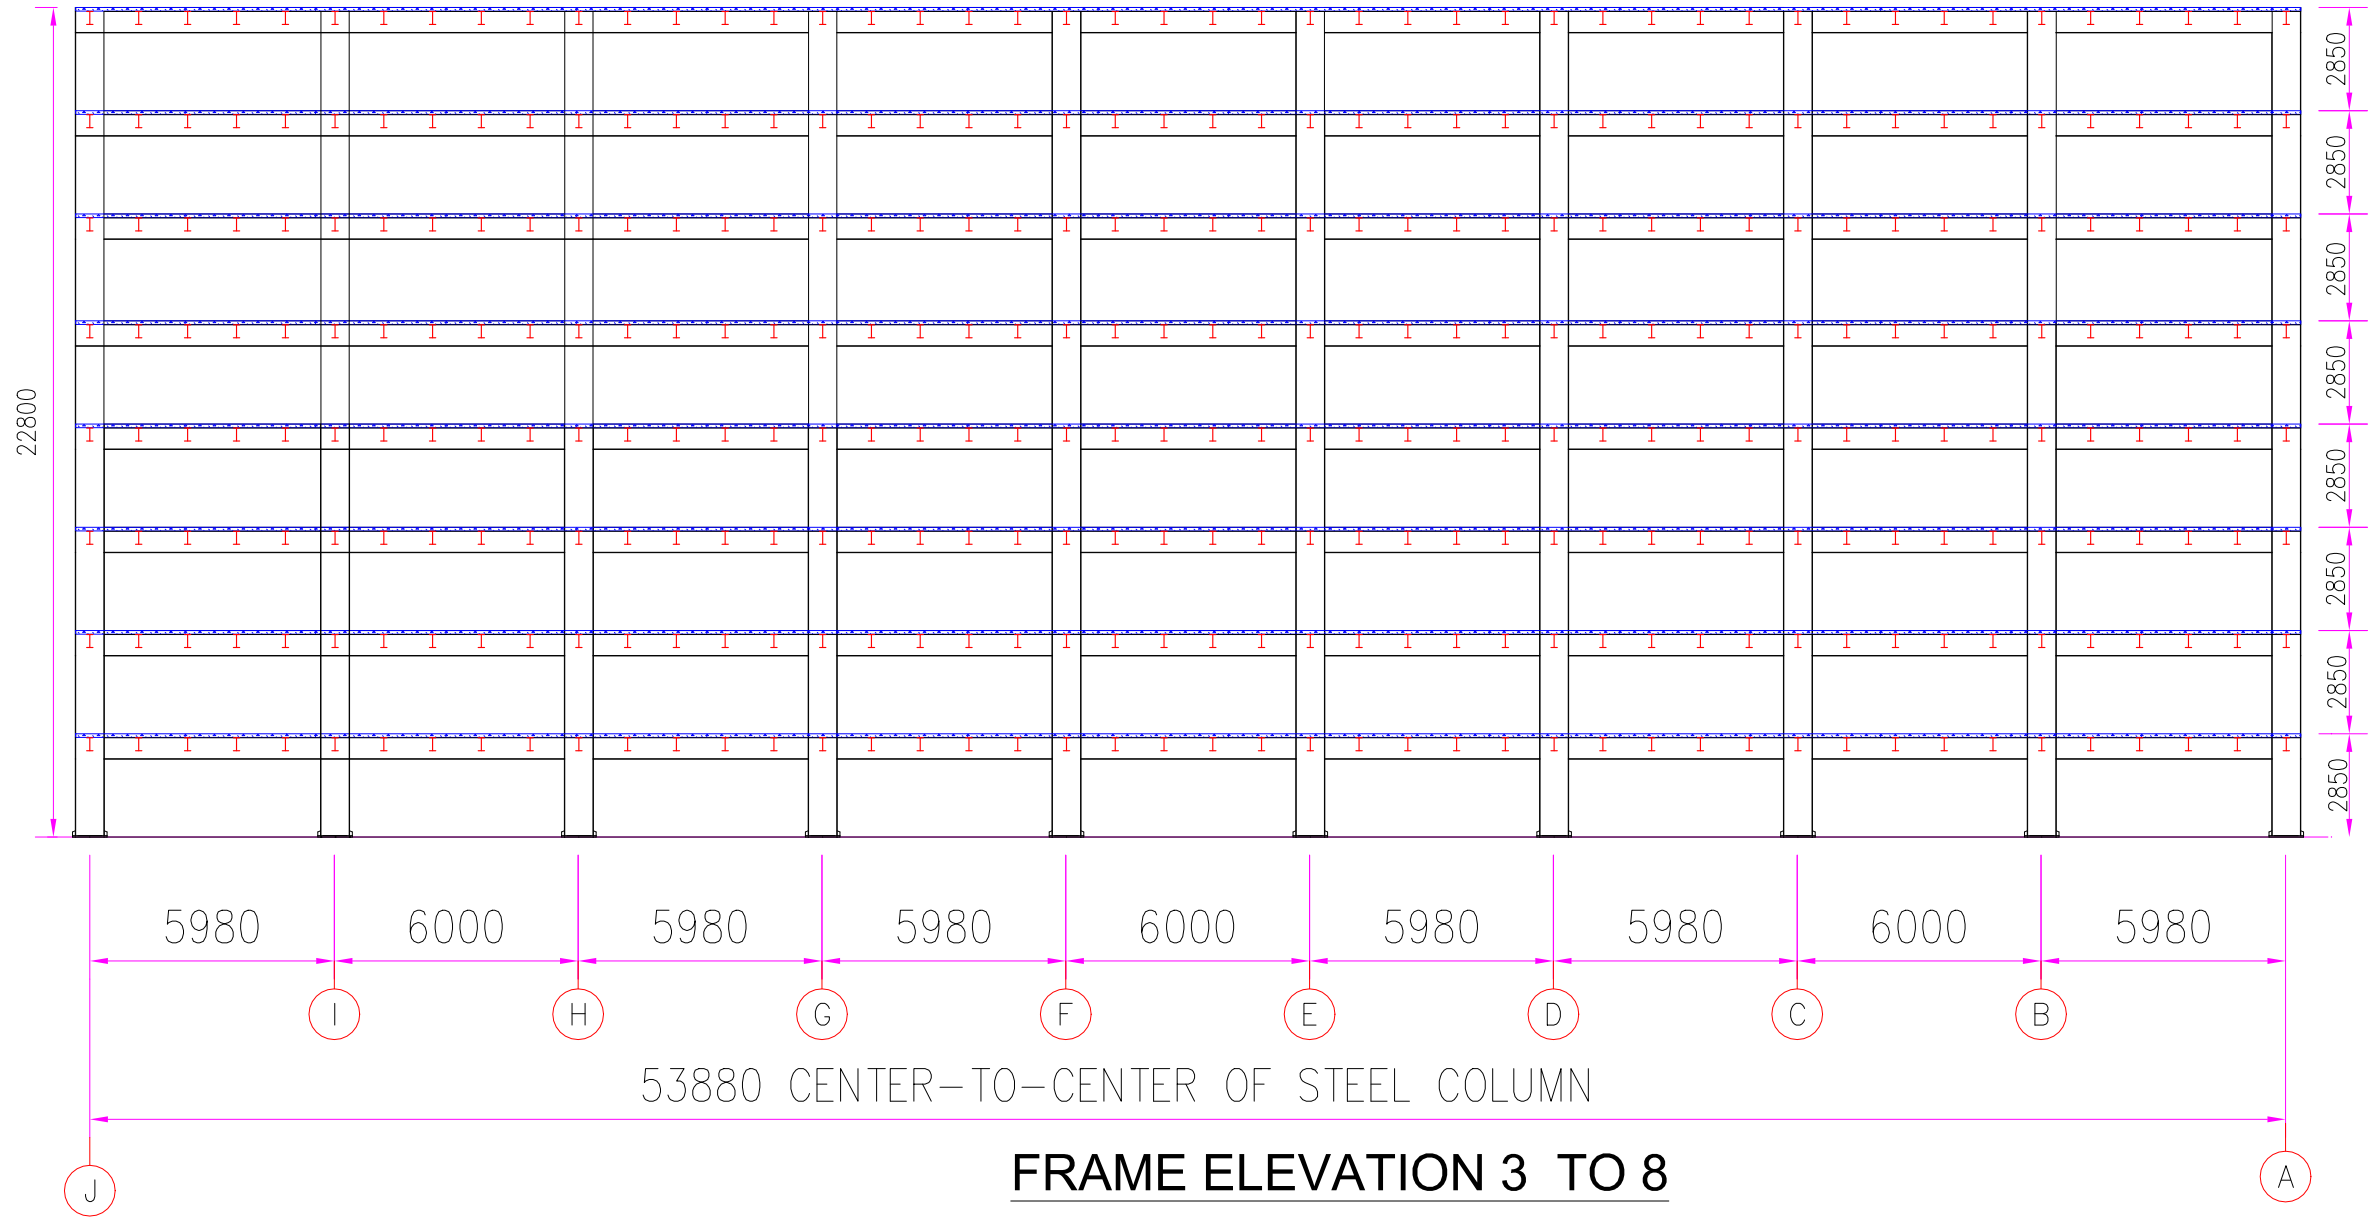

NOTE:

1. ALL DIMENSION ARE IN MILLIMETER U.N.O
  2. ROOF&WALL SHEETING:0.5mm THK. RAL-9016  
FINISH: ALUZINC
- ALL DIMENSION LEVEL SHOW IN THE PROPOSAL  
DRAWING IS INDICATED ONLY, FINAL DESIGN  
DIMENSION LEVEL WILL BE SHOWN IN OUR  
APPROVAL DRAWING IN THE DESIGN STAGE

THIS DOCUMENT IS PROPOSAL  
DRAWING DATA OF SIVOKO  
NOT FOR CONSTRUCTION

|     |             |                     |     |     |     |
|-----|-------------|---------------------|-----|-----|-----|
| 00  | 06.AUG.2021 | ISSUED FOR PROPOSAL | RSG | RSG | VVJ |
| NO. | DATE        | DESCRIPTION         | DSN | DRN | CHK |

PROJECT: PARKING STRUCTURE

CLIENT: -

STEEL CONTRACTOR:



P.O. Box CS 8807,  
Comm. 7, Tema - Ghana (West Africa)  
Tel: +233-0303-910099 / +233-0302-765777  
Fax: +233-0303-951408 / +233-0302-765778  
Website: www.sivoko.net

MANUFACTURER OF P.E.B, LEAF SPRING, BOLTS  
H-BEAM & AXLE

|                                   |                    |                    |                     |
|-----------------------------------|--------------------|--------------------|---------------------|
| QUOTATION NO.<br>Q-NNN            | BUILDING NO.<br>01 | REVISION NO.<br>00 | DATE<br>07.MAY.2026 |
| DRAWING TITLE:<br>FRAME ELEVATION |                    |                    | DRAWING NO.<br>05   |