


OUTLINE SPECIFICATIONS

Date	24 November 2025	Client					Project Location	Ghana																																					
Proposal Id	Q-1392	Project	Parking Structure				Building No.	1	Option	1	Revision	3																																	
Sr.No.	Description	PEB SPECIFICATIONS	
1.	Building type	Mezzanine Building					Area in m²	3740																																					
2.	Length in m (c/c of steel)	Ref.Dwg					Length wise bay spacing	Ref.Dwg																																					
3.	Width in m (c/c of steel)	Ref.Dwg					End wall column spacing	Ref.Dwg																																					
4.	Width modules in m	Ref.Dwg					No. of interior columns per frame	0																																					
5.	Clear height in m	Ref.Dwg					Frames symmetrical	Yes																																					
6.	Roof	Slope: NA		Cladding: NA				Rainwater drainage: Eave Gutters and Down spouts																																					
7.	Future Expansion	NA	
8.	Block Wall	NA	
9.	Column base elevations	NA (At FFL)	
10.	Wall Cladding	NA	
11.	Insulation	Roof: NA					Outer Walls: NA			Partition walls: NA																																			
12.	Openings	<table><tr><td>Outer side only</td><td colspan="5">Numbers</td><td colspan="3">Type</td><td colspan="2">Size in m (w x h)</td></tr><tr><td>Doors</td><td colspan="5">NA</td><td colspan="3">NA</td><td colspan="2">NA</td></tr><tr><td>Windows</td><td colspan="5">NA</td><td colspan="3">NA</td><td colspan="2">NA</td></tr></table>											Outer side only	Numbers					Type			Size in m (w x h)		Doors	NA					NA			NA		Windows	NA					NA			NA	
		Outer side only	Numbers					Type			Size in m (w x h)																																		
		Doors	NA					NA			NA																																		
		Windows	NA					NA			NA																																		
		Location of doors & bracing	
		Side Wall Gridlines	1-2	2-3	3-4	4-5	5-6	6-7	7-8	8-9	9-10	10-11	11-12	Right End Wall																															
		Front Side Wall		XP				XP				XP																																	
		Back Side Wall		XP				XP				XP																																	
		End Wall Axes		A-B	B-C	C-D	D-E	E-F	F-G	G-H	H-I	Back Side Wall																																	
		Right End Wall	
		Left End Wall	
		13.	Extensions	Eave: NA	Gable: NA	Canopies:									Parapet: NA																														
Extension in m: NA						Location: NA																																							
Clear height in m: NA						Rainwater drainage: NA																																							
Slope: NA						Soffit panels: NA																																							
14.	Accessories	Wall Lights:		NA						Roof Monitor		NA	Any other: NA																																
		Skylights:		NA						Cage ladder		NA																																	
		Turbo Ventilators:		NA						Ridge Ventilators:		NA																																	
15.	For Frames (Standard codes and manuals used in design - 2010 Metal Building Systems Manual,	DESIGN LOADS				LOCATION - CLIMATIC DATA					SERVICEABILITY CRITERIA																																		
		Dead Load in kN/m²		0.10		Max wind speed in m/s			36.11	Frames		H/100, L/150																																	
		Live Load in kN/m²		0.575		Exposure category			B	Purlins		Span/150																																	
		Collateral load in kN/m²		0.05		Max rainfall intensity in mm/hr.			150	Girts		Span/120																																	
		Any other		NA		Seismic Design category (Coefficient)			II (0.33)	Crane Beams		Span/600																																	

	NAUS07, AISC05, UBC 1997) Design Software: MBS			Max Temperature variation in °C	20	Mezzanine Beams	Span/240
16.	Mezzanine	Location: Ref.Dwg. Loading: Live load in kN/m²: 5 Dead load in kN/m²: 2.5 Collateral load in kN/m²: 0		Dimensions: Length in m: Ref.Dwg. Width in m: Ref.Dwg. Top of the Mezzanine Floor in m: Ref.Dwg. Depth of mezzanine slab in mm: 100 Deck sheeting thickness: 0.7mm		Accessories: Staircase Nos.: 2 Location: Ref.Dwg. Type: Double staircase with intermediate landing Handrail: All round	
17.	Partition Walls	NA					
18.	Jack Beam	NA					
19.	Assumptions & Remarks	Built-up sections are made from hot rolled plates conforming to ASTM A-572 Gr50 (345MPa) steel. The plates are joined together with double side welding. Sections consist of minimum 5mm for flange & minimum 4mm for web thickness. Cold formed sections thickness 1.5 mm or more are made of hot rolled sheet of Gr50 (345 MPa) steel. Primary structural connections are high strength machine bolts conforming to ASTM A325 or equivalent. Sheeting profile considered is of 1 m standard width, formed from a coil of 1.220 m. Single colour sheeting of up to maximum 9 m lengths is considered. Not considered in scope: Foundation, Block wall (Civil work). Crane Bridge, Trolley, Rail and its installation.					

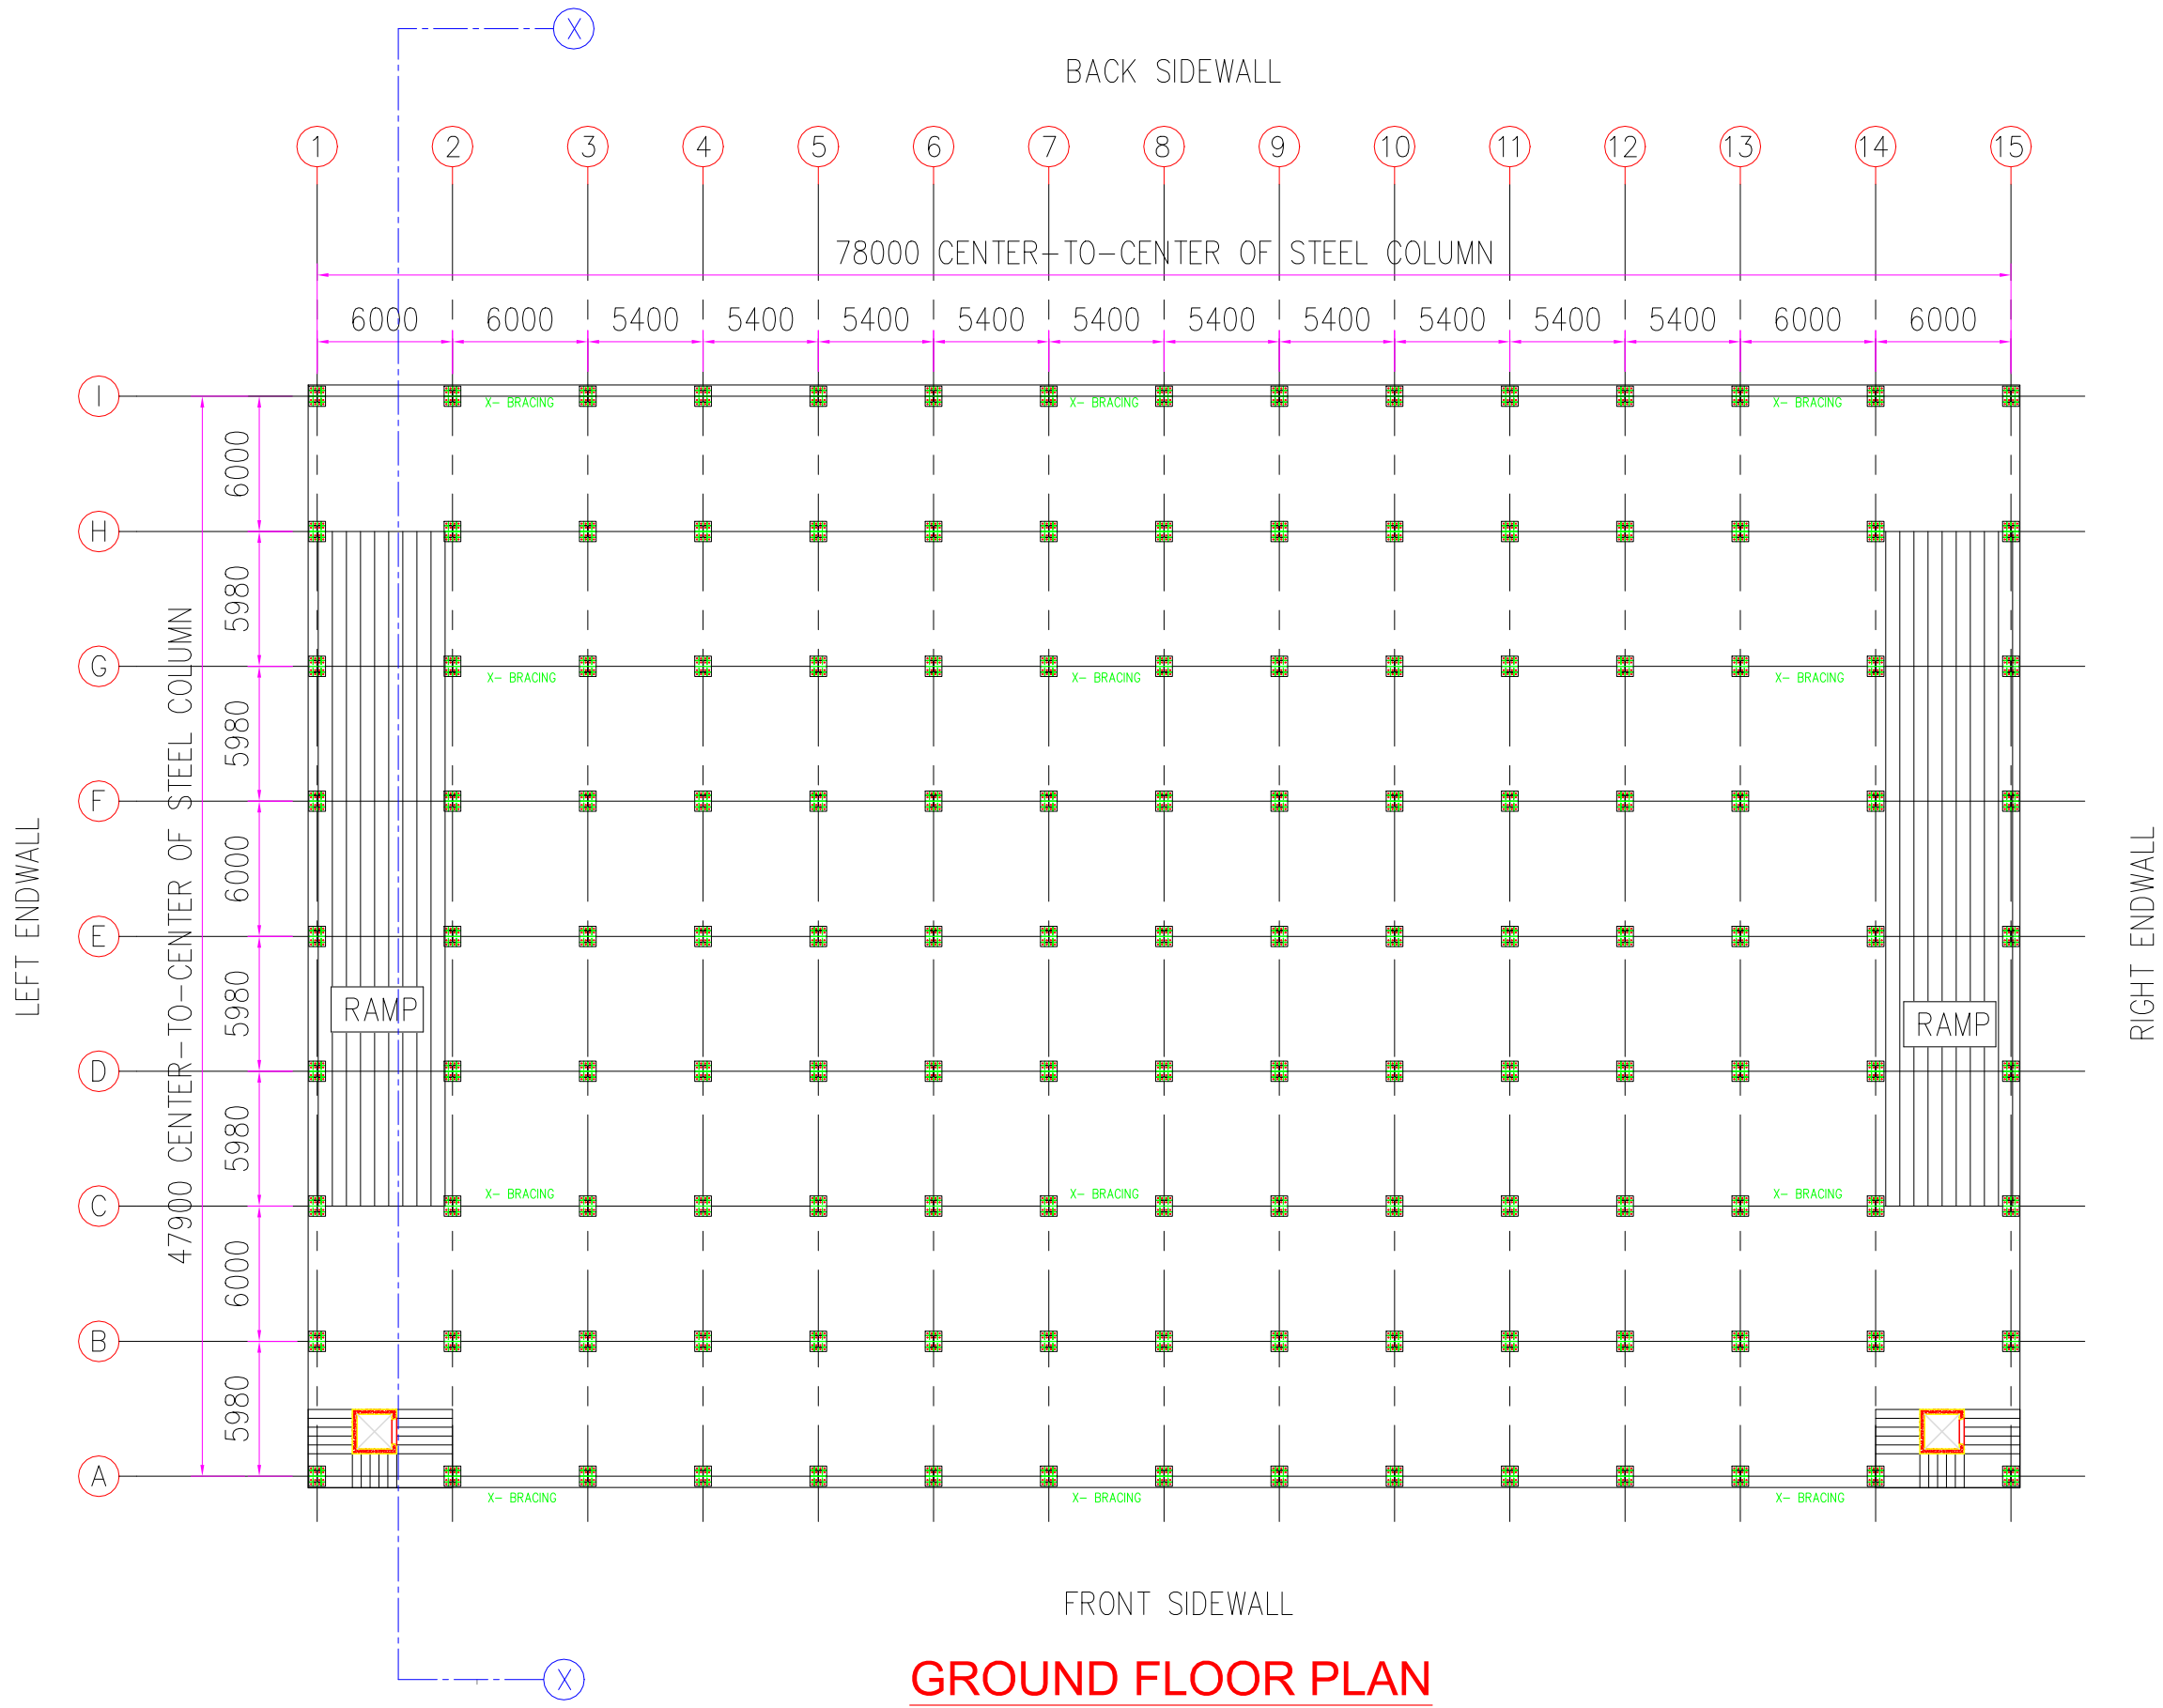

NOTE:

1. ALL DIMENSION ARE IN MILLIMETER U.N.O

2. ROOF&WALL SHEETING:0.5mm THK. RAL-9016

FINISH: ALUZINC

ALL DIMENSION LEVEL SHOW IN THE PROPOSAL

DRAWING IS INDICATED ONLY, FINAL DESIGN

DIMENSION LEVEL WILL BE SHOWN IN OUR

APPROVAL DRAWING IN THE DESIGN STAGE

THIS DOCUMENT IS PROPOSAL
DRAWING DATA OF SIVOKO
NOT FOR CONSTRUCTION

00	24.NOV.25	ISSUED FOR PROPOSAL	RSG	RSG	VVJ
NO.	DATE	DESCRIPTION	DSN	DRN	CHK

PROJECT: PARKING STRUCTURE

CLIENT: -


STEEL CONTRACTOR:



P.O. Box CS 8807,
Comm. 7, Tema - Ghana (West Africa)
Tel: +233-0303-910099 / +233-0302-765777
Fax: +233-0303-951408 / +233-0302-765778
Website: www.sivoko.net

MANUFACTURER OF P.E.B, LEAF SPRING, BOLTS
H-BEAM & AXLE

QUOTATION NO.	BUILDING NO.	REVISION NO.	DATE
Q-1392	01	03	24.NOV.2025
DRAWING TITLE:	COLUMN LAYOUT PLAN		DRAWING NO.
			04

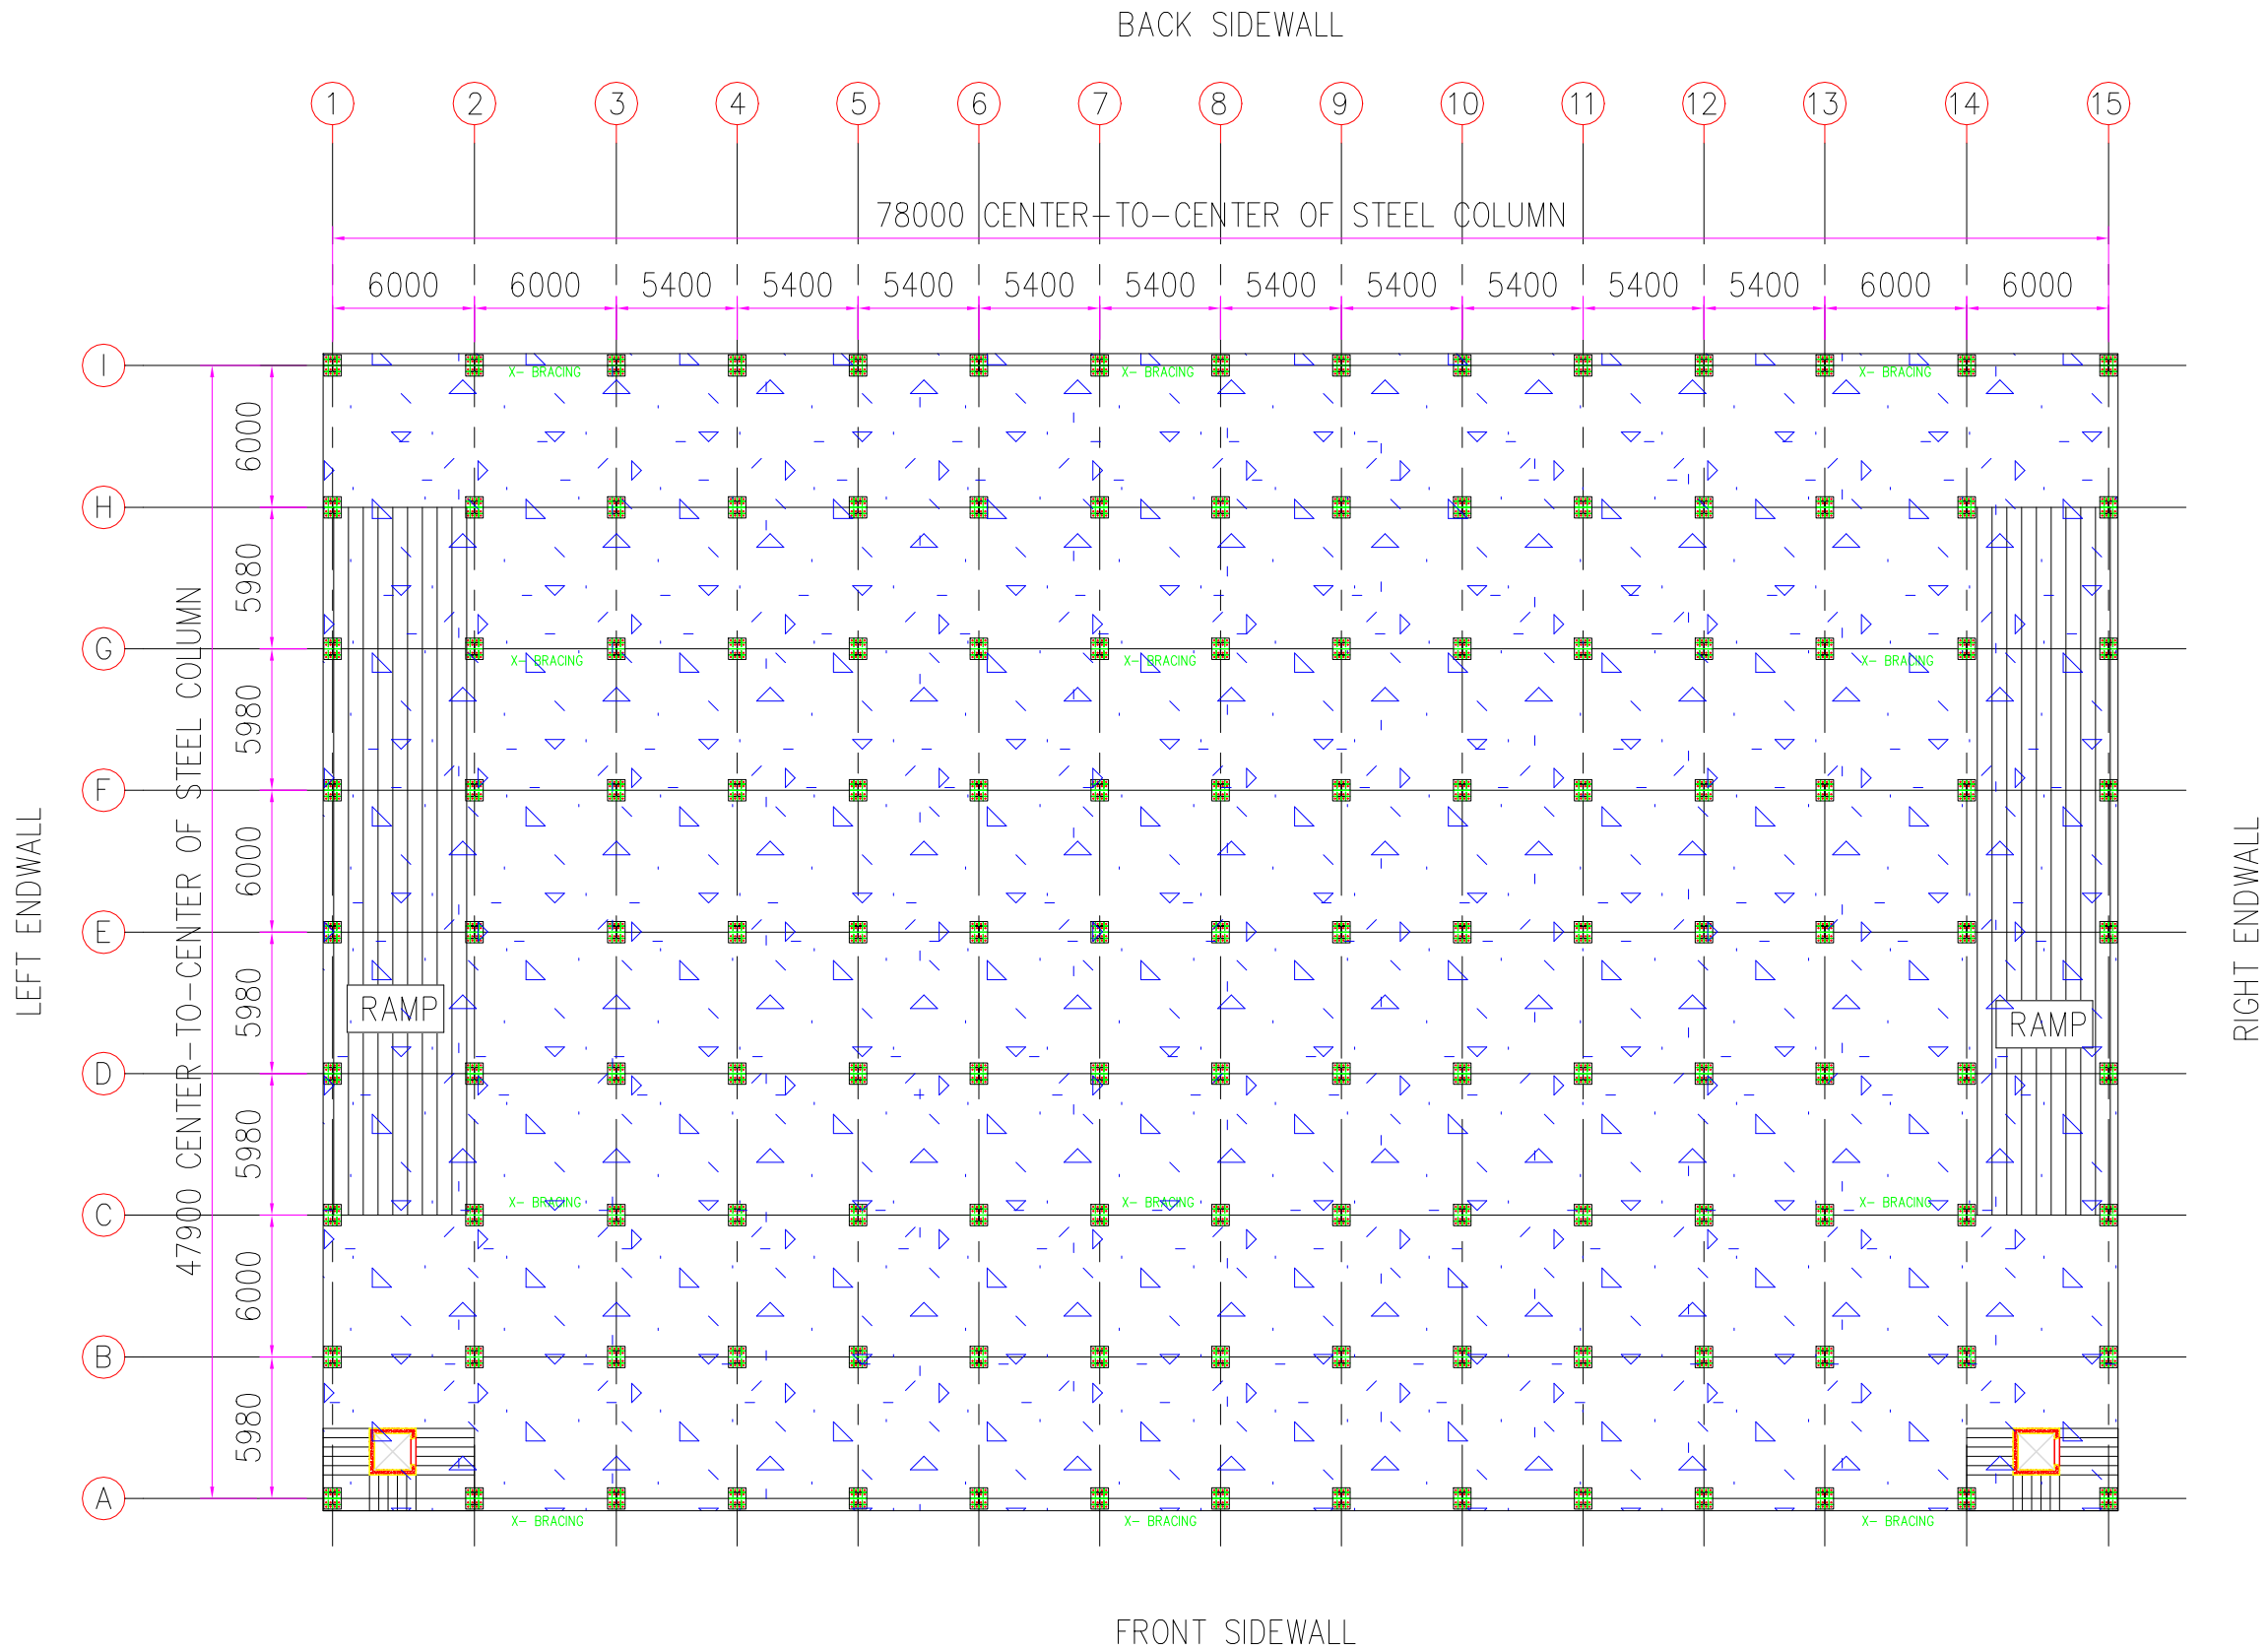

FLOOR PLAN @ LVL.+3.1m, 6.2m, 9.3m, 12.4m, 15.5m, 18.6m, 21.7m, 24.8m, 27.9m, 31.0m

NOTE:

1. ALL DIMENSION ARE IN MILLIMETER U.N.O
2. ROOF&WALL SHEETING:0.5mm THK. RAL-9016
FINISH: ALUZINC

ALL DIMENSION LEVEL SHOW IN THE PROPOSAL
DRAWING IS INDICATED ONLY, FINAL DESIGN
DIMENSION LEVEL WILL BE SHOWN IN OUR
APPROVAL DRAWING IN THE DESIGN STAGE

THIS DOCUMENT IS PROPOSAL
DRAWING DATA OF SIVOKO
NOT FOR CONSTRUCTION

00	24.NOV.25	ISSUED FOR PROPOSAL	RSG	RSG	VVJ
NO.	DATE	DESCRIPTION	DSN	DRN	CHK

PROJECT: PARKING STRUCTURE

CLIENT: -

STEEL CONTRACTOR:




P.O. Box CS 8807,
Comm. 7, Tema - Ghana (West Africa)
Tel: +233-0303-910099 / +233-0302-765777
Fax: +233-0303-951408 / +233-0302-765778
Website: www.sivoko.net

MANUFACTURER OF P.E.B, LEAF SPRING, BOLTS
H-BEAM & AXLE

QUOTATION NO.	BUILDING NO.	REVISION NO.	DATE
Q-1392	01	03	24.NOV.2025

DRAWING TITLE: COLUMN LAYOUT PLAN
DRAWING NO: 05

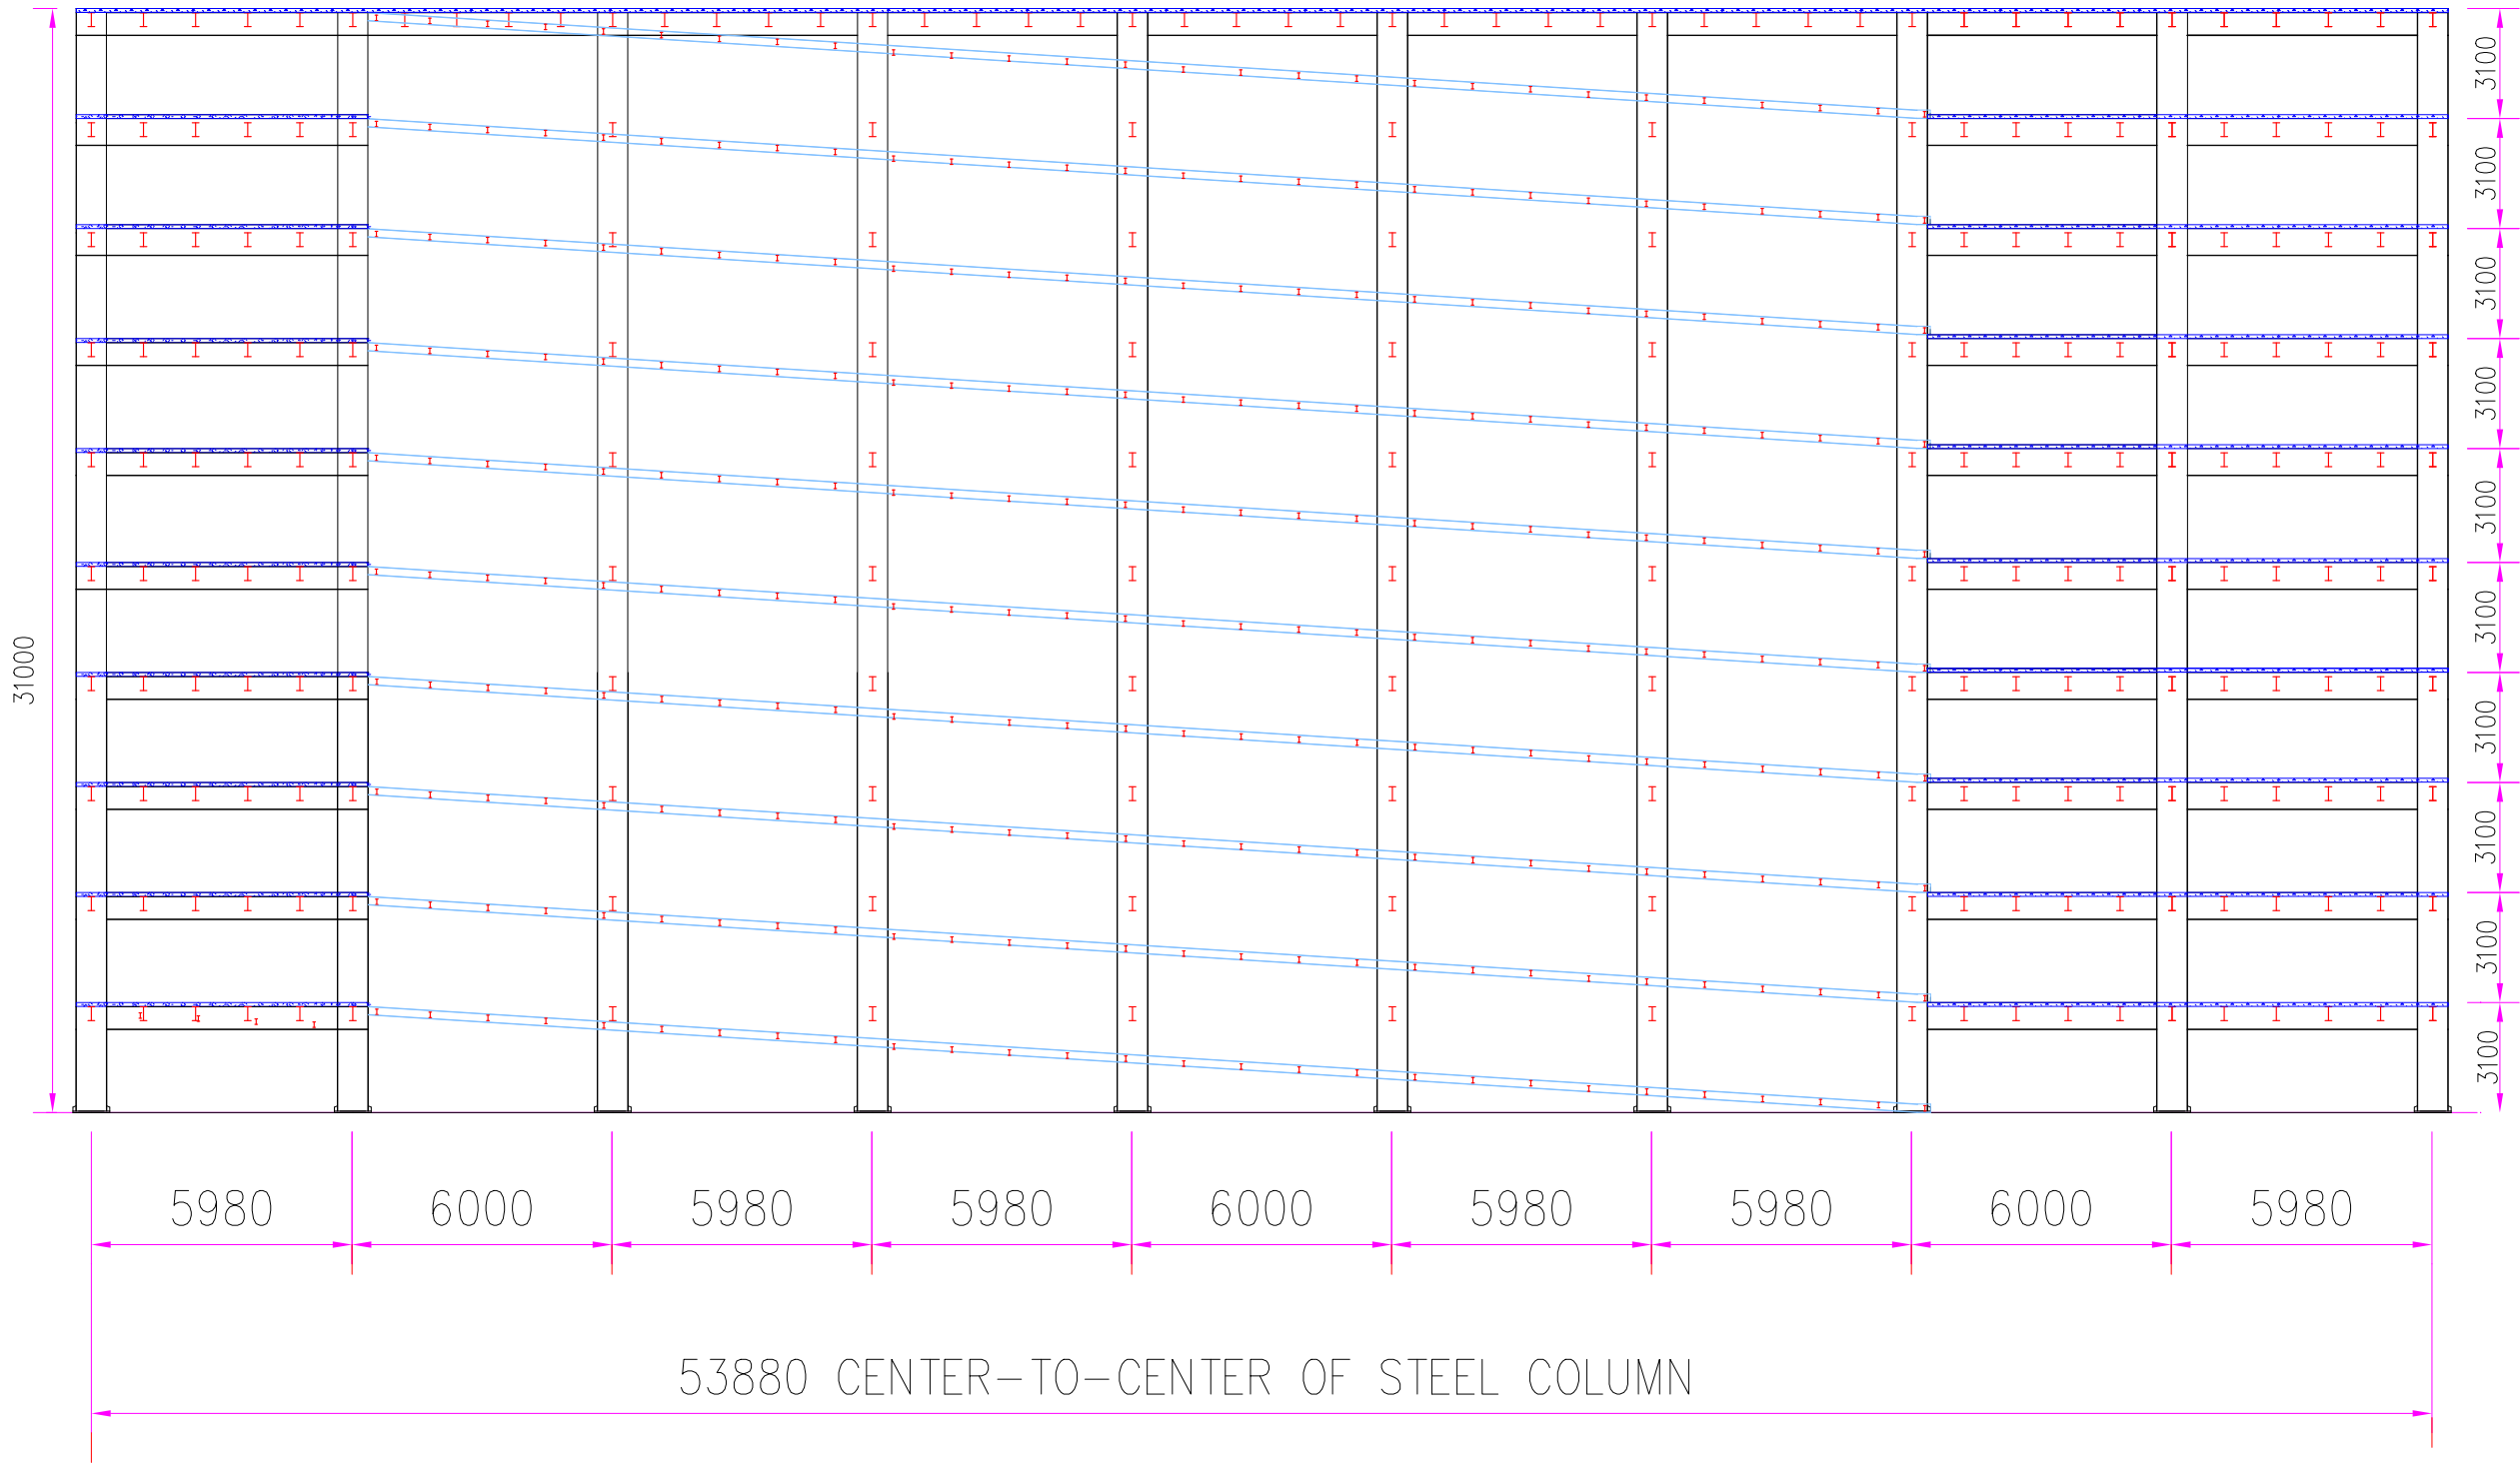

SECTION X-X

NOTE:

1. ALL DIMENSION ARE IN MILLIMETER U.N.O
 2. ROOF&WALL SHEETING:0.5mm THK. RAL-9016
- FINISH: ALUZINC

ALL DIMENSION LEVEL SHOW IN THE PROPOSAL
DRAWING IS INDICATED ONLY, FINAL DESIGN
DIMENSION LEVEL WILL BE SHOWN IN OUR
APPROVAL DRAWING IN THE DESIGN STAGE

THIS DOCUMENT IS PROPOSAL
DRAWING DATA OF SIVOKO
NOT FOR CONSTRUCTION

00	24.NVO.25	ISSUED FOR PROPOSAL	RSG	RSG	VVJ
NO.	DATE	DESCRIPTION	DSN	DRN	CHK

PROJECT:
PARKING STRUCTURE

CLIENT:
-


STEEL CONTRACTOR:



P.O. Box CS 8807,
Comm. 7, Tema - Ghana (West Africa)
Tel: +233-0303-910099 / +233-0302-765777
Fax: +233-0303-951408 / +233-0302-765778
Website: www.sivoko.net

MANUFACTURER OF P.E.B, LEAF SPRING, BOLTS
H-BEAM & AXLE

QUOTATION NO.	BUILDING NO.	REVISION NO.	DATE
Q-NNN	01	00	24.NVO.2025
DRAWING TITLE:	FRAME ELEVATION	DRAWING NO.	05

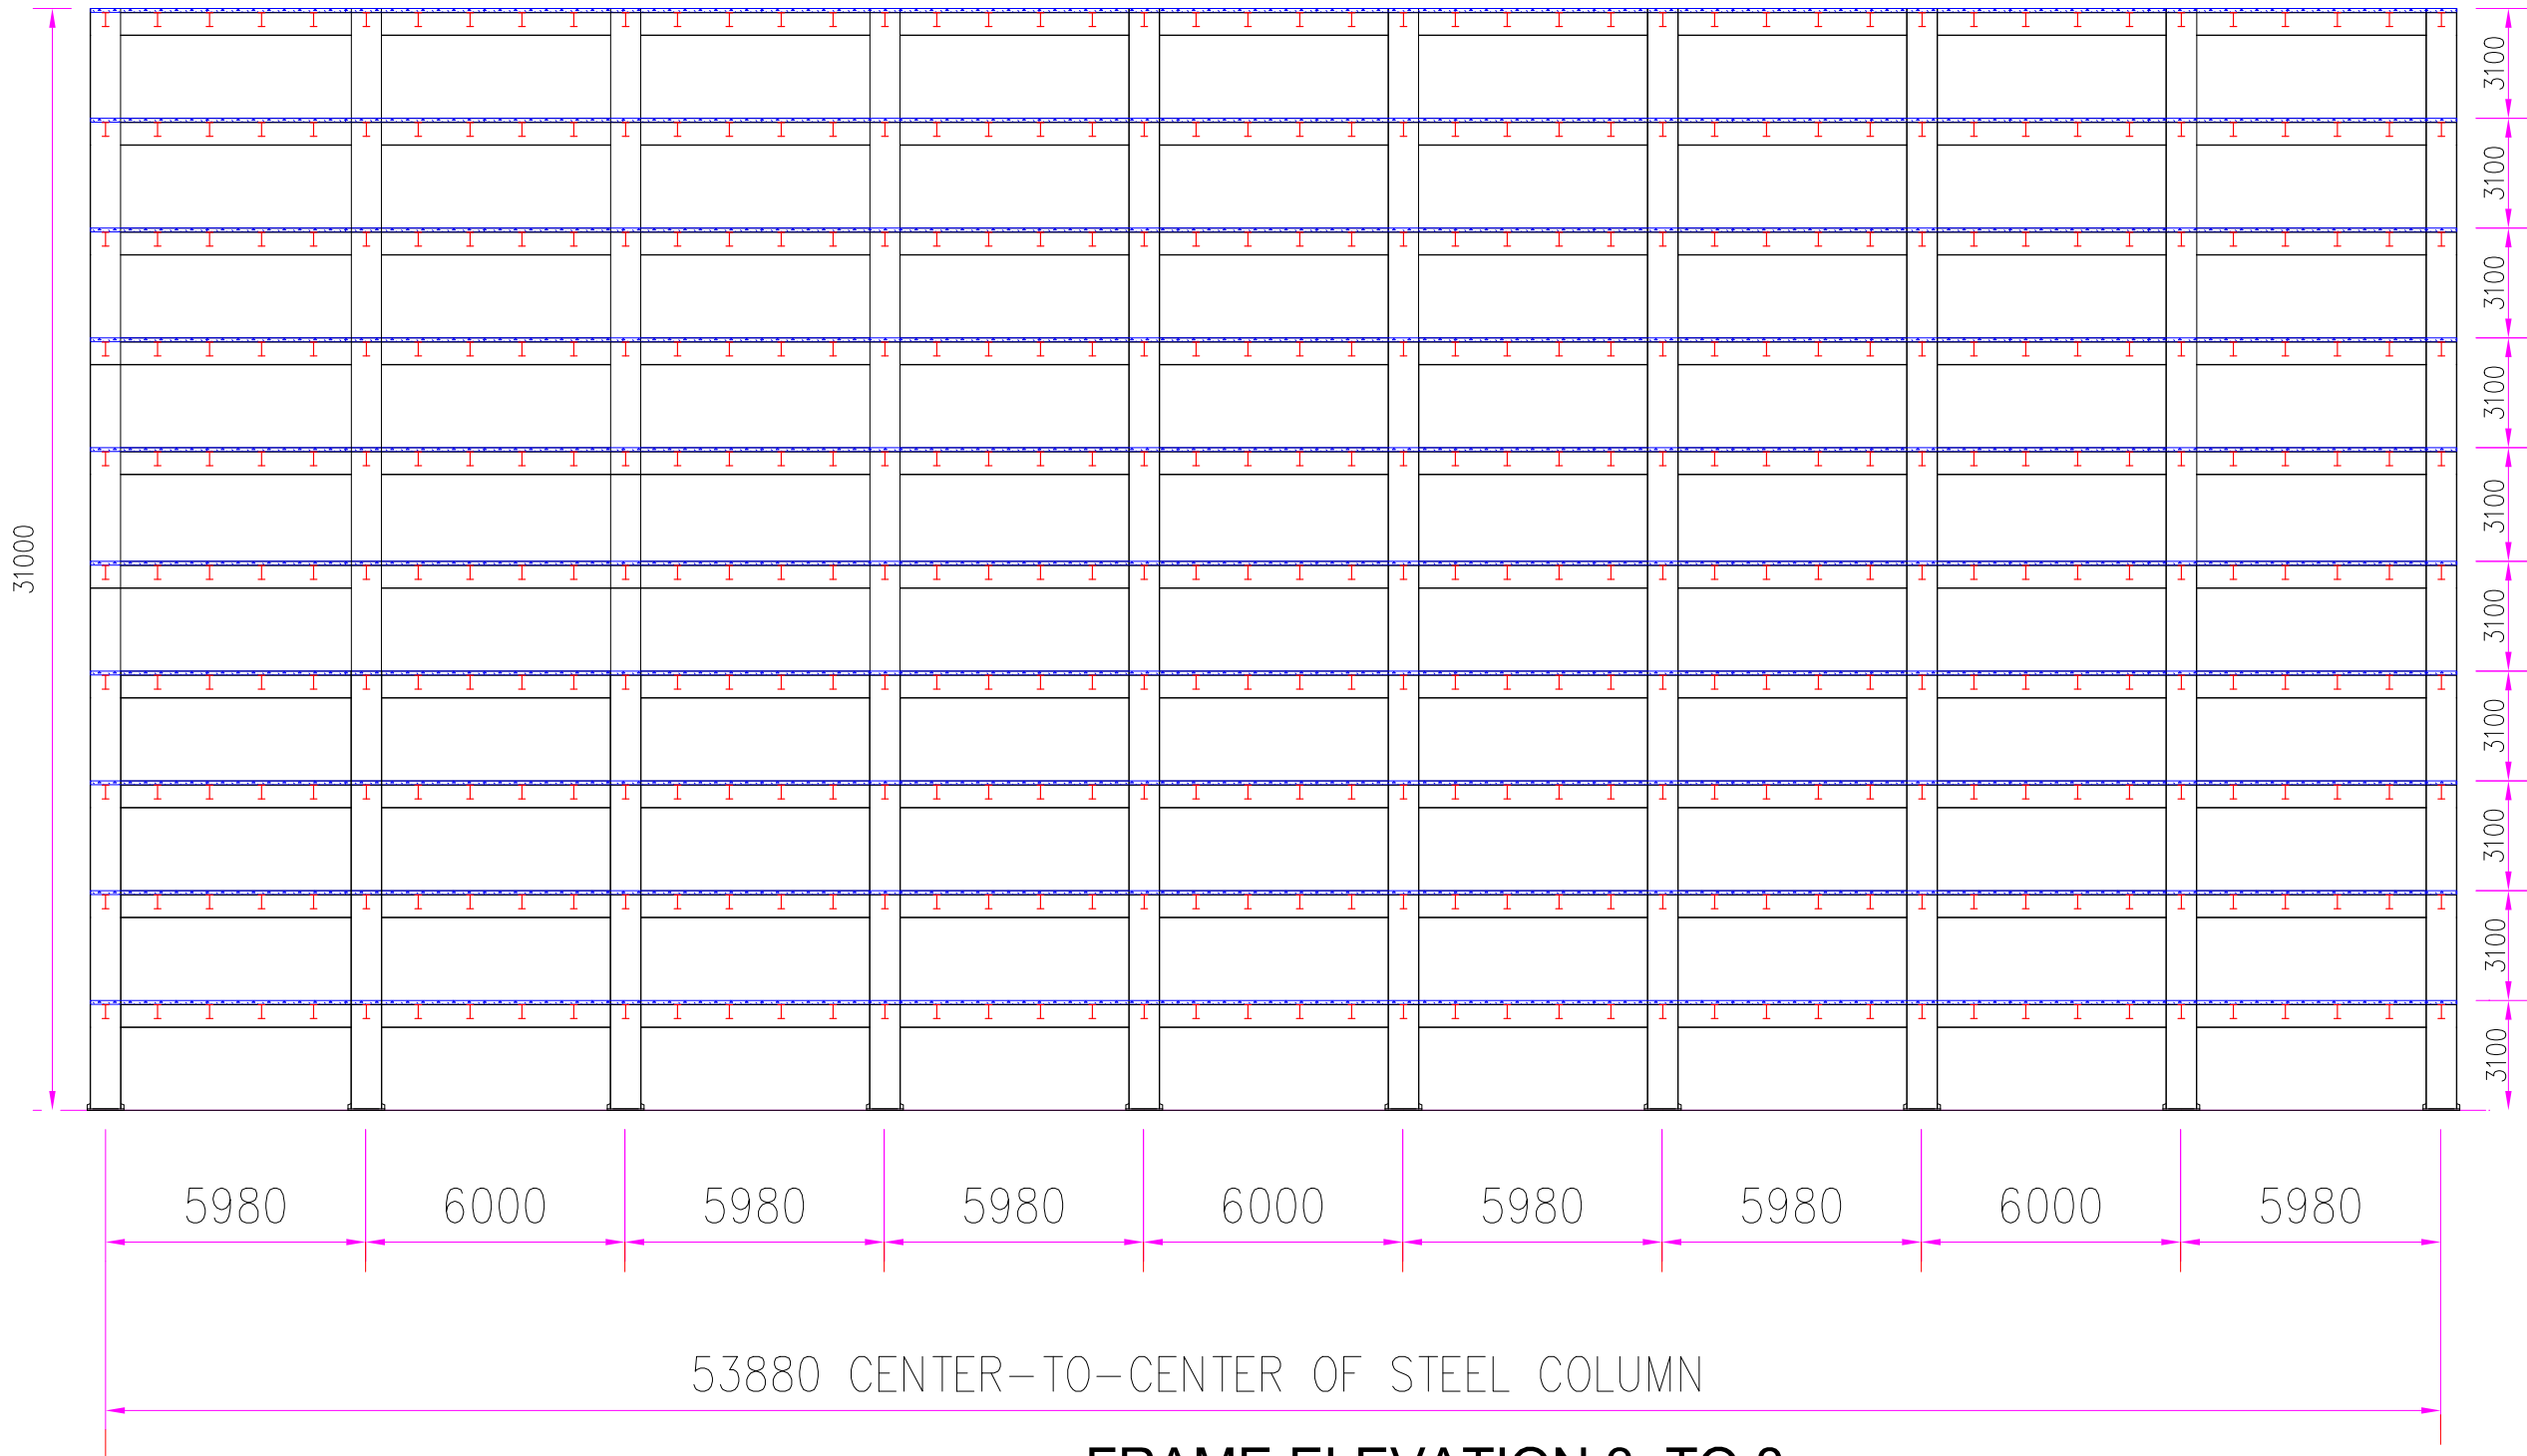

FRAME ELEVATION 3 TO 8

NOTE:

- 1. ALL DIMENSION ARE IN MILLIMETER U.N.O
 - 2. ROOF&WALL SHEETING:0.5mm THK. RAL-9016
- FINISH: ALUZINC

ALL DIMENSION LEVEL SHOW IN THE PROPOSAL
DRAWING IS INDICATED ONLY, FINAL DESIGN
DIMENSION LEVEL WILL BE SHOWN IN OUR
APPROVAL DRAWING IN THE DESIGN STAGE

THIS DOCUMENT IS PROPOSAL
DRAWING DATA OF SIVOKO
NOT FOR CONSTRUCTION

00	24.NVO.25	ISSUED FOR PROPOSAL	RSG	RSG	VVJ
NO.	DATE	DESCRIPTION	DSN	DRN	CHK

PROJECT:
PARKING STRUCTURE

CLIENT:
-

STEEL CONTRACTOR:



P.O. Box CS 8807,
Comm. 7, Tema - Ghana (West Africa)
Tel: +233-0303-910099 / +233-0302-765777
Fax: +233-0303-951408 / +233-0302-765778
Website: www.sivoko.net

MANUFACTURER OF P.E.B, LEAF SPRING, BOLTS
H-BEAM & AXLE

QUOTATION NO.	BUILDING NO.	REVISION NO.	DATE
Q-NNN	01	00	24.NVO.2025
DRAWING TITLE:	FRAME ELEVATION	DRAWING NO.	05