



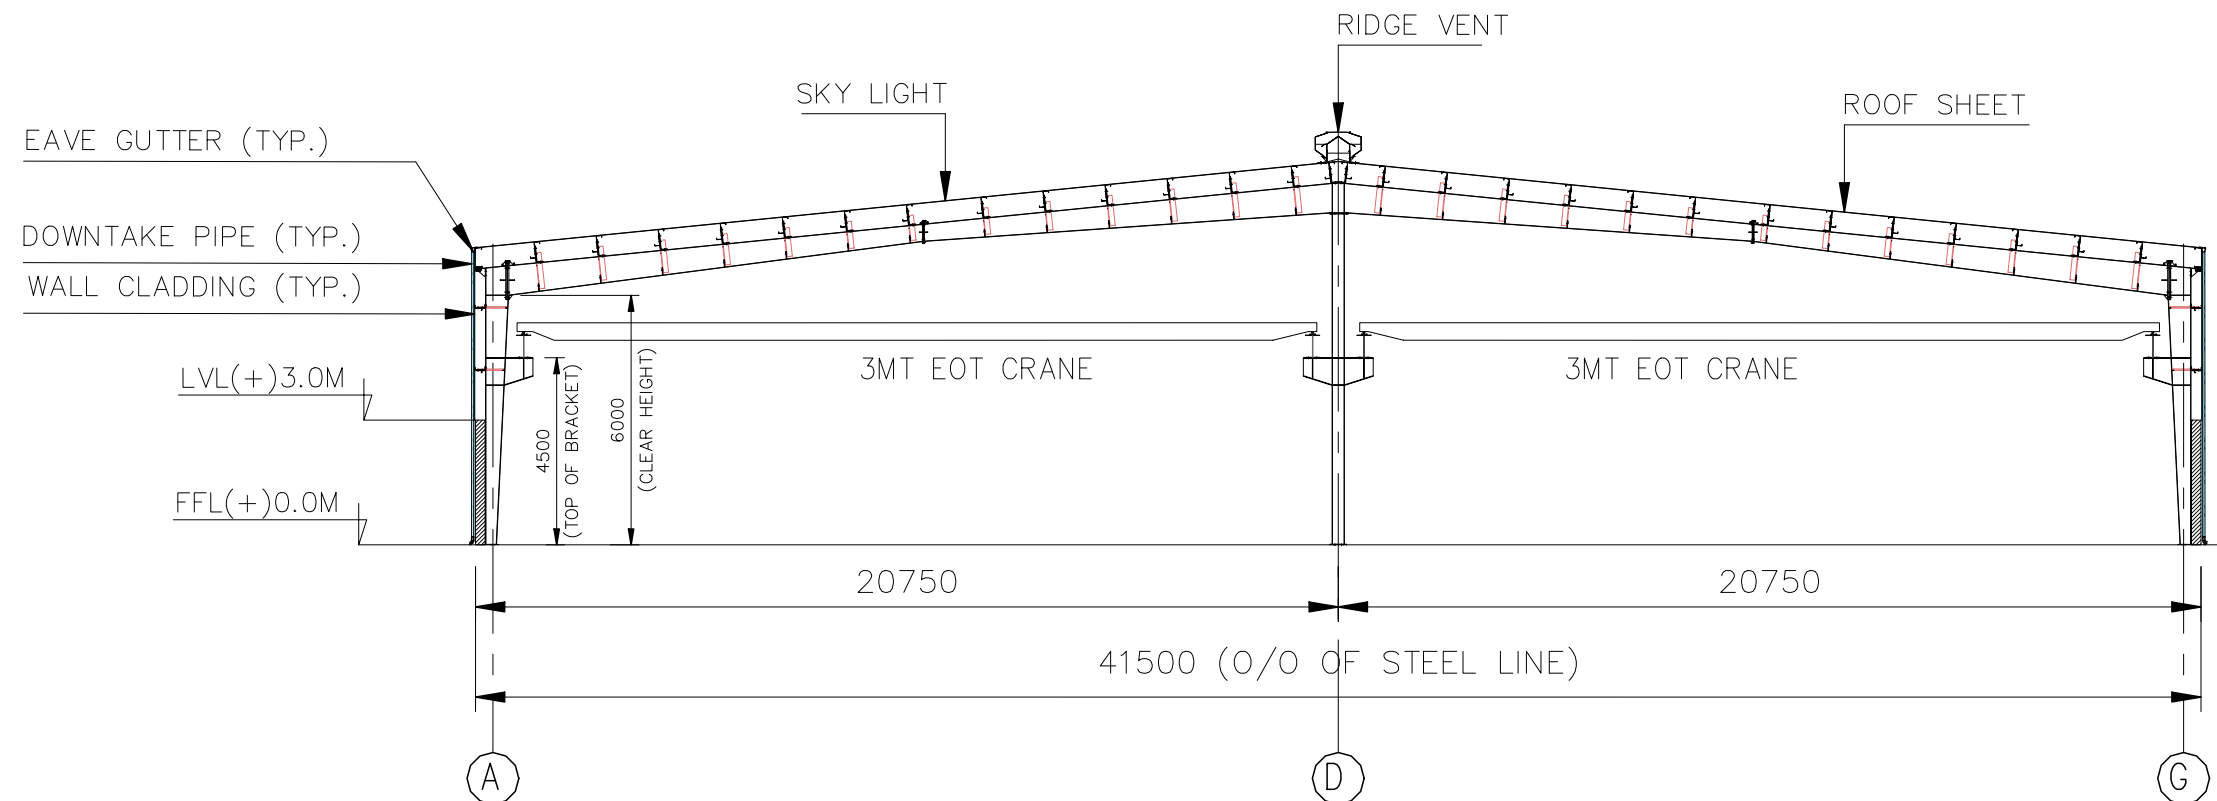

TYPICAL FRAME ELEVATION

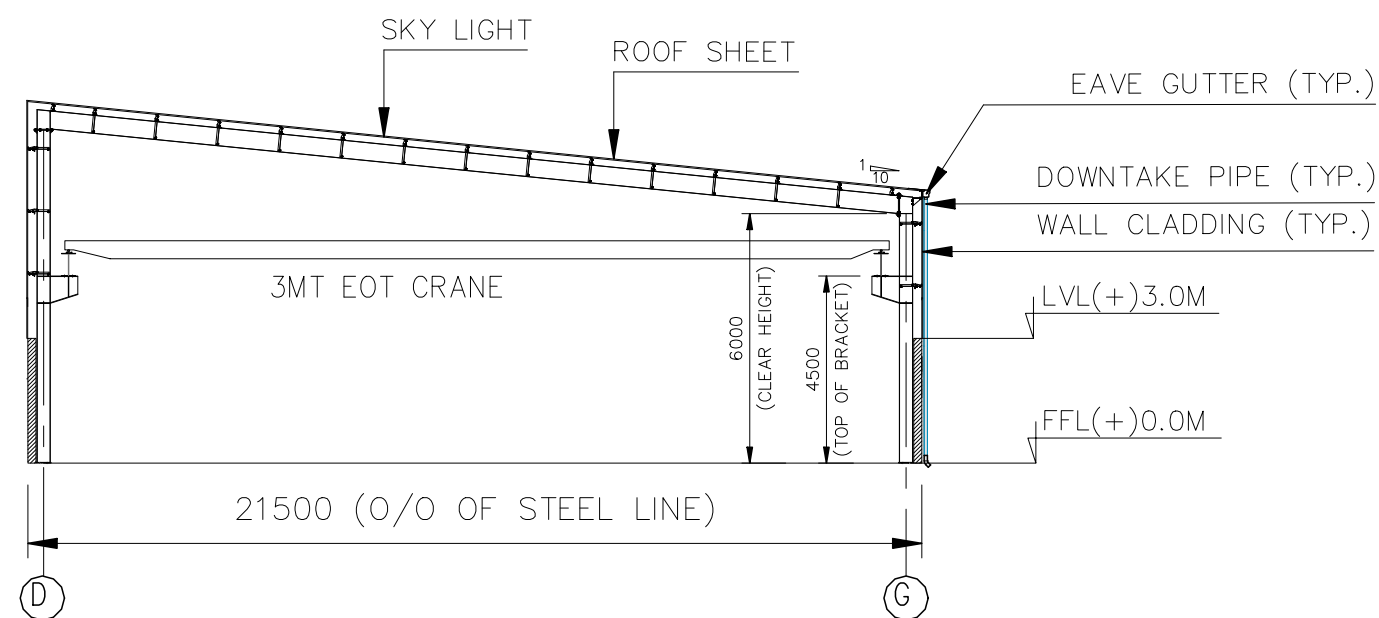

TYPICAL FRAME ELEVATION

LOYA PEB		
DESIGN: AAB	DRAFT: AAB	CHECK: VVJ
PROJECT LOCATION : MALEGAON		
RIGID FRAME ELEVATION		